ZONA DV	CLA	Nº TAL.	DATA PL.	ÁREA (ha)	VAR.
1 7.09 %	CR	1	2026	14.74	REFORMA
TOTAL PLANTIO				14.74	--------

ÁREAS	(ha)	(%)
PLANTIO	14.74	94.92
CARREADORES	0.79	5.08
OUTROS	0.00	0.00
SUB TOTAL AGRICULTÁVEL	15.53	100.00
AP.P.	0.00	0.00
ÁRVORES	0.00	0.00
OUTROS	0.00	0.00
SUB TOTAL NÃO AGRICULT.	0.00	0.00
ÁREA TOTAL	15.53	100.00


C. NÍVEL: 2887.51 m/l 0.66 ha 4.28 %

LEGENDA

- FAZENDA
- TALHÃO
- CURVA DE NÍVEL
- CARREADOR
- CONFRONTANTE
- REDE ELÉTRICA
- TRAJETO VAZIO
- TRAJETO CARREGADO


PLANTIO MANUAL - ESPAÇAMENTO: 1.50 X 1.50
TIRO MÉDIO ESTIMADO: 000.00m

Clealco
Açúcar, Etanol e Energia

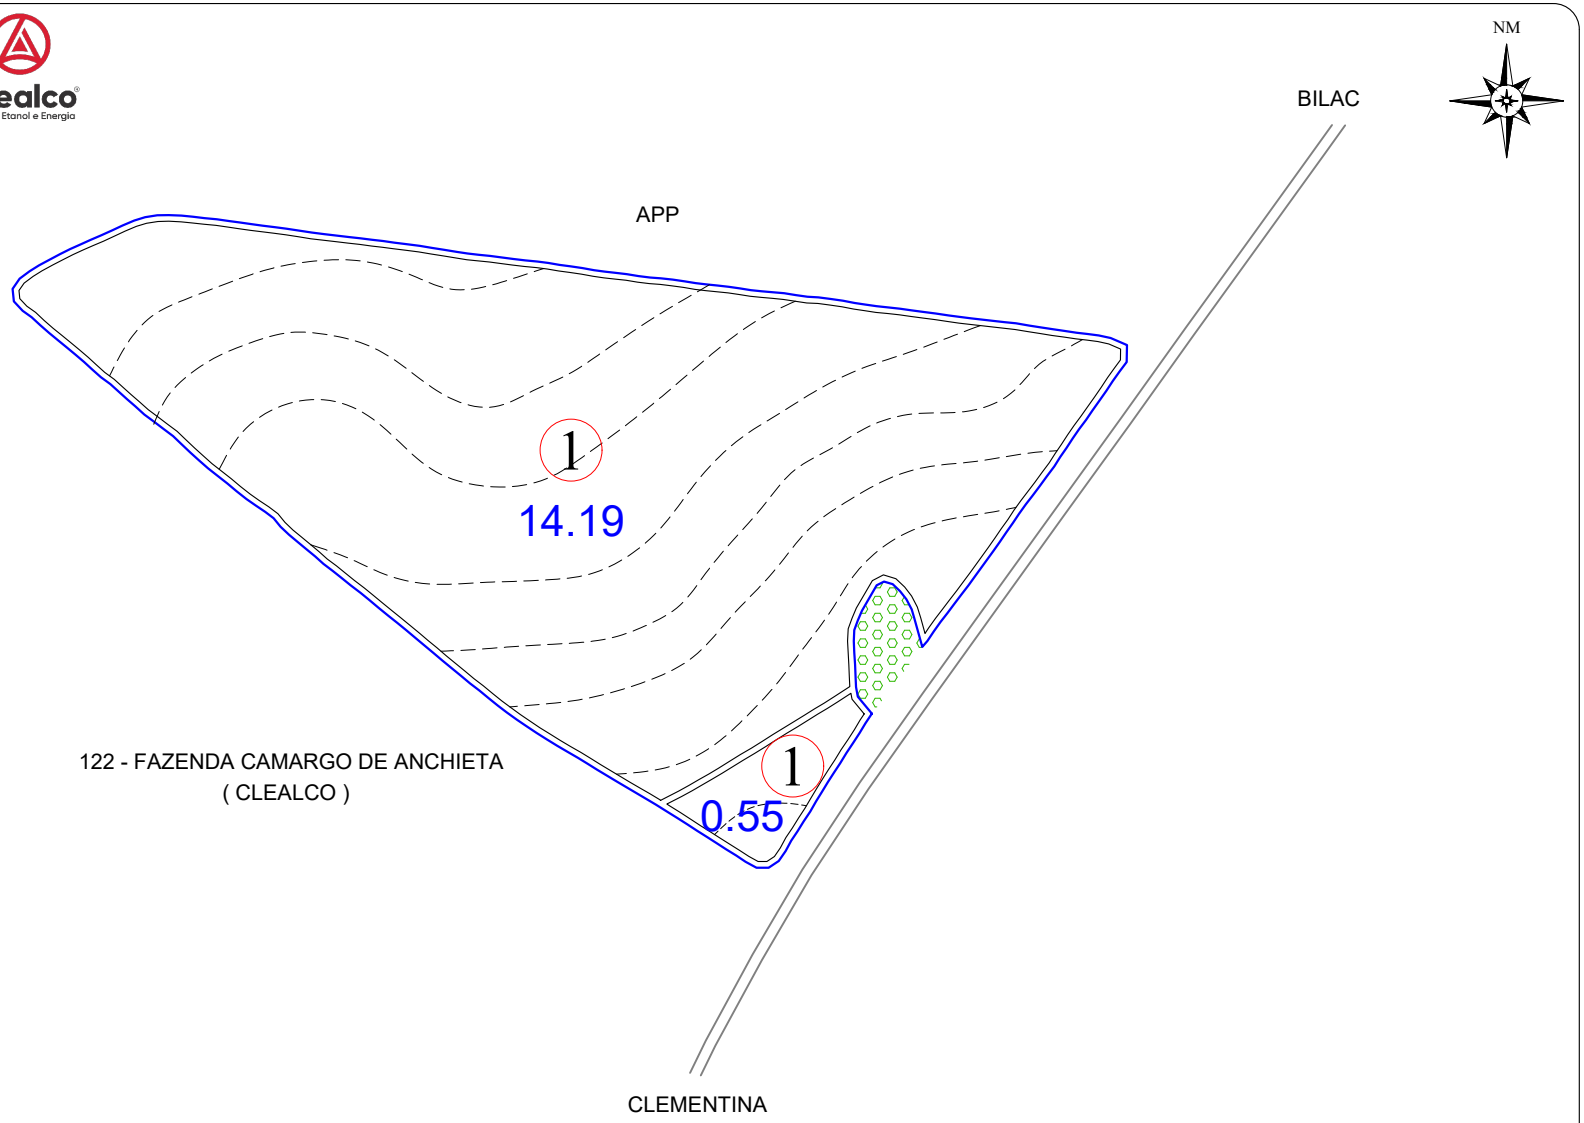

ESCALA: 1: 5.000

CROQUI DE ACESSO

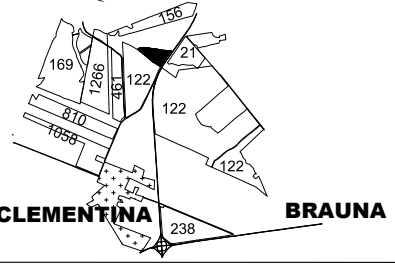

SÍTIO SÃO JOSÉ

PROPRIETÁRIO: CARLOS DONIZETTI GASPAR
ARRENDATÁRIO: ENCARNAÇÃO A. GASPAR
MUNICÍPIO: CLEMENTINA

DISTÂNCIAS (km):
UNID. I - Asfalto: 6.50 Terra.: 0.50
UNID.I I - Asfalto: 62.00 Terra.: 0.50
UNID. III -Asfalto: 32.00 Terra.: 10.50

COORDENADAS: E(X): 558070 N(Y): 7619013
LAT: 21° 31' 50,49420" LONG: 50° 26' 21,30968"

CLEALCO - AÇÚCAR E ALCOOL S/A - DEPARTAMENTO DE TOPOGRAFIA

UNIDADE: I
PARTE: A/A
FUNDO AGRÍCOLA: 301081