| ZONA D.V. | Nº TAL. | DATA PL. | ÁREA (ha) | VAR. |
|---|---|---|---|---|
| 1<br>4.86% | 1 | 08/2022 | 15.99 | RB96 6928 |
| | 2 | | 28.68 | |
| | 3 | | 20.70 | |
| | 4 | | 25.91 | |
| | 5 | | 24.98 | |
| | 6 | | 38.31 | |
| | 7 | | 20.69 | |
| | 8 | | 21.39 | |
| TOTAL PLANTIO | | | 196.65 | -------- |


| ÁREAS | (ha) | (%) |
|---|---|---|
| PLANTIO | 196.65 | 94.16 |
| CARREADORES | 10.48 | 5.02 |
| OUTROS | 0.00 | 0.00 |
| SUB TOTAL AGRICULTÁVEL | 207.13 | 99.18 |
| AP.P. | 0.00 | 0.00 |
| ÁRVORES | 1.45 | 0.69 |
| OUTROS | 0.26 | 0.12 |
| SUB TOTAL NÃO AGRICULT. | 1.71 | 0.82 |
| ÁREA TOTAL | 208.84 | 100.00 |

C. NÍVEL: 17467.49 m/l 4.02 ha 1.92 %

LEGENDA


- FAZENDA
- TALHÃO
- CURVA DE NÍVEL
- CARREADOR
- CONFRONTANTE
- REDE ELÉTRICA
- TRAJETO VAZIO
- TRAJETO CARREGADO

PLANTIO MANUAL - ESPAÇAMENTO: 1.50 X 1.50
TIRO MÉDIO ESTIMADO: 000.00m

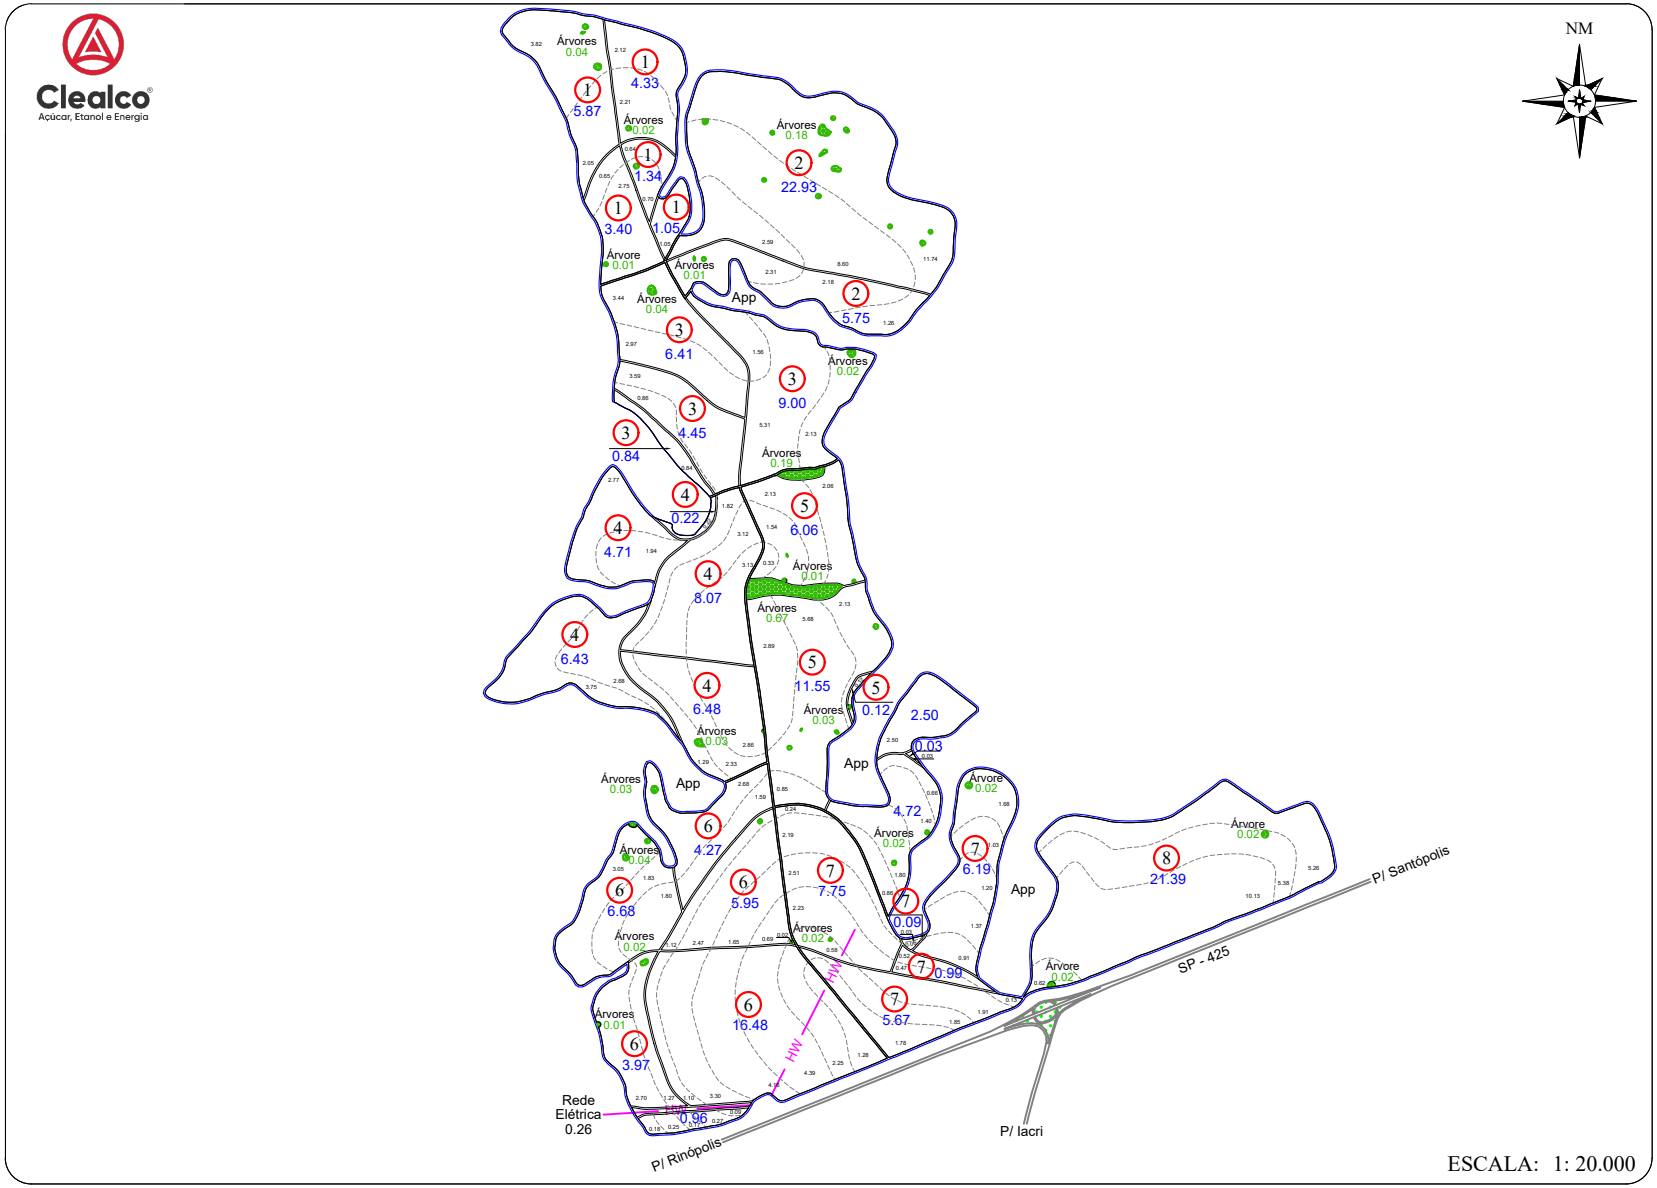


ESCALA: 1: 20.000

CROQUI DE ACESSO

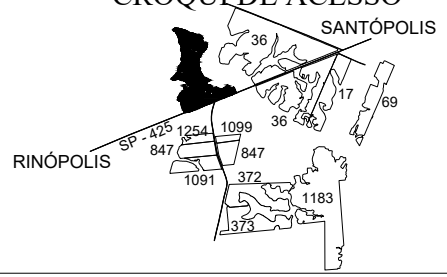


# FAZENDA SANTA ROSA DO AGUAPEI

PROPRIETÁRIO: MARCIO CISNEROS
ARRENDATARIO: CARLOS DONIZETE GASPAR
MUNICÍPIO: IACRI - SP

DISTÂNCIAS (km):
UNID. I - Asfalto: 22.50 Terra.: 0.50
UNID.I I - Asfalto: 55.00 Terra.: 0.50
UNID. III -Asfalto: 0.00 Terra.: 0.00

COORDENADAS: E(X): 540585.17 N(Y): 7603564.93
LAT: -21°40'14.6817" LONG: -50°36'27.7690"

CLEALCO - AÇÚCAR E ALCOOL S/A - DEPARTAMENTO DE TOPOGRAFIA

UNIDADE: I
PARTE: A/A
FUNDO AGRÍCOLA: 307167