| ZONA D.V. | Nº TAL. | DATA PL. | ÁREA (ha) | VAR. |
|---|---|---|---|---|
| 1<br>5.86 % | 1 | 07/2022 | 15.36 | DIVERSAS |
| | 2 | | 16.36 | |
| | 3 | | 3.53 | |
| TOTAL PLANTIO | | | 35.25 | -------- |

| ÁREAS | (ha) | (%) |
|---|---|---|
| PLANTIO | 35.25 | 93.98 |
| CARREADORES | 2.23 | 5.94 |
| OUTROS | 0.00 | 0.00 |
| SUB TOTAL AGRICULTÁVEL | 37.48 | 99.92 |
| AP.P. | 0.00 | 0.00 |
| ÁRVORES | 0.03 | 0.08 |
| OUTROS | 0.00 | 0.00 |
| SUB TOTAL NÃO AGRICULT. | 0.03 | 0.08 |
| ÁREA TOTAL | 37.51 | 100.00 |


C. NÍVEL: 2237.34 m/l 0.51 ha 1.37 %

LEGENDA


- FAZENDA
- TALHÃO
- CURVA DE NÍVEL
- CARREADOR
- CONFRONTANTE
- REDE ELÉTRICA
- TRAJETO VAZIO
- TRAJETO CARREGADO

PLANTIO MANUAL - ESPAÇAMENTO: 0.90 X 1.50
TIRO MÉDIO ESTIMADO: 000.00m

Clealco
Açúcar, Etanol e Energia

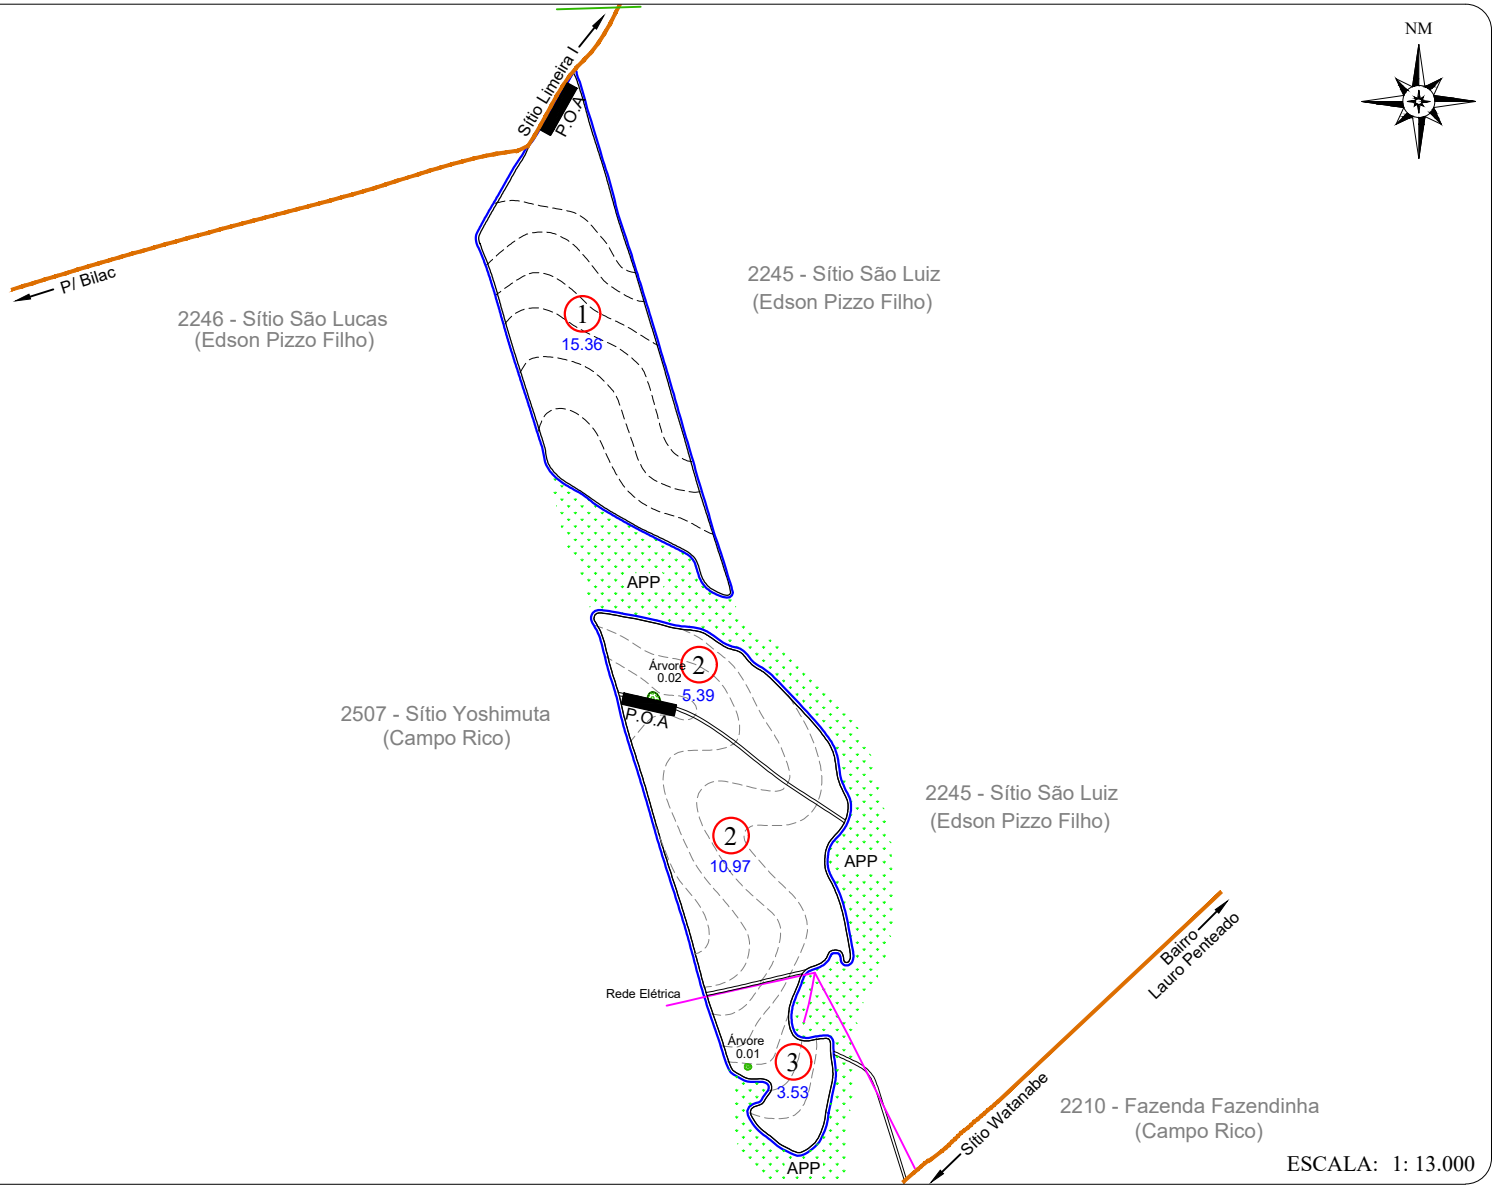


## CROQUI DE ACESSO

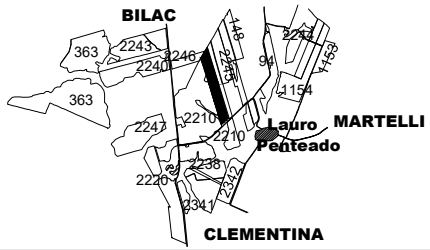


# SÍTIO YOSHIMUTA

PROPRIETÁRIO: TADASHI YOSHIMUTA
ARRENDATÁRIO: EDSON PIZZO FILHO
MUNICÍPIO: BILAC

DISTÂNCIAS (km):

| | | | |
|---|---|---|---|
| UNID. I - Asfalto: | 3.50 | Terra.: | 10.70 |
| UNID.I I - Asfalto: | 60.00 | Terra.: | 10.70 |
| UNID. III -Asfalto: | 50.00 | Terra.: | 10.70 |

COORDENADAS: E(X): 554701 N(Y): 7622251
LAT: 21° 30' 05,54586" LONG: 50° 28' 18,77186"

CLEALCO - AÇÚCAR E ALCOOL S/A - DEPARTAMENTO DE TOPOGRAFIA

UNIDADE: I

PARTE: A/A

FUNDO AGRÍCOLA: 302507