ZONA DV	Nº TAL.	DATA PL.	ÁREA (ha)	VARIEDADE
1 4.20 %	8	06/2022	10.01	RB867515
	9		35.63	
	10		33.71	
	11		12.30	
	12		12.62	
TOTAL PLANTIO			104.27	--------


ÁREAS	(ha)	(%)
PLANTIO	104.27	96.23
CARREADORES	3.92	3.62
OUTROS	0.00	0.00
SUB TOTAL AGRICULTÁVEL	108.19	99.85
AP.P.	0.00	0.00
ÁRVORES	0.16	0.15
OUTROS	0.00	0.00
SUB TOTAL NÃO AGRICULT.	0.16	0.15
ÁREA TOTAL	108.35	100.00

C. NÍVEL: 14843.89 m/l 3.41 ha 3.15 %


LEGENDA

- FAZENDA
- TALHÃO
- CURVA DE NÍVEL
- CARREADOR
- CONFRONTANTE
- REDE ELÉTRICA
- TRAJETO VAZIO
- TRAJETO CARREGADO

PLANTIO MECANIZADO - ESPAÇAMENTO: 0.90 x 1.50
TIRO MÉDIO ESTIMADO: 280.60

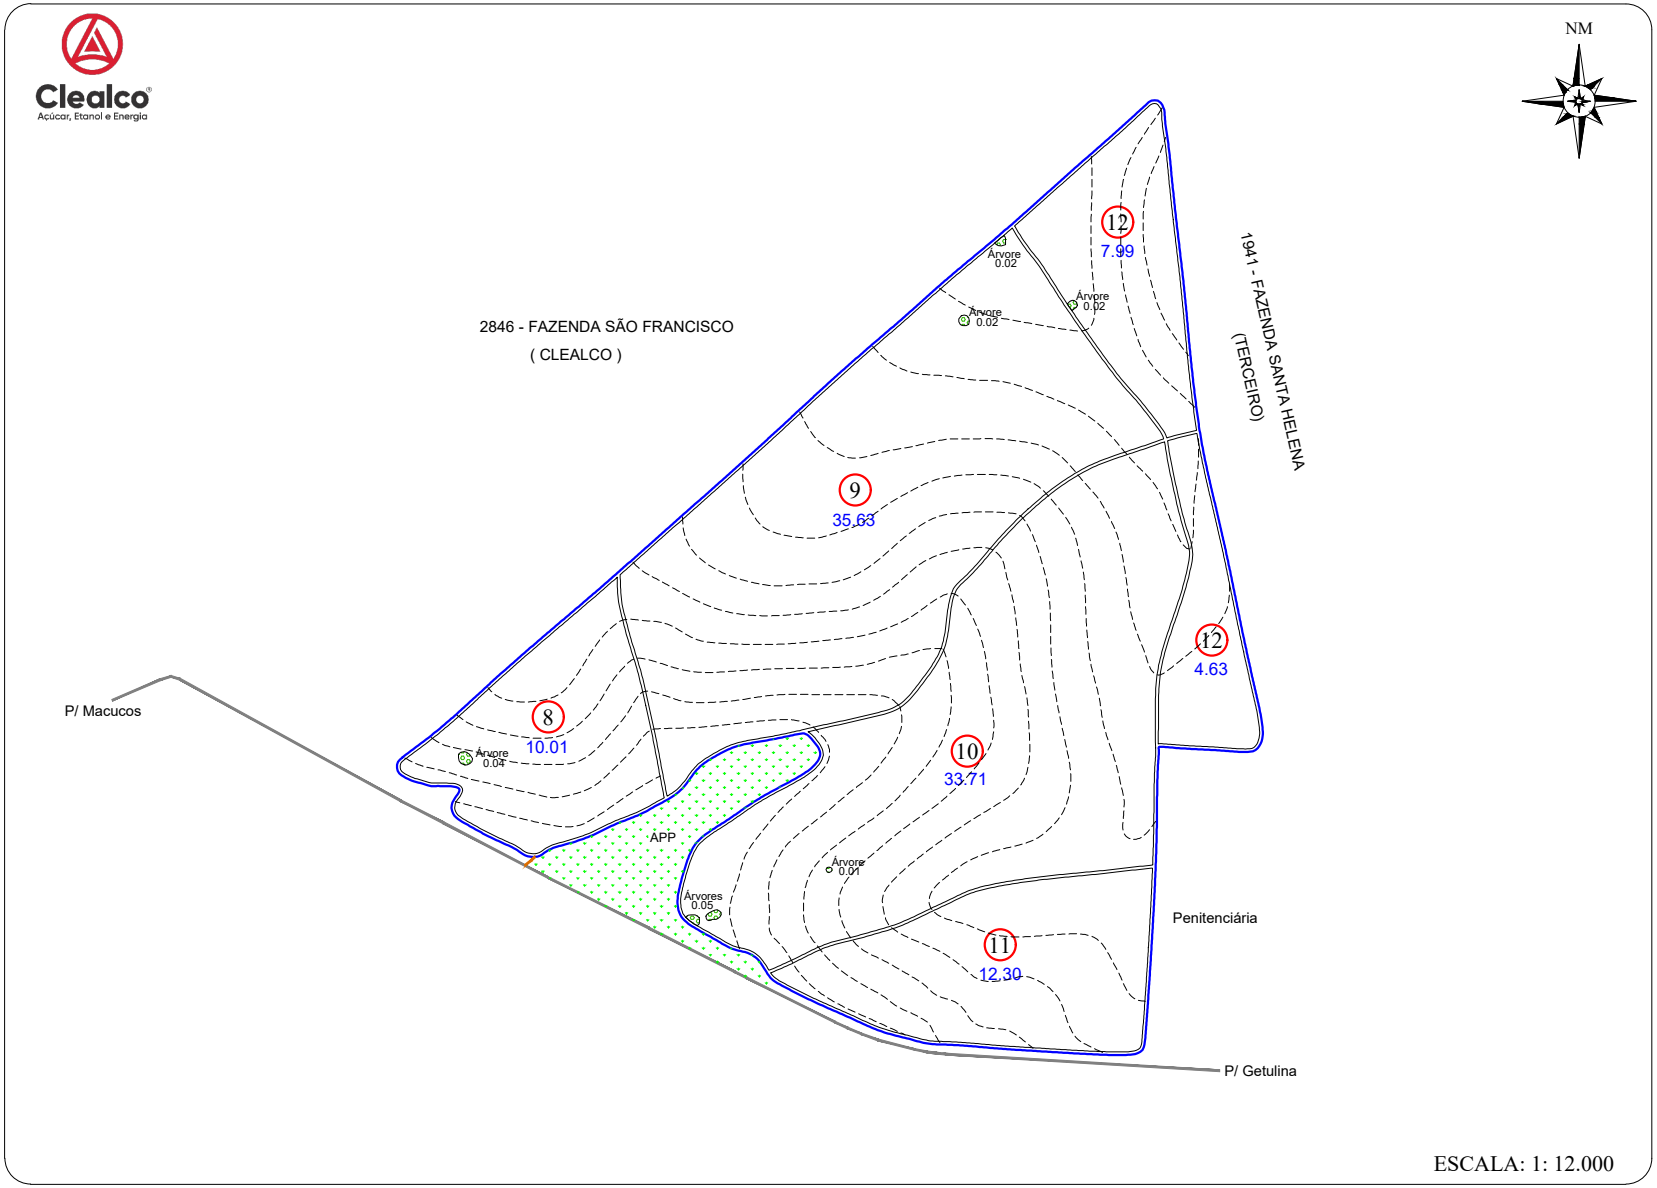

ESCALA: 1: 12.000

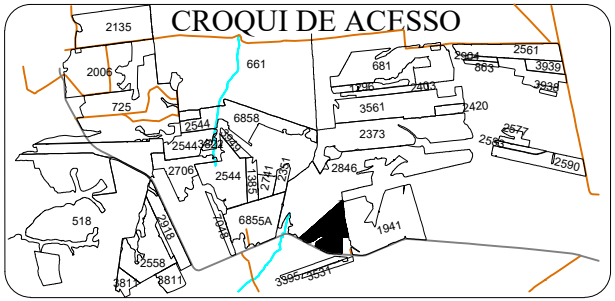

SITIO METODIO

PROPRIETÁRIO: CAMPO RICO AGROPECUARIA LTDA
COMPRADOR: CLEALCO S/A
MUNICÍPIO: GETULINA

DISTÂNCIAS (km):
UNID. I - Asfalto: 82.70 Terra.: 1.10
UNID.I I - Asfalto: 29.20 Terra.: 1.10
UNID. III -Asfalto: 82.30 Terra.: 1.10

COORDENADAS: E(X): 597962.60 N(Y): 7590336.28
LAT: -21°47'16.8384" LONG: -50°3'8.5506"

CLEALCO - AÇÚCAR E ALCOOL S/A - DEPARTAMENTO DE TOPOGRAFIA

UNIDADE: II
PARTE: A/A
FUNDO AGRÍCOLA: 306855

M:\01-Mapa de safra\Mapas Atualizados\Acionista\Edson Pizzo Filho e Leticia Giorjao Pizzo (Campo Rico)\306855 - Sítio Metódio (Álvaro Metódio)\306855 - Sítio Metódio (Álvaro Metódio).dwg

Peterson Santos 15/07/22