ZONA DV	Nº TAL.	DATA PL.	ÁREA (ha)	VAR.
1	1	05/2021	14.65	RB 966928
	2		24.87	
	3		24.87	
	4		21.90	
	5		28.93	
	6		9.05	
TOTAL PLANTIO			124.27	


ÁREAS	(ha)	(%)
PLANTIO	124.27	89.08
CARREADORES	7.21	5.17
SUB TOTAL AGRICULTÁVEL	131.48	--------
ÁRVORES	0.22	0.15
PEDREIRA	0.11	0.08
EROSÃO	7.31	5.24
REDE ELÉTRICA	0.39	0.28
SUB TOTAL NÃO AGRICULT.	8.03	--------
ÁREA TOTAL	139.51	100.00

C. NÍVEL 21434.09 m/l 4.93 ha 3.97 %


LEGENDA

- FAZENDA
- TALHÃO
- CURVA DE NÍVEL
- CARREADOR
- CONFRONTANTE
- REDE ELÉTRICA
- TRAJETO VAZIO
- TRAJETO CARREGADO

PLANTIO MANUAL - ESPAÇAMENTO: 1.50 x 1.50

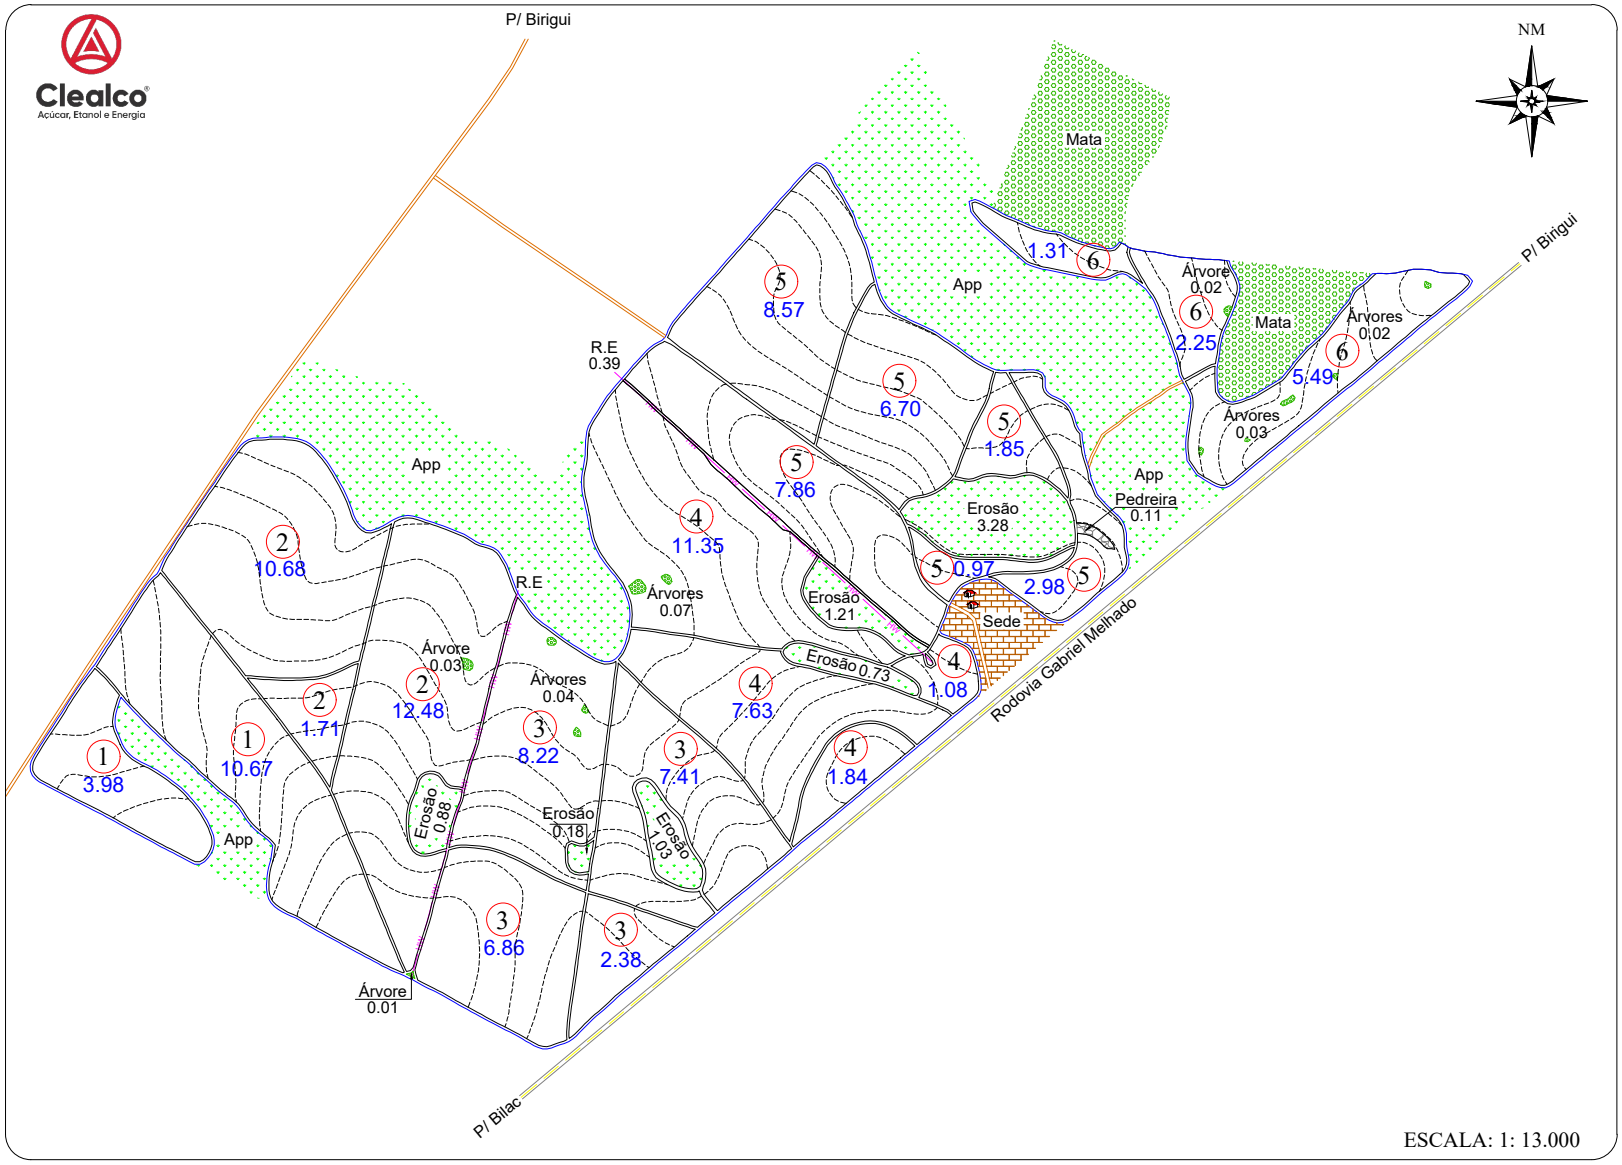

CROQUI DE ACESSO

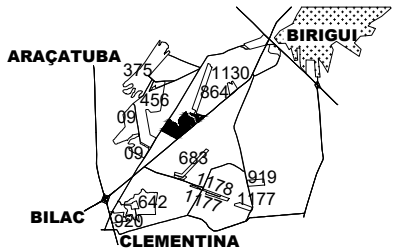

FAZENDA CALIFÓRNIA IV

PROPRIETÁRIO: IBRAHIM DAVID CURY NETO
COMPRADOR: MARILINA PIZZO PADOVESE
MUNICÍPIO: BIRIGUI

DISTÂNCIAS (km):

UNID. I - Asfalto:	28.70	Terra.:	0.60
UNID.I I - Asfalto:	84.00	Terra.:	0.60
UNID. III -Asfalto:	94.00	Terra.:	0.60

COORDENADAS: E(X): 560851.9804 N(Y): 7639500.8909
LAT: 21°20'43,52900" LONG: 50°24'47,27836"

CLEALCO - AÇÚCAR E ALCOOL S/A - DEPARTAMENTO DE TOPOGRAFIA

UNIDADE: I

PARTE: A/A

FUNDO AGRÍCOLA: 307798

Bruno Gamboa 09/04/25

M:\01-Mapa de safra\Mapas Atualizados\Acionista\Marilina Pizzo Padovese\307798 - Fazenda Califórnia IV (Leticia Giorjao Pizzo)\307798 - Fazenda Califórnia IV (Leticia Giorjao Pizzo).dwg