
Clealco
Açúcar, Etanol e Energia

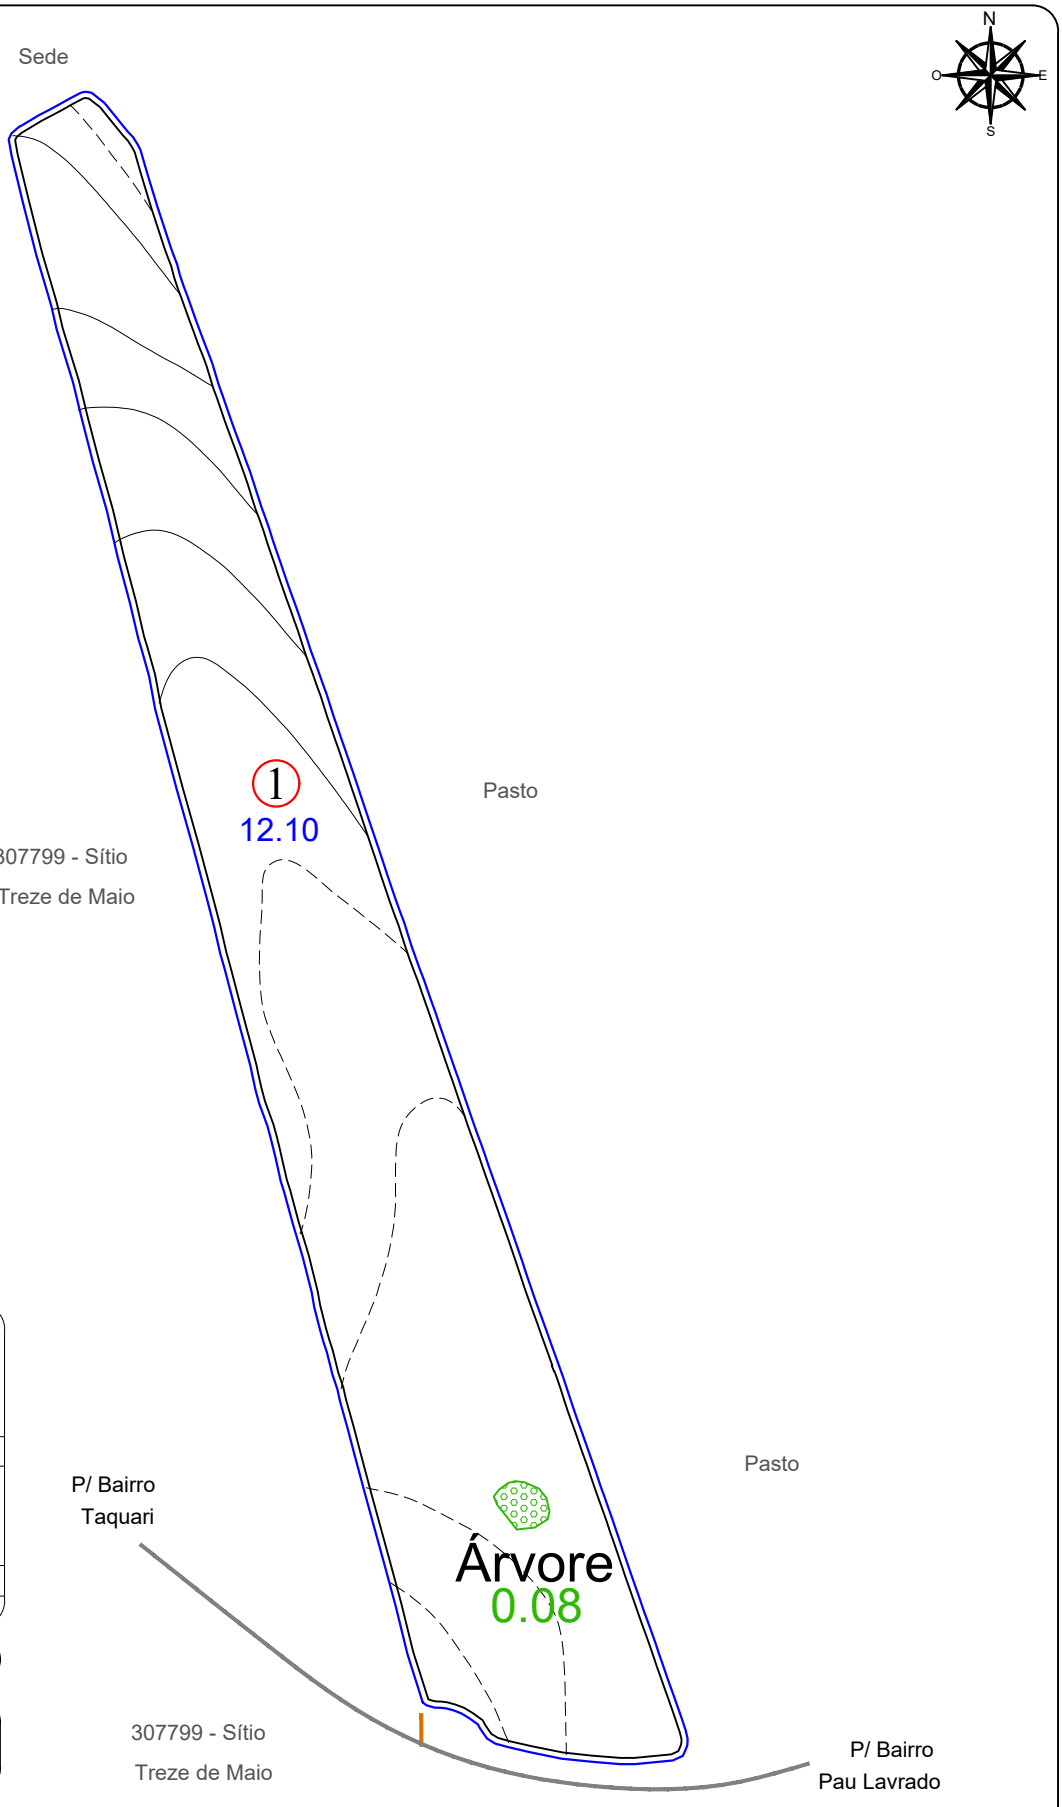

Nº TAL.	DATA PL.	ÁREA (ha)	VARIEDADE
1	03/2026	12.10	RB975201
TOTAL PLANTIO		12.10	

ÁREAS	(ha)	(%)
PLANTIO	12.10	92.04
CARREADORES	0.97	7.35
OUTROS	0.00	0.00
SUB TOTAL AGRICULTÁVEL	13.07	99.39
AP.P.	0.00	0.00
ÁRVORES	0.08	0.61
OUTROS	0.00	0.00
SUB TOTAL NÃO AGRICULT.	0.08	0.61
ÁREA TOTAL	13.15	100.00

C. NÍVEL: 1821.41 m/l 0.42 ha 3.19 %


LEGENDA

- FAZENDA
- TALHÃO
- REDE ELÉTRICA
- TERRAÇO BASE LARGA
- TERRAÇO EMBUTIDO
- (P.O.A) PATIO DE OPERAÇÃO

ESPAÇAMENTO: 1.50 x 1.50
TIRO MÉDIO ESTIMADO: 230.52 m
D.V: 2.00 %

ESCALA: 1: 5.000

CROQUI DE ACESSO

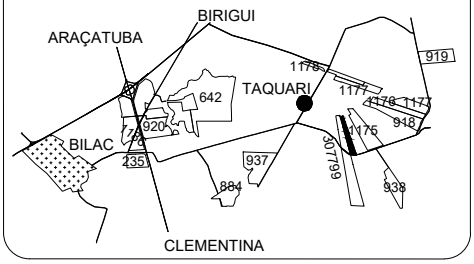

SÍTIO TREZE DE MAIO

PROPRIETÁRIO: LETICIA GIORJAO PIZZO
COMPRADOR: CLEALCO
MUNICÍPIO: BIRIGUI - SP

DISTÂNCIAS (km):
UNID. I - Asfalto: 30.50 Terra.: 0.10
UNID.I I - Asfalto: 85.50 Terra.: 0.10

COORDENADAS: E(X): 562336.00 N(Y): 7634050.11
LAT: -21°23'40.8991" LONG: -50°23'55.0239"

CLEALCO - AÇÚCAR E ALCOOL S/A - DEPARTAMENTO DE GEOTECNOLOGIA

LEVANTAMENTO VIA:
- SATÉLITE
- GPS / VANT
- GOOGLE

UNIDADE: I
PARTE: A/A
FUNDO AGRÍCOLA: 307802

M:\01-Mapa de safra\Mapas Atualizados\Acionista\Edson Pizzo Filho e Leticia Giorjao Pizzo (Campo Rico)\307802 - Sitio Treze de Maio (Leticia Giorjao Pizzo)\307802 - Sitio Treze de Maio (Leticia Giorjao Pizzo).dwg

Benati 10/07/2026