D.V.	Nº TAL.	DATA PL.	ÁREA (ha)	VARIEDADE
6.15%	1	06/2023	9.14	RB 855453
TOTAL PLANTIO			9.14	--------

ÁREAS	(ha)	(%)
PLANTIO	9.14	91.47
CARREADORES	0.63	6.32
OUTROS	0.00	0.00
SUB TOTAL AGRICULTÁVEL	9.77	97.80
AP.P.	0.00	0.00
ÁRVORES	0.07	0.70
OUTROS	0.15	1.50
SUB TOTAL NÃO AGRICULT.	0.22	2.20
ÁREA TOTAL	9.99	100.00

C. NÍVEL: 1256.00 m/l 0.29 ha 2.89 %

LEGENDA

▬ FAZENDA	▬ CONFRONTANTE
▬ TALHÃO	---- REDE ELÉTRICA
▬ CURVA DE NÍVEL	—▷ TRAJETO VAZIO
— CARREADOR	—► TRAJETO CARREGADO

PLANTIO MANUAL - ESPAÇAMENTO: 1.50 X 1.50
TIRO MÉDIO ESTIMADO: 102.77 m

Clealco
Açúcar, Etanol e Energia

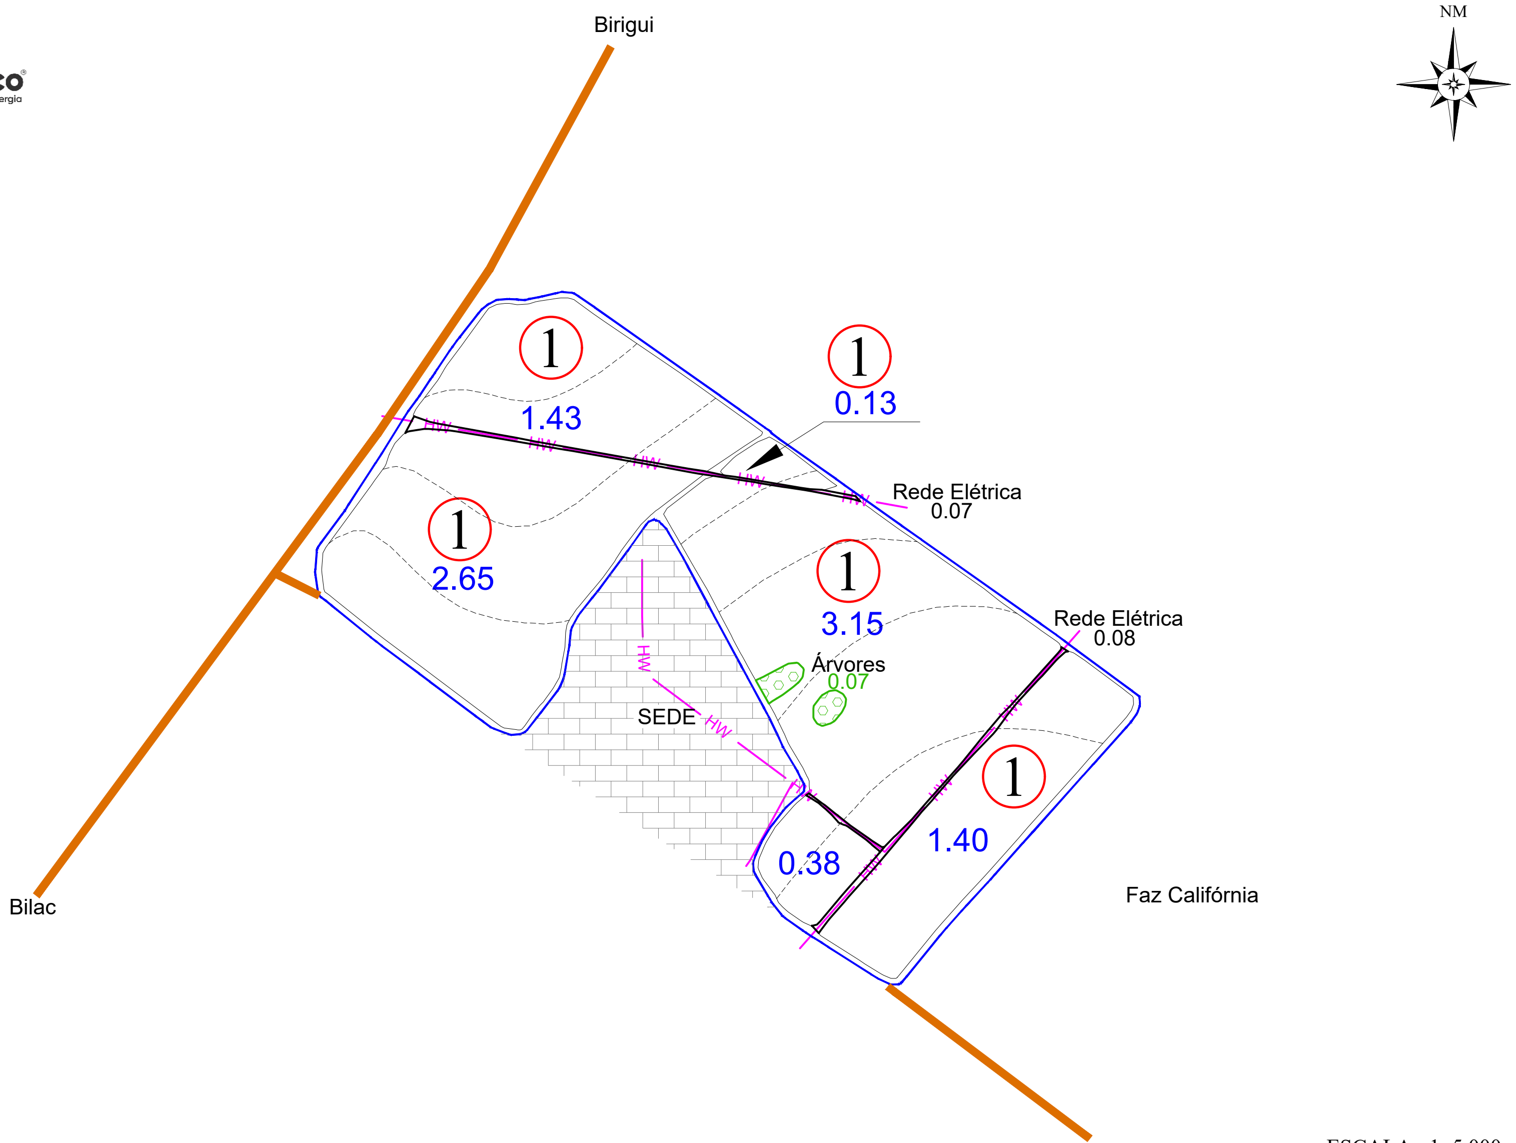
NM
Birigui
Bilac
①
1.43
①
0.13
①
2.65
①
3.15
①
1.40
0.38
Rede Elétrica
0.07
Rede Elétrica
0.08
Árvores
0.07
SEDE
Faz Califórnia
Rod. 461

ESCALA: 1: 5.000

CROQUI DE ACESSO

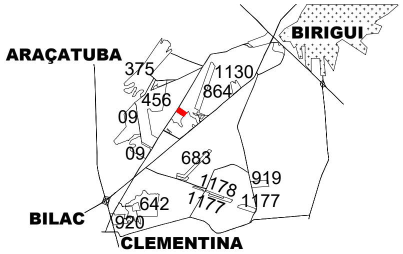
ARAÇATUBA
BIRIGUI
375
1130
456
864
09
09
683
919
1178
1177
1177
642
920
BILAC
CLEMENTINA

SÍTIO TAPENA

PROPRIETÁRIO: LETICIA GIORJÃO PIZZO
COMPRADOR: CLEALCO S/A
MUNICÍPIO: BIRIGUI - SP

DISTÂNCIAS (km):

UNID. I - Asfalto:	28.70	Terra.:	1.00
UNID.I I - Asfalto:	84.00	Terra.:	1.00
UNID. III -Asfalto:	94.00	Terra.:	1.00

COORDENADAS: E(X):	560396.59	N(Y):	7640192.23
LAT:	-21°20'21.3631"	LONG:	-50°25'3.1687"

CLEALCO - AÇÚCAR E ALCOOL S/A - DEPARTAMENTO DE TOPOGRAFIA

UNIDADE:
I

PARTE:
A

FUNDO AGRÍCOLA:
307809

M:\01-Mapa de safra\Mapas Atualizados\Acionista\Marilina Pizzo Padovese\307809 - Sítio Tapena (José Carlos)\307809 - Sítio Tapena (José Carlos).dwg

Bruno Gamboa 28/12/23