
Clealco
Açúcar, Etanol e Energia

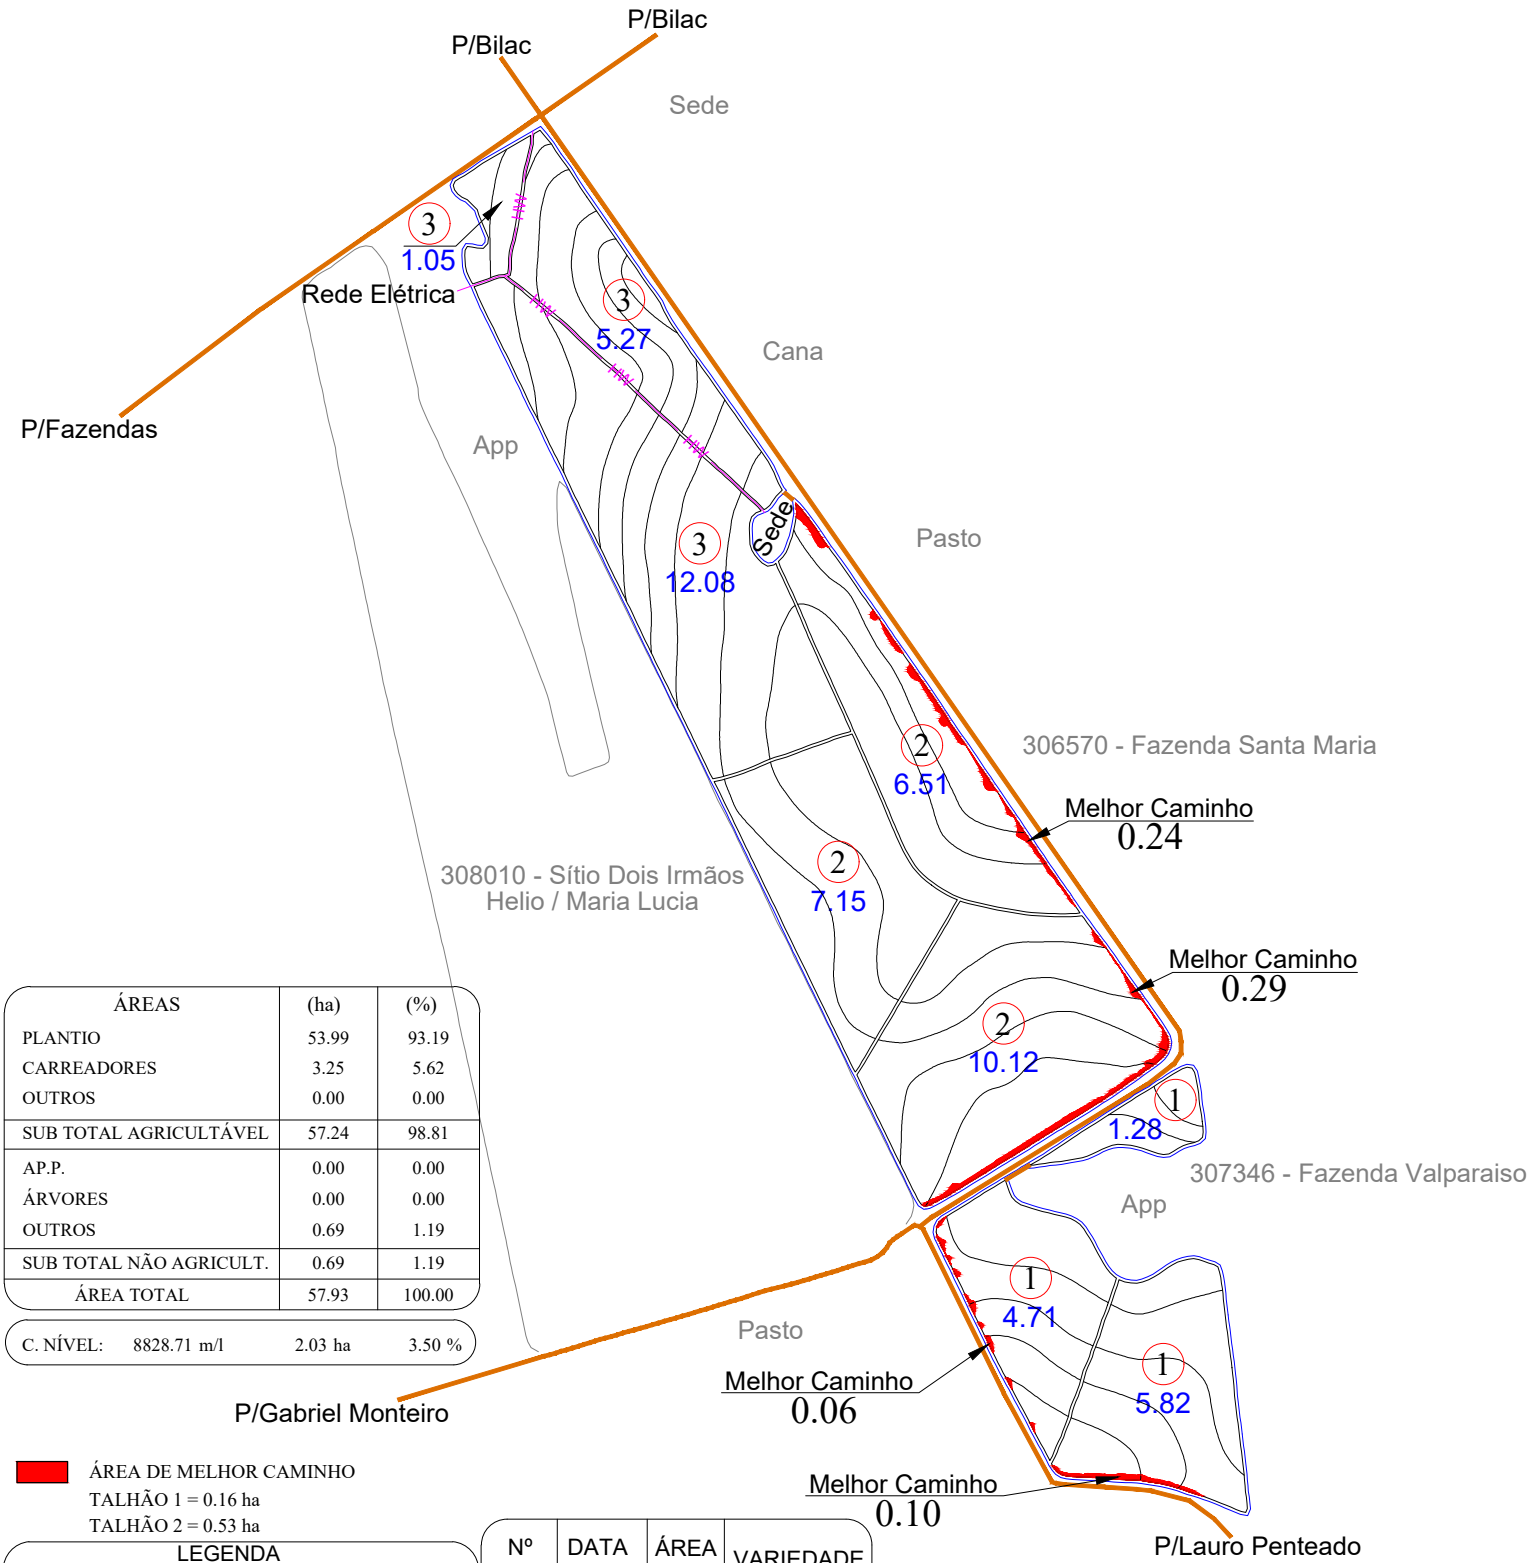

ÁREAS	(ha)	(%)
PLANTIO	53.99	93.19
CARREADORES	3.25	5.62
OUTROS	0.00	0.00
SUB TOTAL AGRICULTÁVEL	57.24	98.81
AP.P.	0.00	0.00
ÁRVORES	0.00	0.00
OUTROS	0.69	1.19
SUB TOTAL NÃO AGRICULT.	0.69	1.19
ÁREA TOTAL	57.93	100.00

C. NÍVEL: 8828.71 m/l 2.03 ha 3.50 %

ÁREA DE MELHOR CAMINHO
TALHÃO 1 = 0.16 ha
TALHÃO 2 = 0.53 ha

LEGENDA
- FAZENDA
- TALHÃO
- REDE ELÉTRICA
- TERRAÇO BASE LARGA
- TERRAÇO EMBUTIDO
- (P.O.A) PATIO DE OPERAÇÃO

ESPAÇAMENTO: 1.50 x 1.50
TIRO MÉDIO ESTIMADO: 000.00 m
D.V: 6.75 %

Nº TAL.	DATA PL.	ÁREA (ha)	VARIEDADE
1	04/2021	11.81	RB 966828
2		23.78	
3		18.40	
TOTAL PLANTIO		53.99	

ESCALA: 1: 10.500

CROQUI DE ACESSO



SÍTIO NOSSA SENHORA DA CONCEIÇÃO

PROPRIETÁRIO: LETICIA GIORJÃO PIZZO
COMPRADOR: CLEALCO
MUNICÍPIO: BILAC - SP

DISTÂNCIAS (km):
UNID. I - Asfalto: 16.00 Terra.: 3.50
UNID.I I - Asfalto: 71.50 Terra.: 3.50

COORDENADAS: E(X): 552452.12 N(Y): 7628142.79
LAT: -21°26'54.1708" LONG: -50°29'37.6253"
CLEALCO - AÇÚCAR E ALCOOL S/A - DEPARTAMENTO DE GEOTECNOLOGIA

LEVANTAMENTO VIA:
- SATÉLITE
- GPS / VANT
- GOOGLE

UNIDADE: I
PARTE: A/A
FUNDO AGRÍCOLA: 308009

M:\01-Mapa de safra\Mapas Atualizados\Acionista\Marilina Pizzo Padovesi\308009 - Sítio Nossa Senhora da Conceição (Leticia Giorjao Pizzo)\308009 - Sítio Nossa Senhora da Conceição (Leticia Giorjao Pizzo).dwg

Bruno Gamboa 24/09/25