ZONA DV	Nº TAL.	DATA PL.	ÁREA (ha)	VAR.
1	1	06/2021	15.05	RB 985476
	2		20.43	
	3		28.79	
	4		27.19	
TOTAL PLANTIO			91.46	

ÁREAS	(ha)	(%)
PLANTIO	91.46	95.12
CARREADORES	4.68	4.87
OUTROS		
SUB TOTAL AGRICULTÁVEL	96.14	-
VÁRZEA	-	-
ÁRVORES	0.01	0.01
OUTROS	-	-
SUB TOTAL NÃO AGRICULT.	0.01	--------
ÁREA TOTAL	96.15	100.00


C. NÍVEL: 8572.76 m/l 1.97 ha 2.16 %

LEGENDA

- FAZENDA
- TALHÃO
- CURVA DE NÍVEL
- CARREADOR
- CONFRONTANTE
- REDE ELÉTRICA
- TRAJETO VAZIO
- TRAJETO CARREGADO


PLANTIO MANUAL - ESPAÇAMENTO: 1.50 x 1.50

Clealco
Açúcar, Etanol e Energia

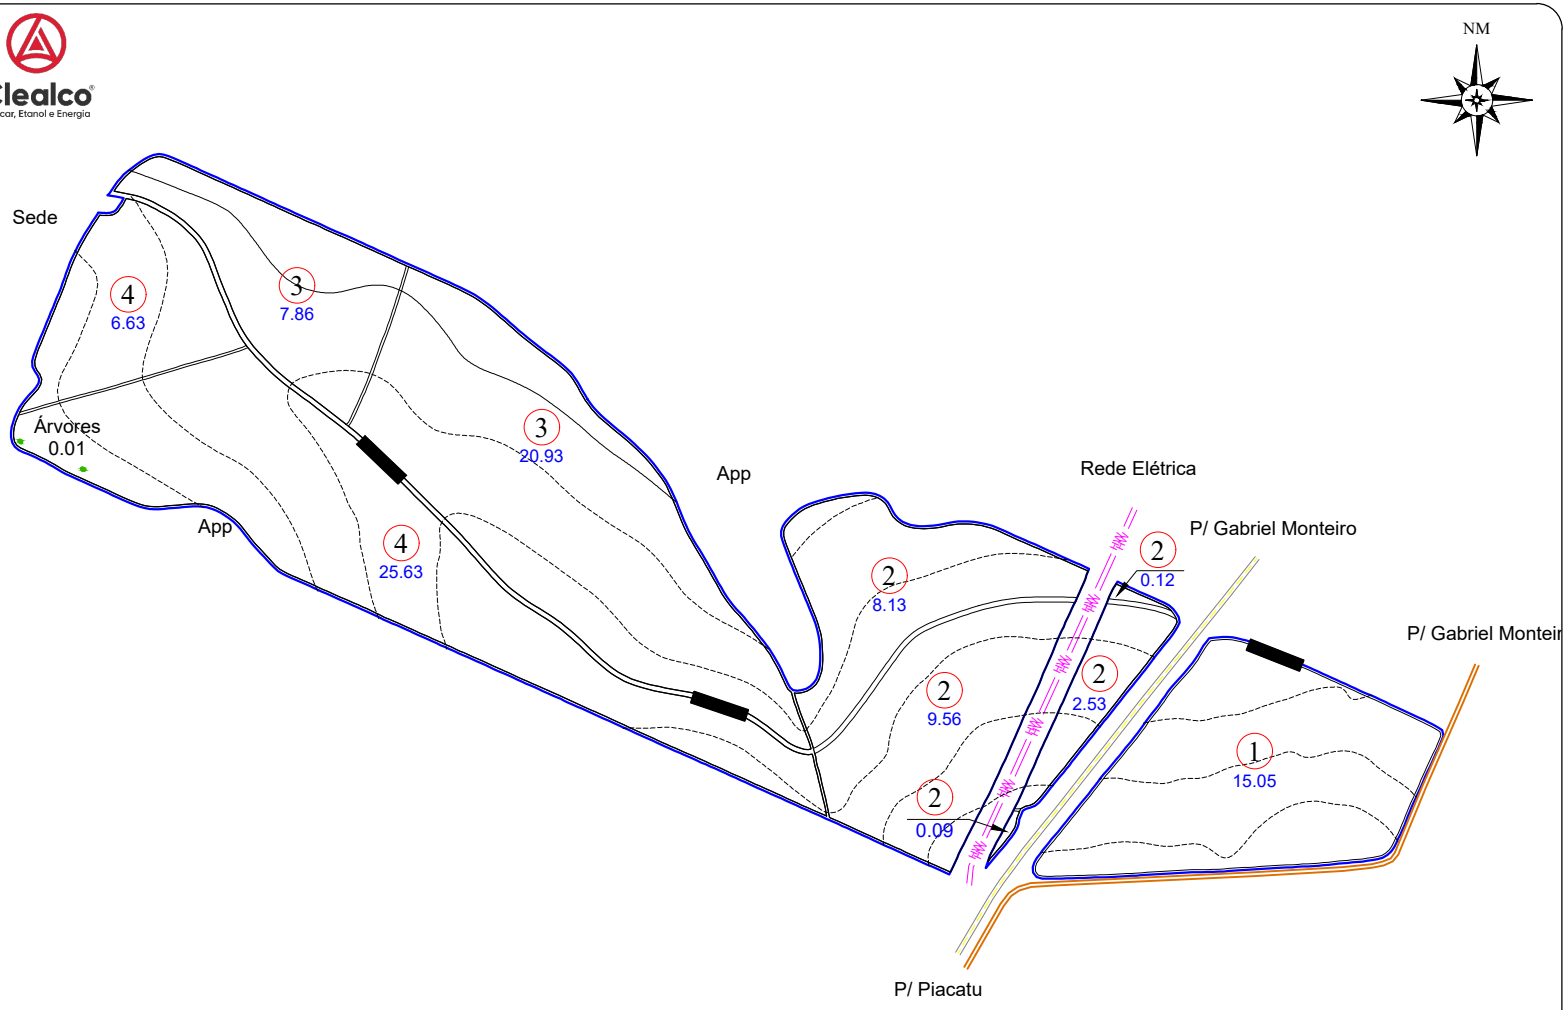

ESCALA: 1: 12.000

CROQUI DE ACESSO

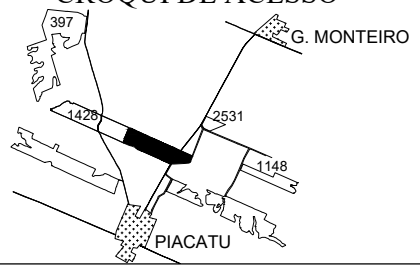

FAZENDA SÃO JOSÉ

PROPRIETÁRIO: EDMUR F. DE JESUS
ARRENDATÁRIO: EMI AGROPECUARIA LTDA
MUNICÍPIO: PIACATU

DISTÂNCIAS (km):
UNID. I - Asfalto: 28.50 Terra.: 7.00
UNID.I I - Asfalto: 63.00 Terra.: 7.00
UNID. III -Asfalto: 73.00 Terra.: 7.00

COORDENADAS: E(X): 542336.8677 N(Y): 7615223.9528
LAT: 21º 33' 55,05557" LONG: 50º 35' 27,88960"

CLEALCO - AÇÚCAR E ALCOOL S/A - DEPARTAMENTO DE TOPOGRAFIA

UNIDADE: I
PARTE: A/A
FUNDO AGRÍCOLA: 300434

M:\01-Mapa de safra\Mapas Atualizados\Acionista\Kenkiti Kimura\300434 - Fazenda São José (Edmur Fernandes de Jesus)\300434 - Fazenda São José (Edmur Fernandes de Jesus).dwg

Fernanda Bezerra 20/07/21