ZONA DV	Nº TAL.	DATA PL.	ÁREA (ha)	VAR.
1 4.59 %	1	06/2021	43.93	RB 975201
	2		5.33	RB 985476
TOTAL PLANTIO			49.26	--------


ÁREAS	(ha)	(%)
PLANTIO	49.26	91.90
CARREADORES	4.32	8.06
OUTROS	0.00	0.00
SUB TOTAL AGRICULTÁVEL	53.58	99.96
VÁRZEA	0.00	0.00
ÁRVORES	0.02	0.04
OUTROS	0.00	0.00
SUB TOTAL NÃO AGRICULT.	0.02	0.04
ÁREA TOTAL	53.60	100.00

C. NÍVEL: 0.00 m/l 0.00 ha 0.00 %


LEGENDA

- FAZENDA
- TALHÃO
- CURVA DE NÍVEL
- CARREADOR
- CONFRONTANTE
- REDE ELÉTRICA
- TRAJETO VAZIO
- TRAJETO CARREGADO

PLANTIO MANUAL - ESPAÇAMENTO: 1.50 x 1.50

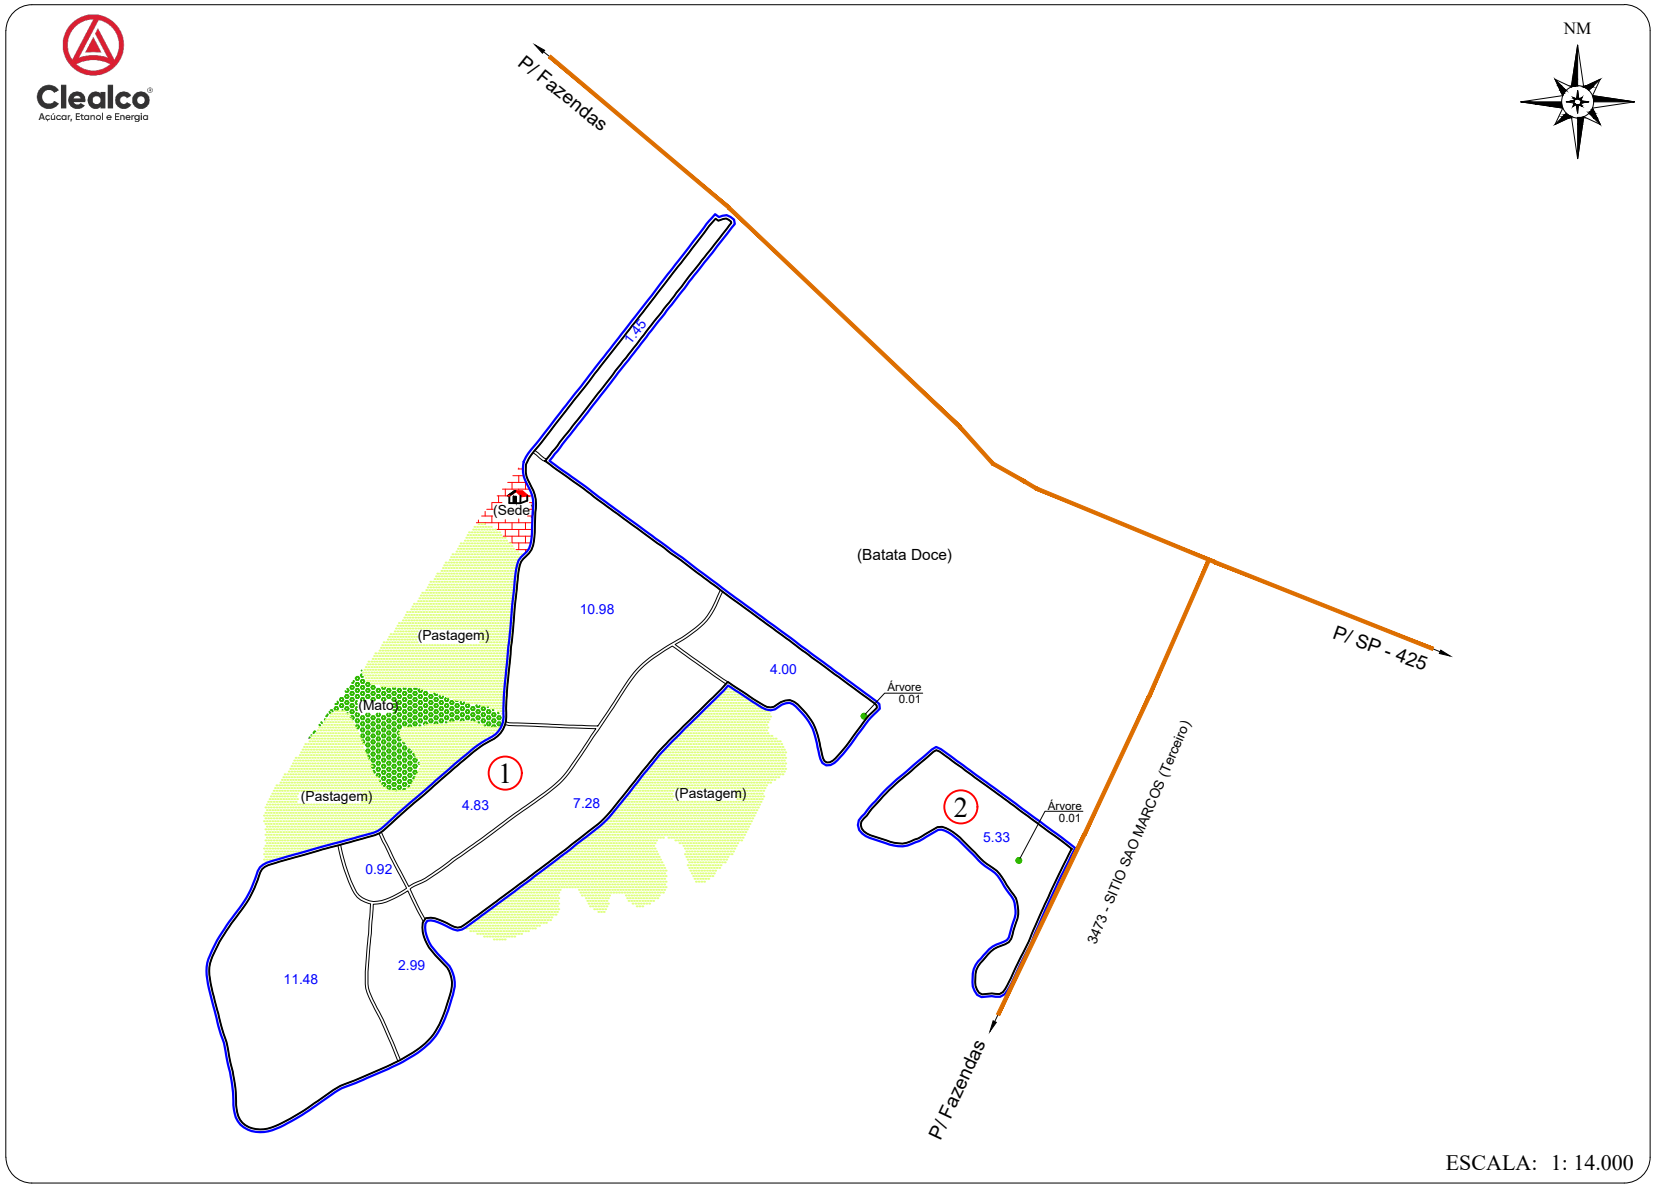

CROQUI DE ACESSO

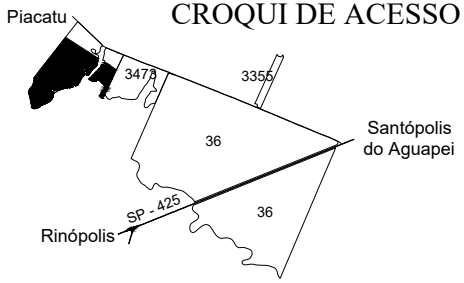

FAZENDA NOSSA SENHORA APARECIDA

PROPRIETÁRIO: JOSÉ SANTINO MAZIERO
ARRENDATÁRIO: IVETE KIMURA TOMO
MUNICÍPIO: PIACATU

DISTÂNCIAS (km):
UNID. I - Asfalto: 18.00 Terra.: 5.50
UNID.I I - Asfalto: 50.00 Terra.: 5.50
UNID. III -Asfalto: 61.00 Terra.: 5.50

COORDENADAS: E(X): 540240,8924 N(Y): 7605792,5024
LAT: 21° 39' 02,25804" LONG: 50° 36' 39,94270"

CLEALCO - AÇÚCAR E ALCOOL S/A - DEPARTAMENTO DE TOPOGRAFIA

UNIDADE: I

PARTE: A/A

FUNDO AGRÍCOLA: 302538

M:\01-Mapa de safra\Mapas Atualizados\Acionista\Kenkiti Kimura\302538 - Fazenda Nossa Senhora Aparecida (Ivete Matiko Kimura Tomo)\302538 - Fazenda Nossa Senhora Aparecida (Ivete Matiko Kimura Tomo).dwg

Pedro Becker 20/07/21