
Clealco
Açúcar, Etanol e Energia

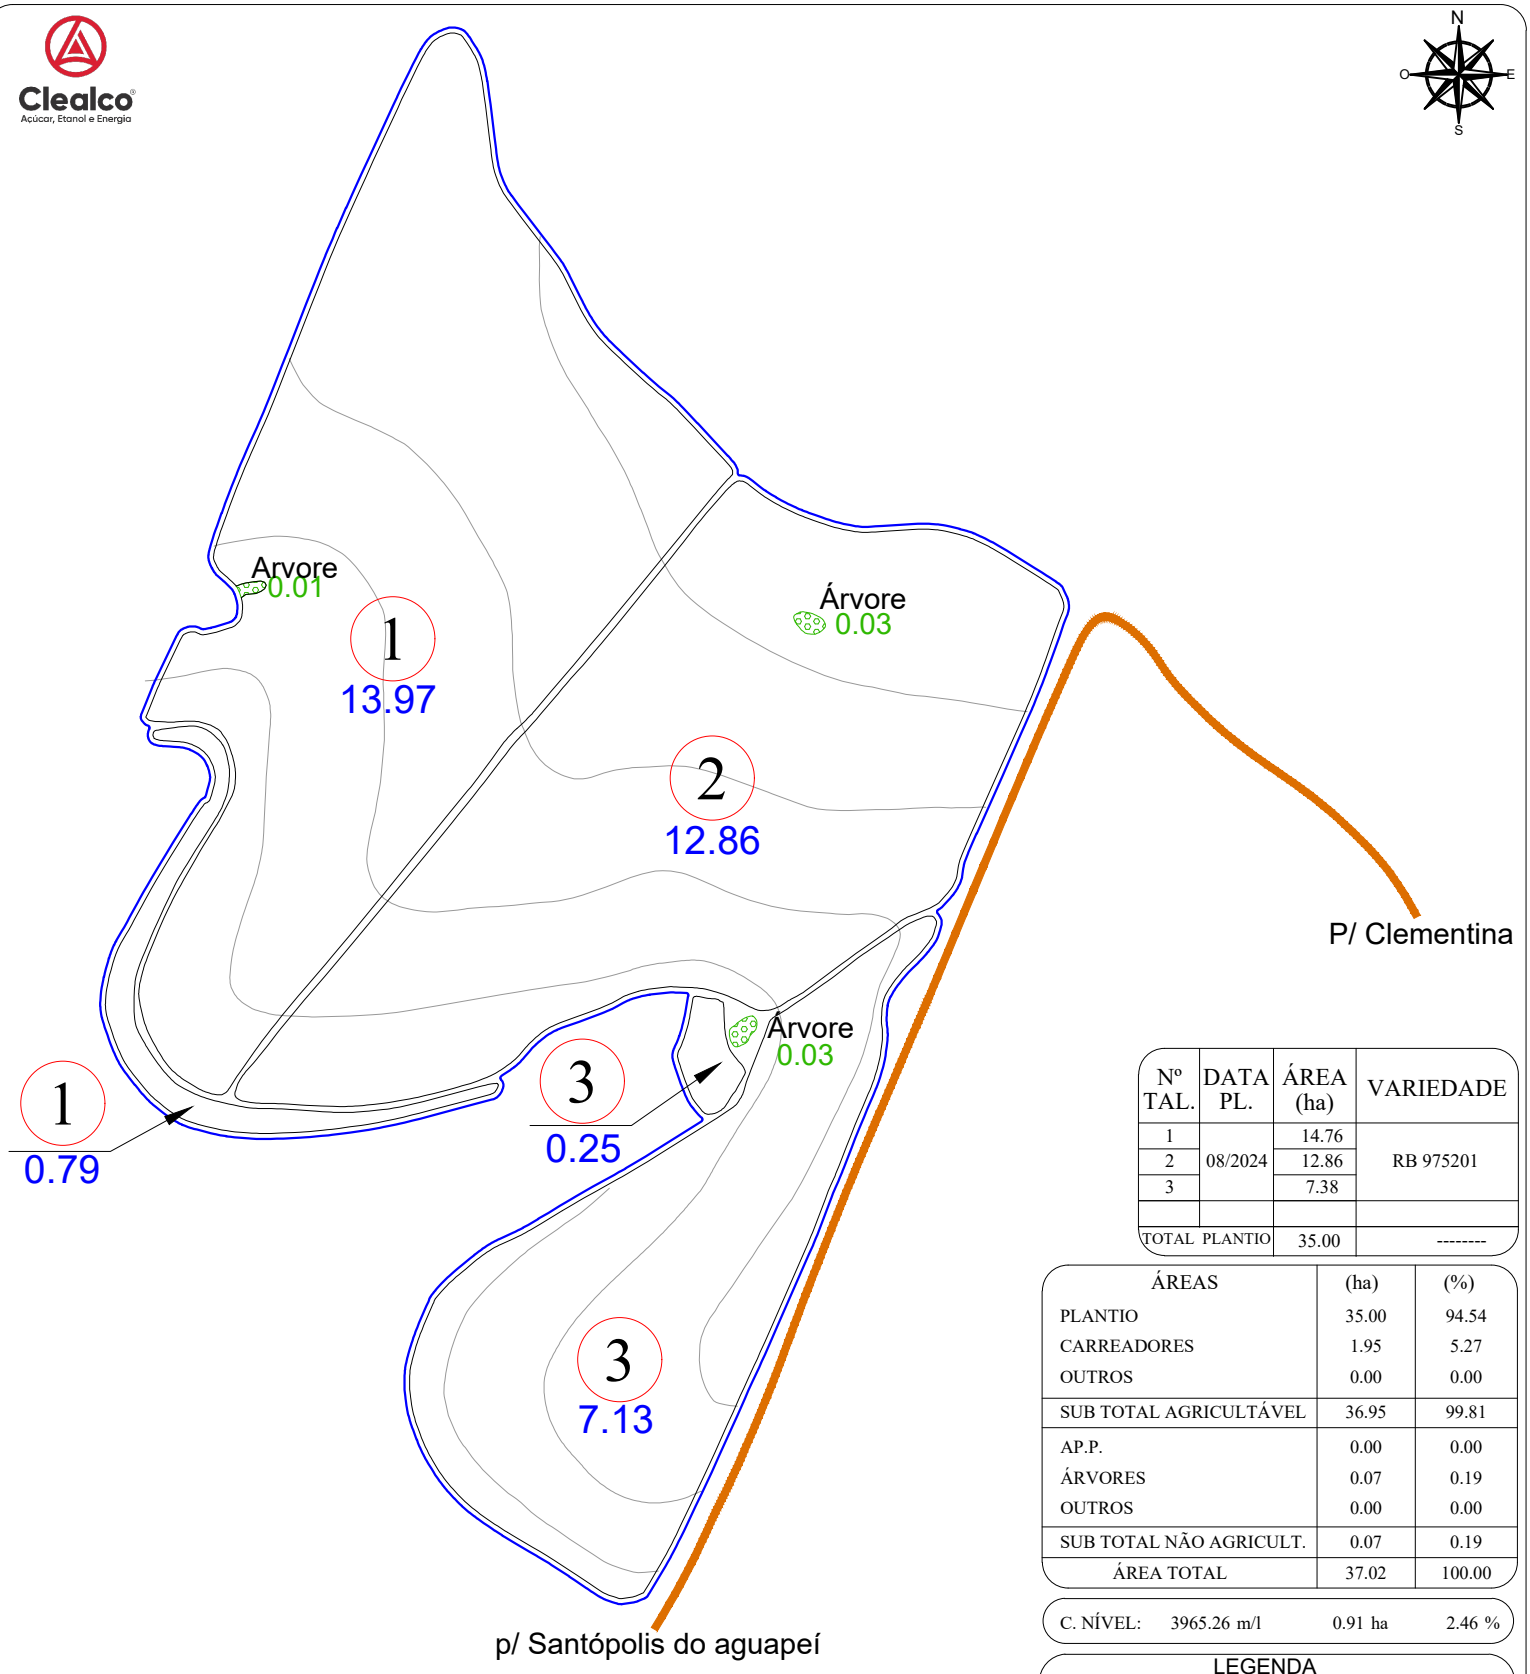

Nº TAL.	DATA PL.	ÁREA (ha)	VARIEDADE
1	08/2024	14.76	RB 975201
2		12.86	
3		7.38	
TOTAL PLANTIO		35.00	--------

ÁREAS	(ha)	(%)
PLANTIO	35.00	94.54
CARREADORES	1.95	5.27
OUTROS	0.00	0.00
SUB TOTAL AGRICULTÁVEL	36.95	99.81
AP.P.	0.00	0.00
ÁRVORES	0.07	0.19
OUTROS	0.00	0.00
SUB TOTAL NÃO AGRICULT.	0.07	0.19
ÁREA TOTAL	37.02	100.00

C. NÍVEL: 3965.26 m/l 0.91 ha 2.46 %


LEGENDA

- FAZENDA
- TALHÃO
- REDE ELÉTRICA
- TERRAÇO BASE LARGA
- TERRAÇO EMBUTIDO
- (P.O.A) PATIO DE OPERAÇÃO

ESPAÇAMENTO: 1.50 x 1.50
TIRO MÉDIO ESTIMADO: 292.86 m
D.V: 5.34 %

ESCALA: 1: 5.500

CROQUI DE ACESSO

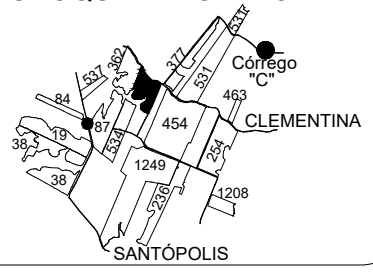

SÍTIO SÃO JORGE

PROPRIETÁRIO: MARCIO HIDEZAKU KIMURA
COMPRADOR: CLEALCO
MUNICÍPIO: CLEMENTINA - SP

DISTÂNCIAS (km):
UNID. I - Asfalto: 5.70 Terra.: 6.75
UNID.I I - Asfalto: 53.40 Terra.: 6.75

COORDENADAS: E(X): 549736.74 N(Y): 7613321.00
LAT: -21°34'56.5305" LONG: -50°31'10.3812"

CLEALCO - AÇÚCAR E ALCOOL S/A - DEPARTAMENTO DE GEOTECNOLOGIA

LEVANTAMENTO VIA:
- SATÉLITE
- GPS / VANT
- GOOGLE

UNIDADE: I
PARTE: A/A
FUNDO AGRÍCOLA: 302621

M:\01-Mapa de safra\Mapas Atualizados\Acionista\Kenkiti Kimura\302621 - Sitio Sao Jorge (Marcio Hidekazu Kimura)\302621 - Sitio Sao Jorge (Marcio Hidekazu Kimura).dwg

Bruno Gamboa 23/07/25