ZONA DV	CLA	Nº TAL.	DATA PL.	ÁREA (ha)	VAR.
1		1	04/2019	29.69	RB 975242
4.37 %	SR	2		29.43	
TOTAL PLANTIO				59.12	--------

ÁREAS	(ha)	(%)
PLANTIO	59.12	96.01
CARREADORES	2.46	3.99
OUTROS	0.00	0.00
SUB TOTAL AGRICULTÁVEL	61.58	---------
ÁREA DE REDE ELÉTRICA	0.66	1.06
MATA	0.00	0.00
OUTROS	0.00	0.00
SUB TOTAL NÃO AGRICULT.	0.66	1.06
ÁREA TOTAL	62.24	---------


C. NÍVEL: 6726.77 m/l 1.55 ha 2.62 %

LEGENDA

- FAZENDA
- TALHÃO
- CURVA DE NÍVEL
- CARREADOR
- CONFRONTANTE
- REDE ELÉTRICA
- TRAJETO VAZIO
- TRAJETO CARREGADO

TIPO DE PLANTIO: CONVENCIONAL: 0.00 ha
ESPAÇAMENTO: 0.90 x 1.50 MECANIZADO: 0.00 ha


Clealco
Açúcar, Etanol e Energia

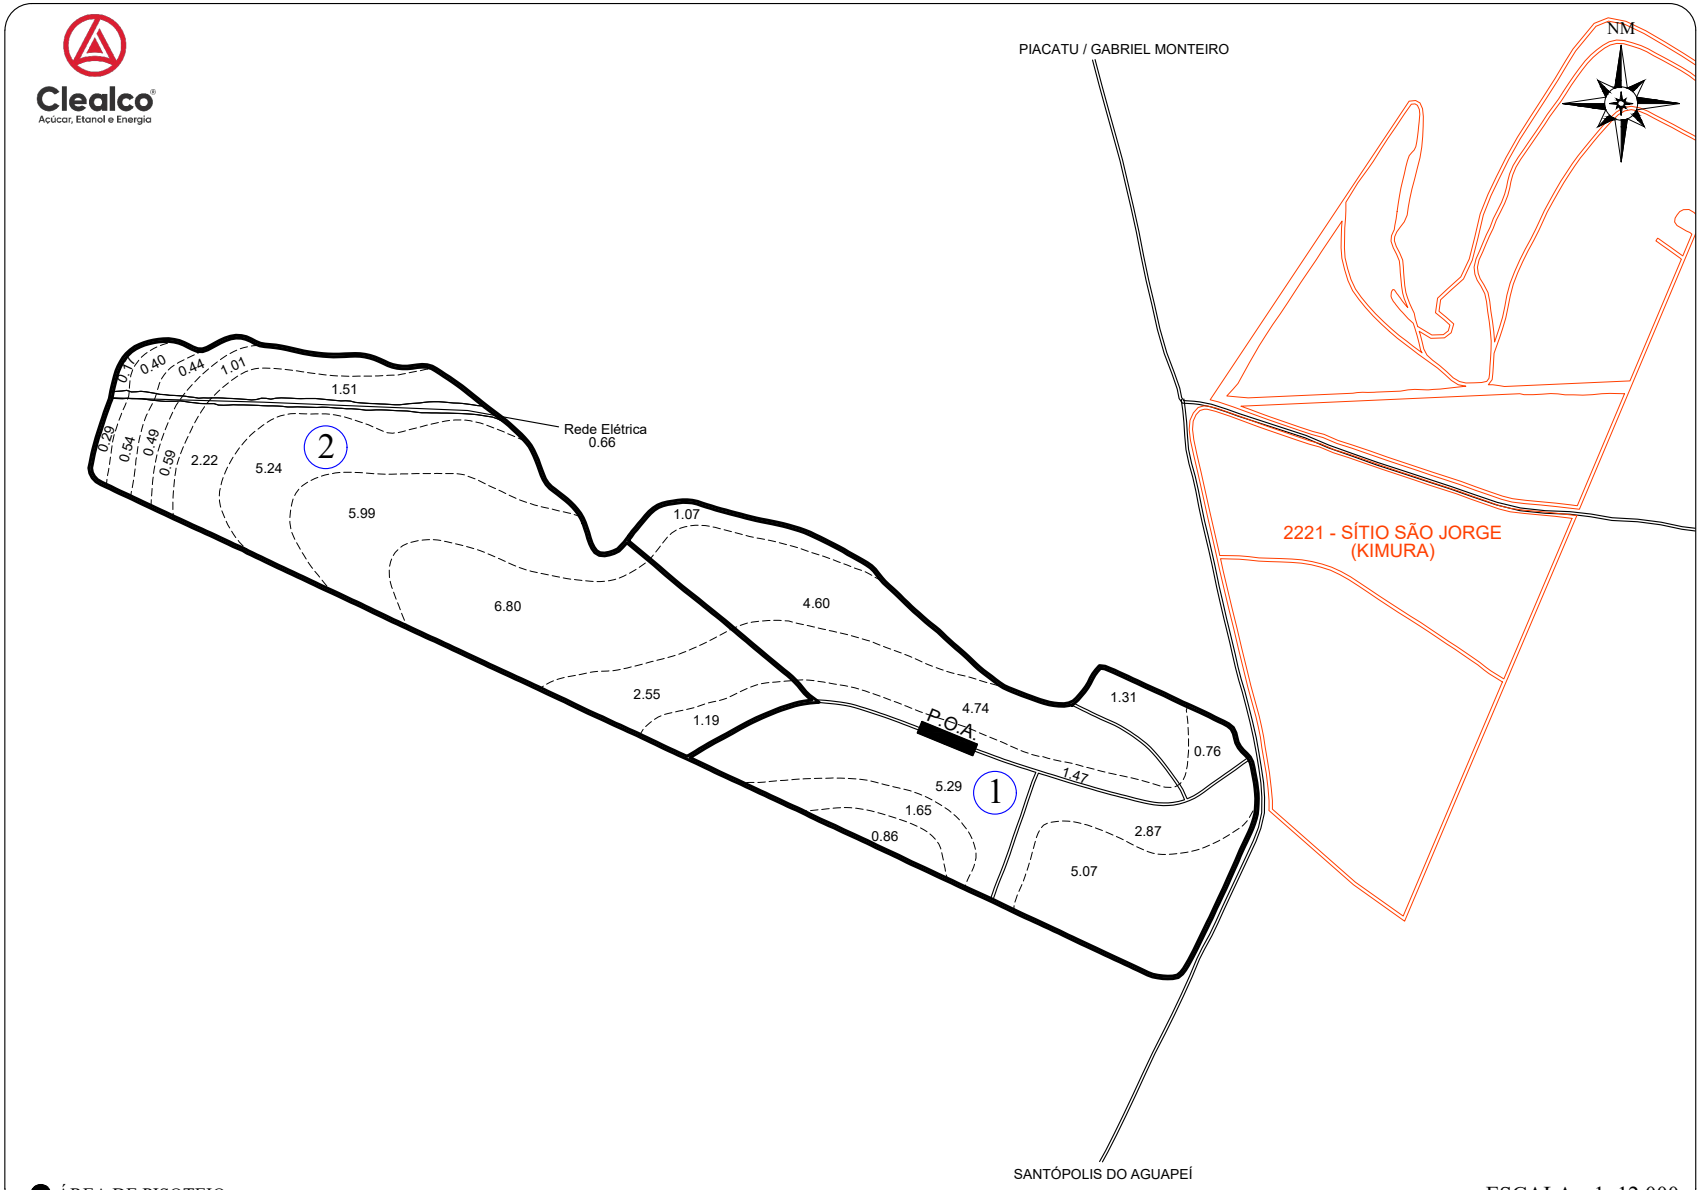

● ÁREA DE PISOTEIO

ESCALA: 1: 12.000

CROQUI DE ACESSO

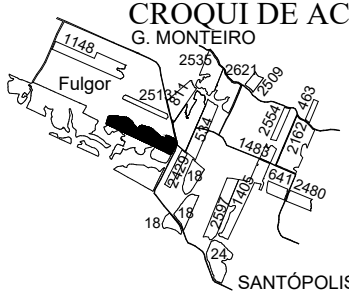

SÍTIO PONGAL

PROPRIETÁRIO: IVETE M. KIMURA TOMO
ARRENDATÁRIO: IVETE M. KIMURA TOMO
MUNICÍPIO: CLEMENTINA

DISTÂNCIAS (km):
UNID. I - Asfalto: 6.50 Terra.: 8.50
UNID.I I - Asfalto: 53.00 Terra.: 8.50
UNID. III -Asfalto: 52.00 Terra.: 8.50

COORDENADAS: E(X): 548813.13 N(Y): 7612616.07
LAT: 21º 35' 19,28183" LONG: 50º 31' 42,43213"

CLEALCO - AÇÚCAR E ALCOOL S/A - DEPARTAMENTO DE TOPOGRAFIA

UNIDADE: I
PARTE: A/A
FUNDO AGRÍCOLA: 302952