| ZONA D.V. | Nº TAL. | DATA PL. | ÁREA (ha) | VAR. |
|---|---|---|---|---|
| 1 6.58% | 1 | 06/2022 | 21.08 | RB975242 |
| | 2 | | 26.67 | |
| | 3 | | 38.29 | |
| | 4 | | 33.88 | |
| | 5 | | 22.99 | |
| | 6 | | 24.41 | |
| | 7 | | 1.63 | |
| | 8 | | 10.91 | |
| | 9 | | 32.95 | |
| | 10 | | 23.68 | |
| | 11 | | 22.94 | |
| | 12 | | 10.45 | |
| TOTAL PLANTIO | | | 269.88 | -------- |

| ÁREAS | (ha) | (%) |
|---|---|---|
| PLANTIO | 269.88 | 95.73 |
| CARREADORES | 11.00 | 3.90 |
| OUTROS | 0.00 | 0.00 |
| SUB TOTAL AGRICULTÁVEL | 280.88 | 99.63 |
| AP.P. | 0.00 | 0.00 |
| ÁRVORES | 0.70 | 0.25 |
| OUTROS | 0.34 | 0.12 |
| SUB TOTAL NÃO AGRICULT. | 1.04 | 0.37 |
| ÁREA TOTAL | 281.92 | 100.00 |


C. NÍVEL: 34949.49 m/l 8.04 ha 2.85 %

LEGENDA

- FAZENDA
- TALHÃO
- CURVA DE NÍVEL
- CARREADOR
- CONFRONTANTE
- REDE ELÉTRICA
- TRAJETO VAZIO
- TRAJETO CARREGADO


PLANTIO MANUAL - ESPAÇAMENTO: 1.50 X 1.50
TIRO MÉDIO ESTIMADO: 000.00m

Clealco
Açúcar, Etanol e Energia

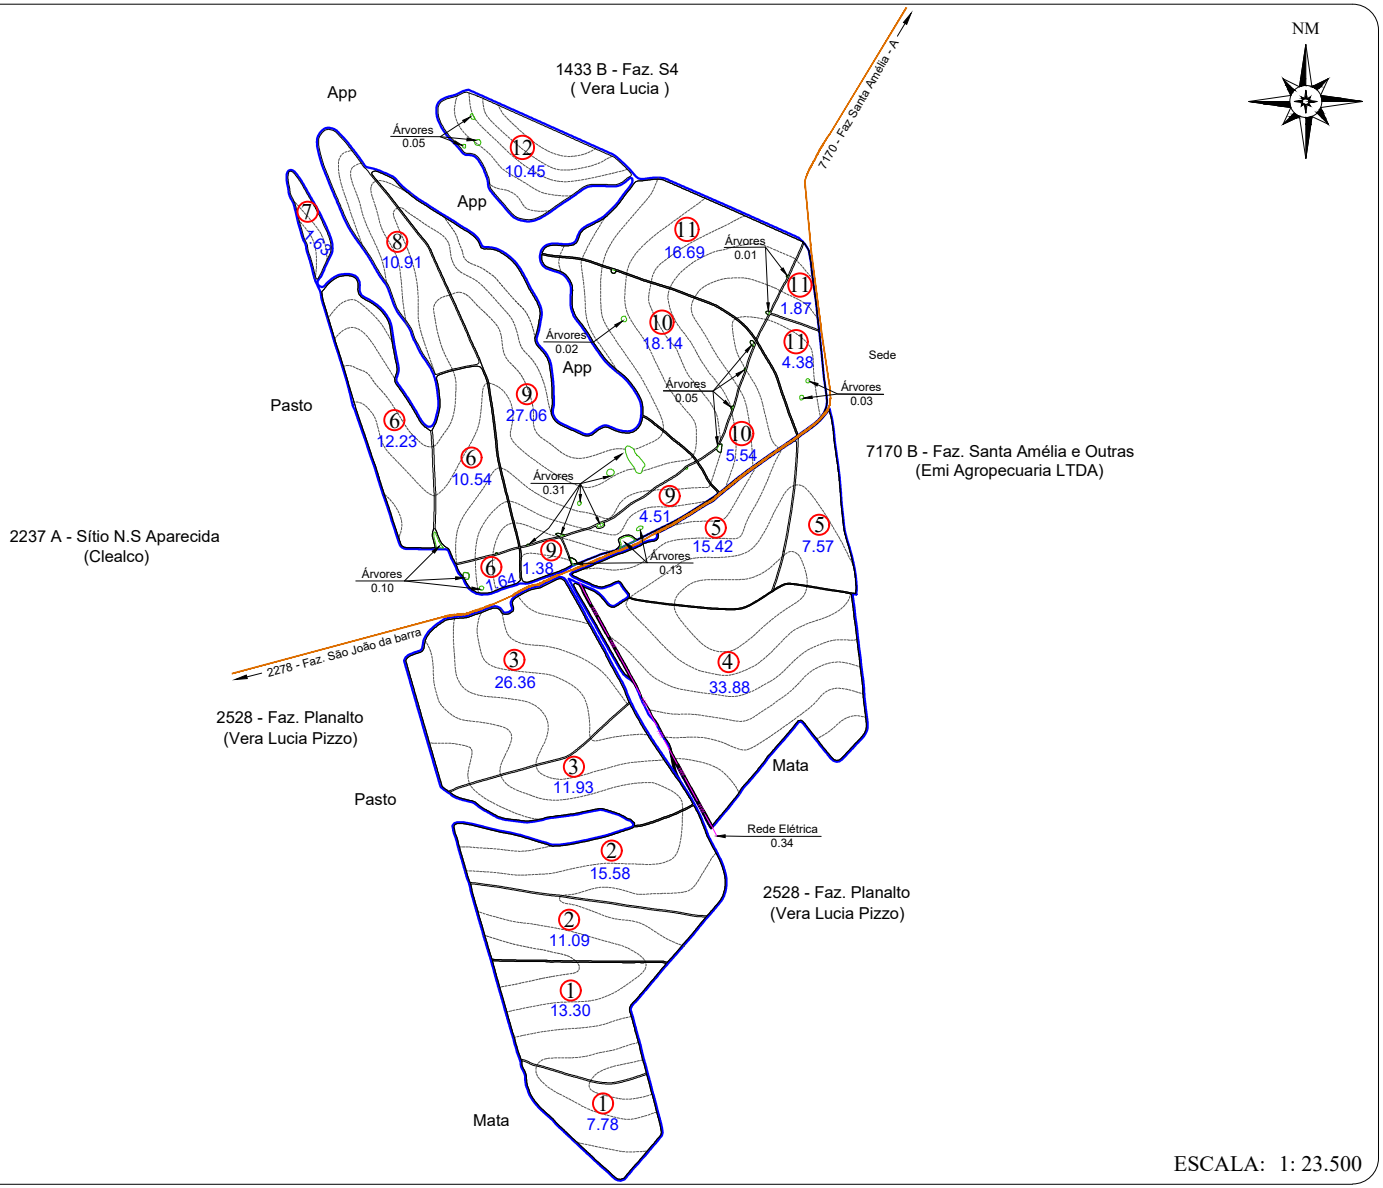


ESCALA: 1: 23.500

## CROQUI DE ACESSO

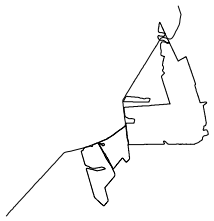

# FAZENDA SANTA AMÉLIA

PROPRIETÁRIO: EMI AGROPECUARIA LTDA
COMPRADOR: EUGENIO CARLOS FILHO
MUNICÍPIO: HERCULÂNDIA - SP

DISTÂNCIAS (km):
UNID. I - Asfalto: 25.80 Terra.: 28.87
UNID.I I - Asfalto: 18.00 Terra.: 10.10
UNID. III -Asfalto: 34.00 Terra.: 21.00

COORDENADAS: E(X): 565841.81 N(Y): 7586050.22
LAT: -21°49'41.5969" LONG: -50°21'46.4427"

CLEALCO - AÇÚCAR E ALCOOL S/A - DEPARTAMENTO DE TOPOGRAFIA

UNIDADE: II
PARTE: A/B
FUNDO AGRÍCOLA: 307170