ZONA D.V.	Nº TAL.	DATA PL.	ÁREA (ha)	VAR.
1 6.58%	13	06/2022	8.31	RB975242
	14		20.61	
	15		36.56	
	16		16.91	
	17		20.65	
	18		22.54	
	19		21.38	
	20		22.46	
	21		18.83	
	22		13.43	
	23		7.15	
	24		29.79	
	25		5.96	
	26		5.88	
	27		28.14	
	28		12.80	
	29		23.79	
	30		16.10	
	31		22.25	
	32		14.50	
	33		6.20	
TOTAL PLANTIO			374.24	--------


ÁREAS	(ha)	(%)
PLANTIO	374.24	96.57
CARREADORES	12.40	3.20
OUTROS	0.18	0.05
SUB TOTAL AGRICULTÁVEL	386.82	99.82
AP.P.	0.00	0.00
ÁRVORES	0.69	0.18
OUTROS	0.00	0.00
SUB TOTAL NÃO AGRICULT.	0.69	0.18
ÁREA TOTAL	387.51	100.00

C. NÍVEL: 41131.58 m/l 9.46 ha 2.44 %


LEGENDA

- FAZENDA
- TALHÃO
- CURVA DE NÍVEL
- CARREADOR
- CONFRONTANTE
- REDE ELÉTRICA
- TRAJETO VAZIO
- TRAJETO CARREGADO

PLANTIO MANUAL - ESPAÇAMENTO: 1.50 X 1.50
TIRO MÉDIO ESTIMADO: 000.00m

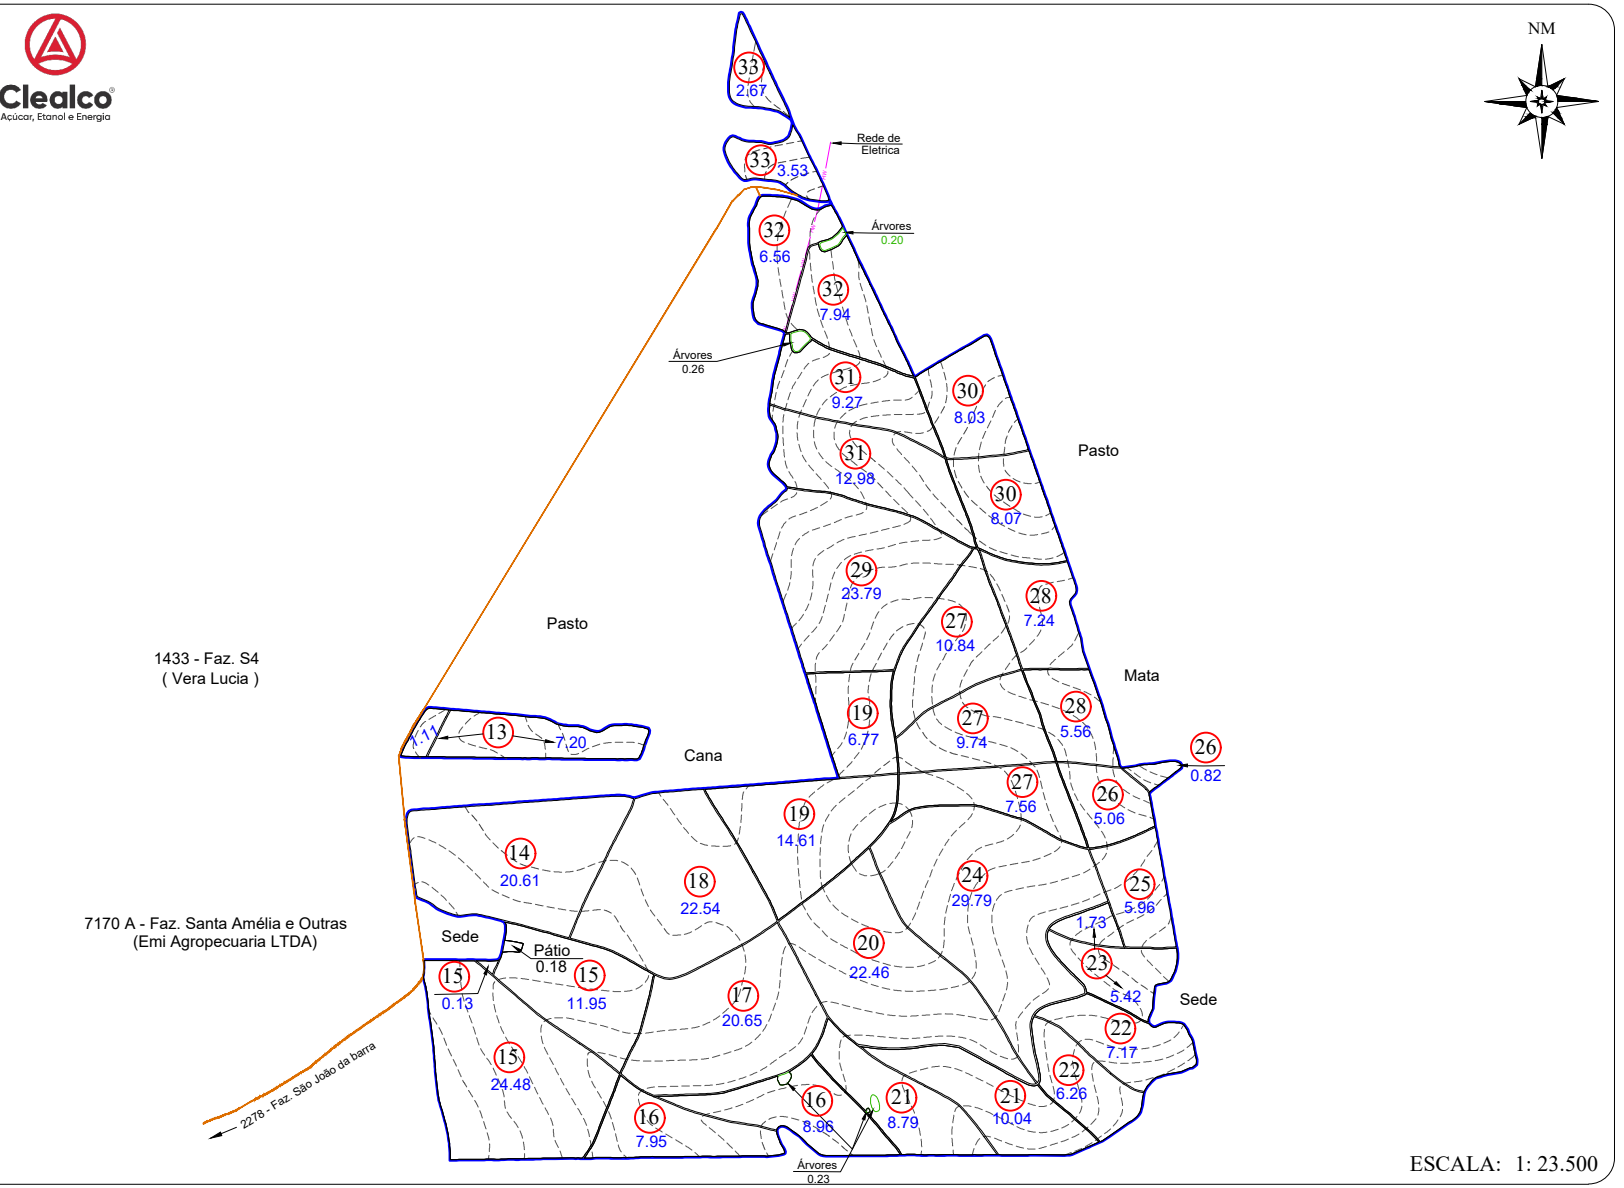

CROQUI DE ACESSO

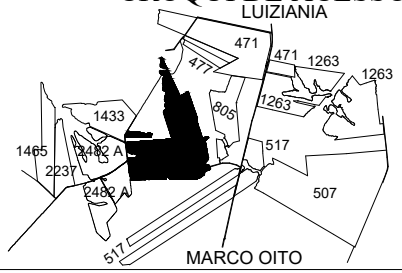

FAZENDA SANTA AMÉLIA

PROPRIETÁRIO: EMI AGROPECUARIA LTDA
COMPRADOR: EUGENIO CARLOS FILHO
MUNICÍPIO: HERCULÂNDIA - SP

DISTÂNCIAS (km):
UNID. I - Asfalto: 25.80 Terra.: 28.87
UNID.I I - Asfalto: 18.00 Terra.: 10.10
UNID. III -Asfalto: 34.00 Terra.: 21.00

COORDENADAS: E(X): 566482.51 N(Y): 7587420.23
LAT: -21°48'56.9531" LONG: -50°21'24.3248"

CLEALCO - AÇÚCAR E ALCOOL S/A - DEPARTAMENTO DE TOPOGRAFIA

UNIDADE: II
PARTE: B/B
FUNDO AGRÍCOLA: 307170