| ZONA D.V. | Nº TAL. | DATA PL. | ÁREA (ha) | VARIEDADE |
|---|---|---|---|---|
| 1<br>6.97 % | 1 | 04/2024 | 8.24 | RB 975201 |
| | 2 | | 15.83 | |
| | 3 | 07/2023 | 37.81 | RB 985476 |
| | 4 | | 44.06 | |
| | 5 | | 18.24 | |
| TOTAL PLANTIO | | | 124.18 | -------- |

| ÁREAS | (ha) | (%) |
|---|---|---|
| PLANTIO | 124.18 | 94.00 |
| CARREADORES | 6.10 | 4.62 |
| OUTROS | 0.00 | 0.00 |
| SUB TOTAL AGRICULTÁVEL | 130.28 | 98.62 |
| AP.P. | 0.00 | 0.00 |
| ÁRVORES | 0.50 | 0.38 |
| OUTROS | 1.32 | 1.00 |
| SUB TOTAL NÃO AGRICULT. | 1.82 | 1.38 |
| ÁREA TOTAL | 132.10 | 100.00 |

C. NÍVEL: 10571.16 m/l 2.43 ha 1.84 %

## LEGENDA


- FAZENDA
- TALHÃO
- CURVA DE NÍVEL
- CARREADOR
- CONFRONTANTE
- REDE ELÉTRICA
- TRAJETO VAZIO
- TRAJETO CARREGADO

ESPAÇAMENTO: 1.50 x 1.50

TIRO MÉDIO ESTIMADO: 284.00 m


Clealco
Açúcar, Etanol e Energia

NM

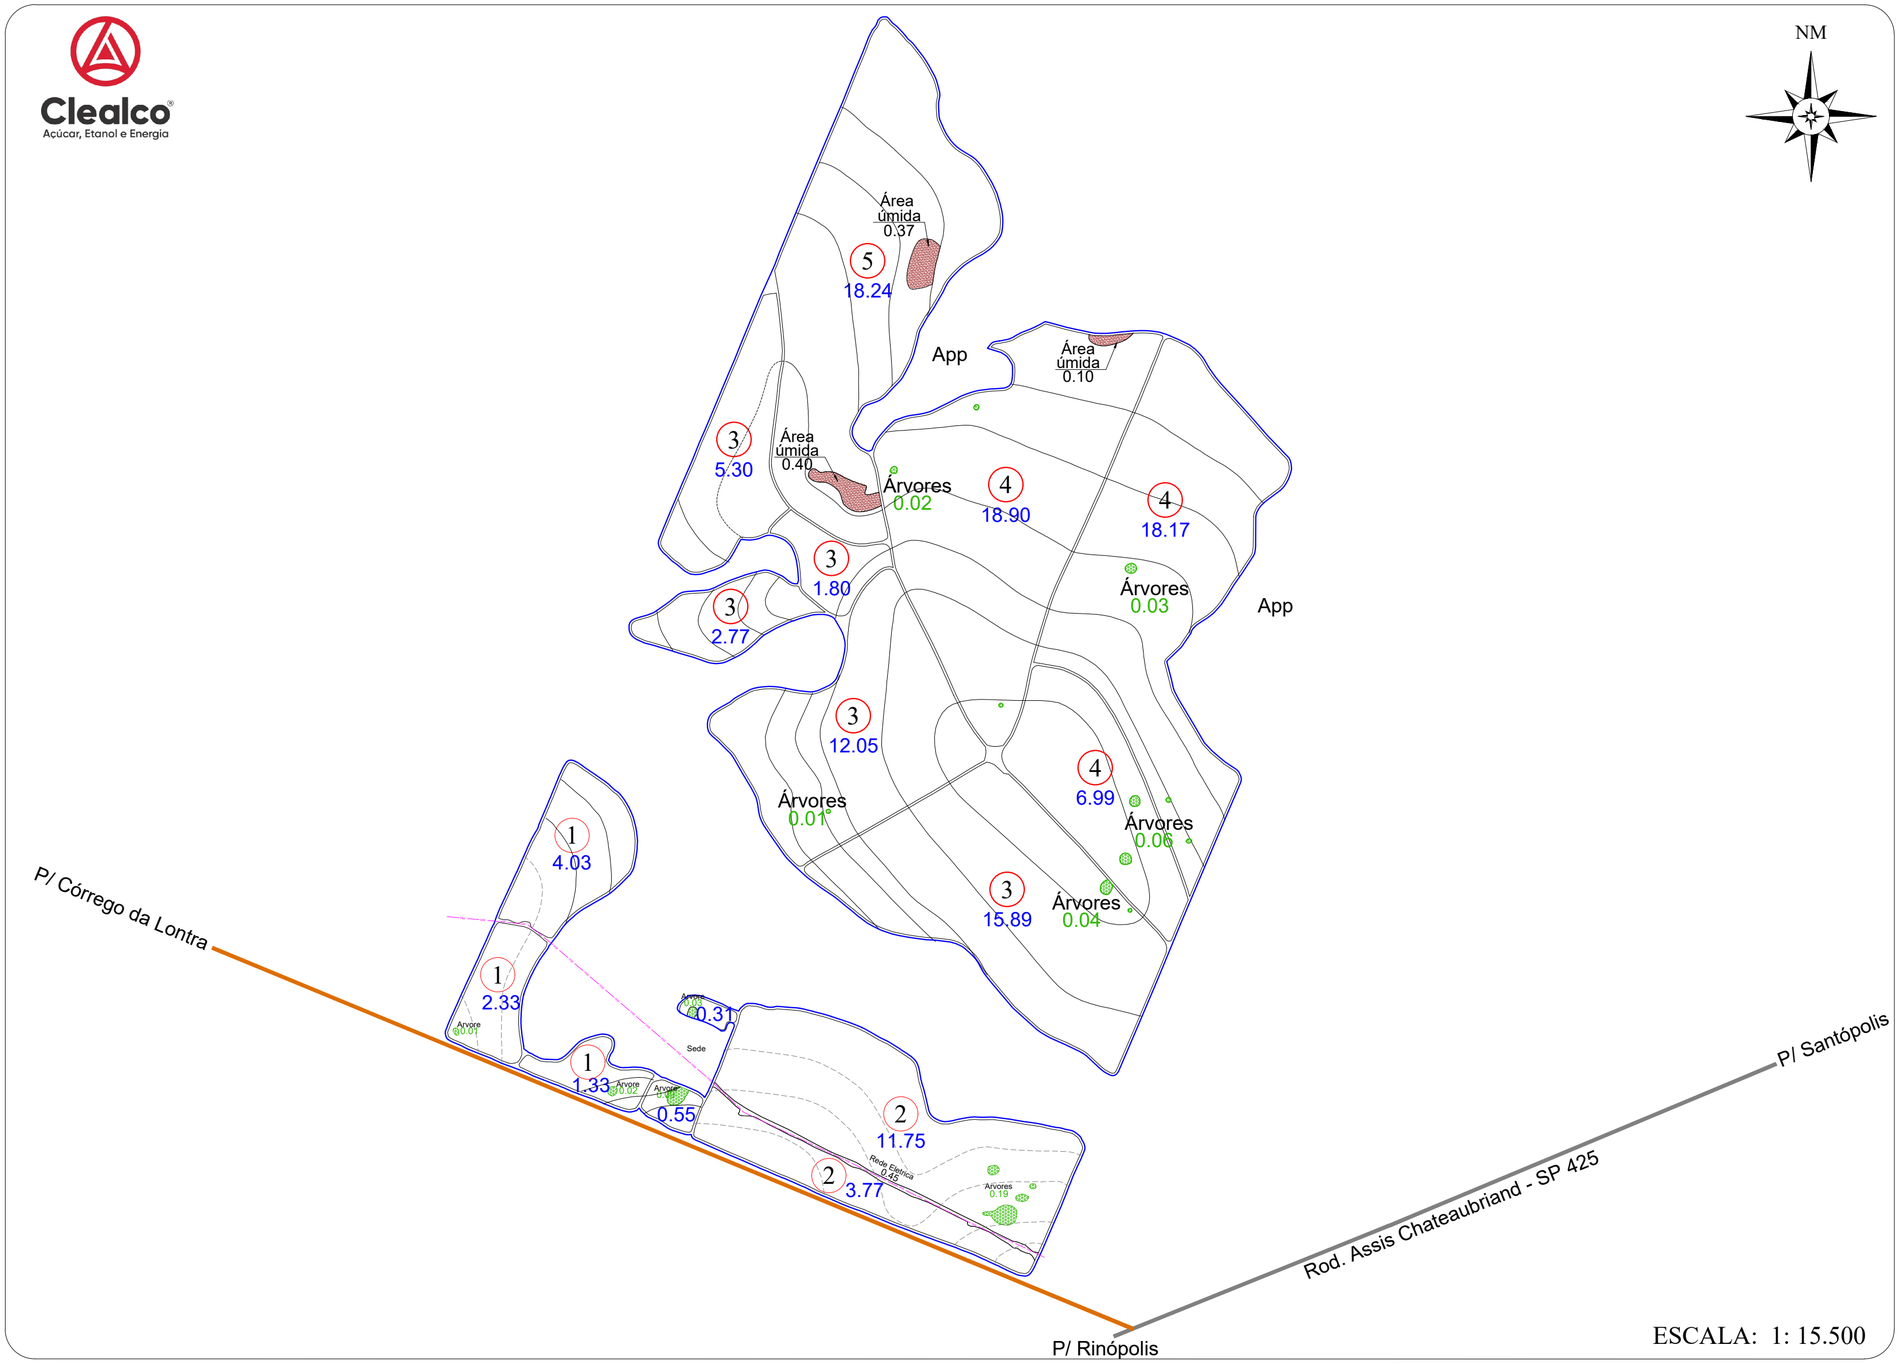


ESCALA: 1: 15.500

## CROQUI DE ACESSO

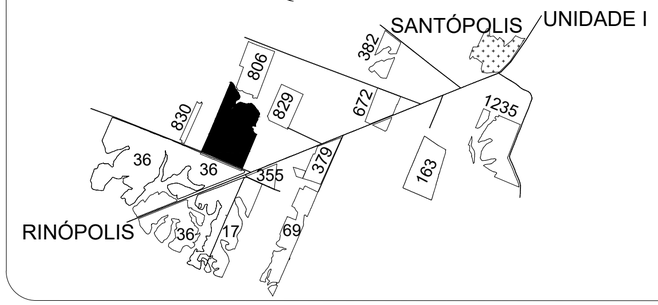


# SÍTIO ALVORADA

PROPRIETÁRIO: EMI AGROPECUÁRIA LTDA
COMPRADOR: CLEALCO S/A
MUNICÍPIO: SANTÓPOLIS DO AGUAPEI

DISTÂNCIAS (km):

| | | | |
|---|---|---|---|
| UNID. I - Asfalto: | 20.00 | Terra.: | 1.20 |
| UNID.I I - Asfalto: | 55.00 | Terra.: | 1.20 |
| UNID. III -Asfalto: | 26.00 | Terra.: | 1.20 |

COORDENADAS: E(X): 545328.03 N(Y): 7605535.45
LAT: -21°39'10.1780" LONG: -50°33'42.9298"

CLEALCO - AÇÚCAR E ALCOOL S/A - DEPARTAMENTO DE TOPOGRAFIA

UNIDADE: I

PARTE: A/A

FUNDO AGRÍCOLA: 307558

M:\01-Mapa de safra\Mapas Atualizados\Acionista\Kenkiti Kimura\307558 - Sítio Alvorada (Emi Agropecuária)\307558 - Sítio Alvorada (Emi Agropecuária).dwg

Benati 02/10/2024