
Clealco
Açúcar, Etanol e Energia

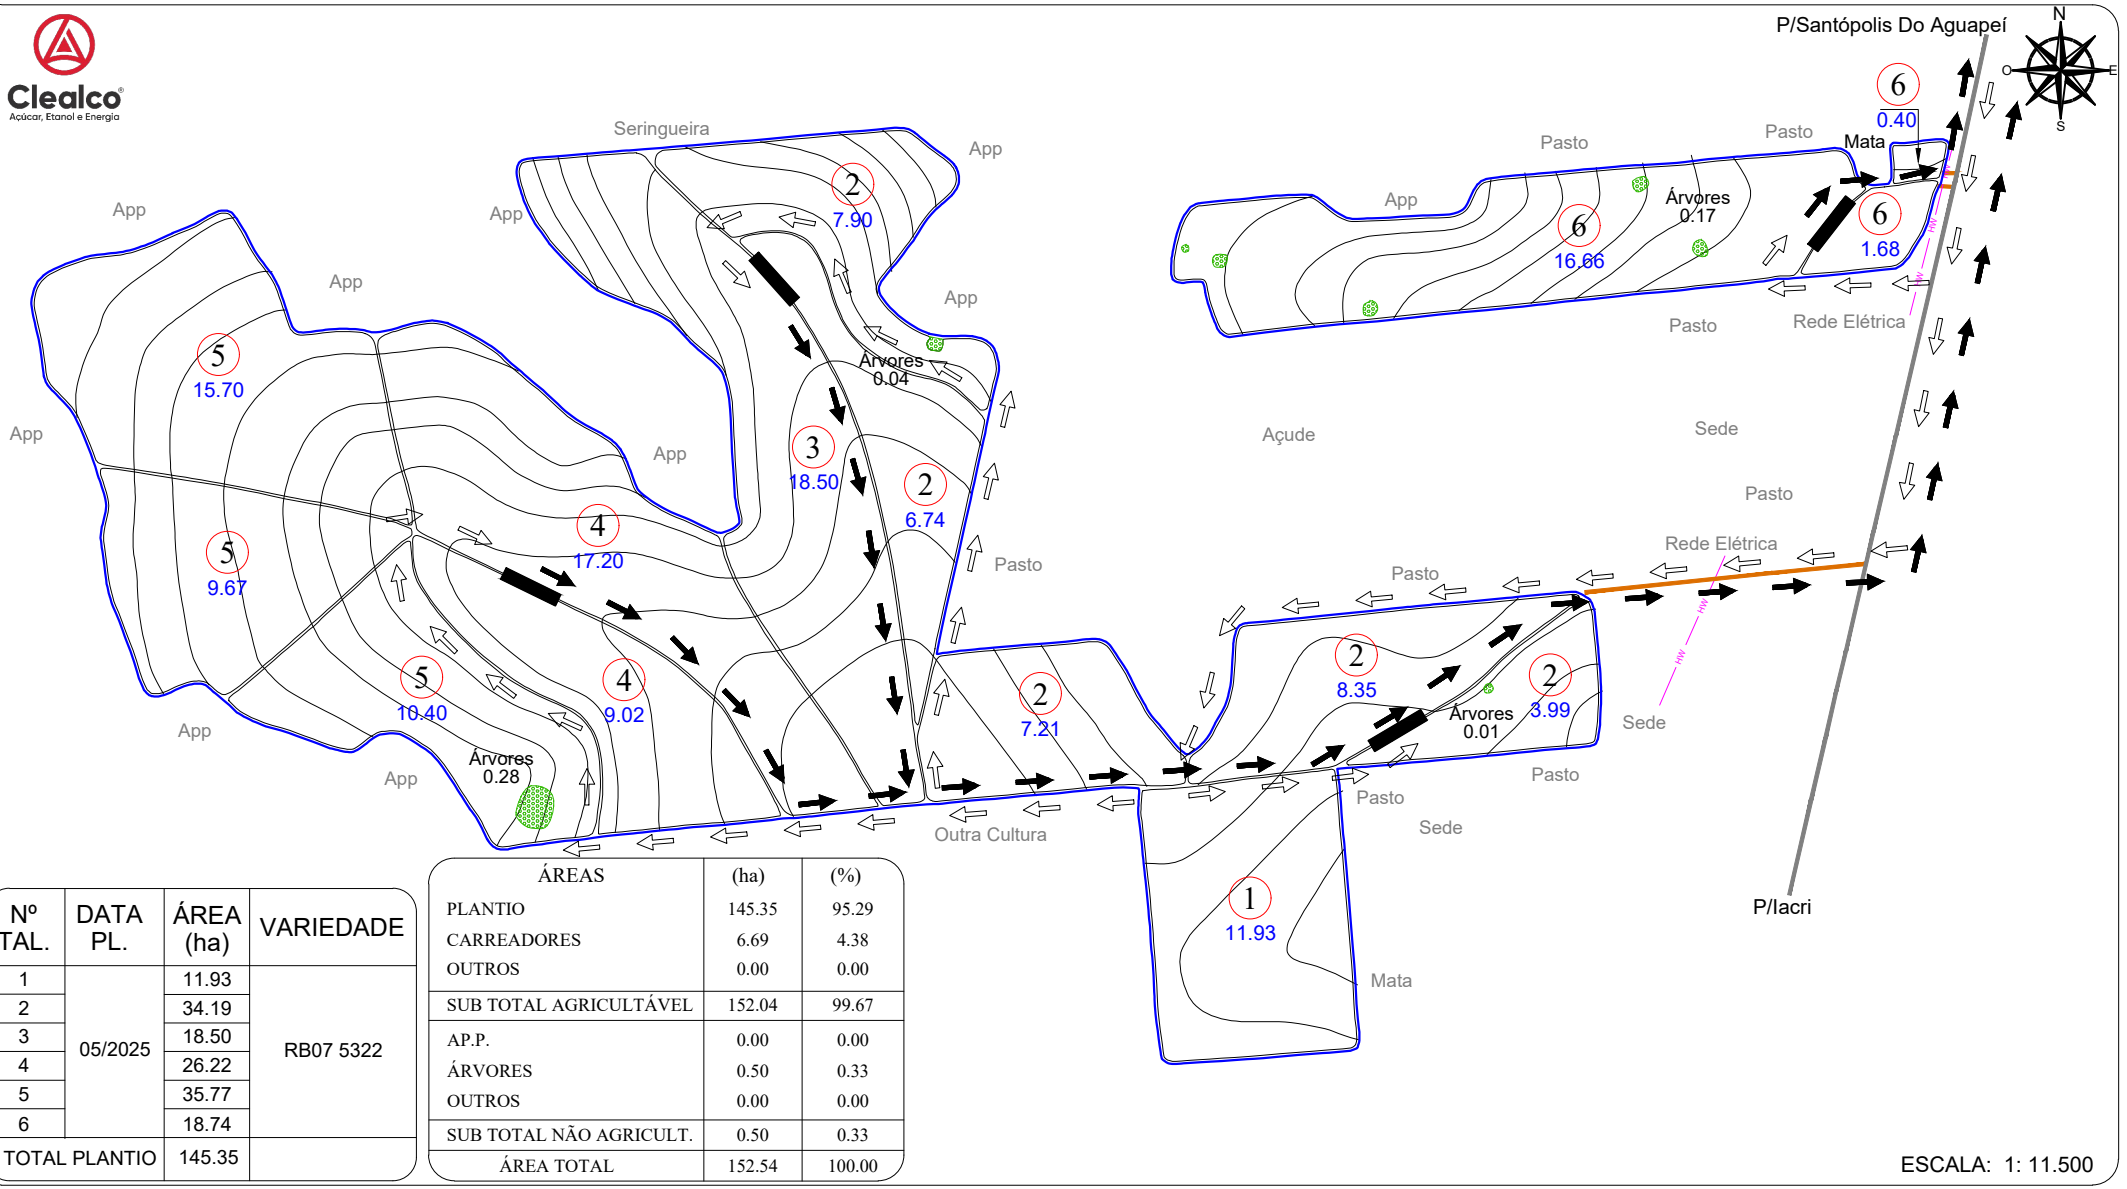

Nº TAL.	DATA PL.	ÁREA (ha)	VARIEDADE
1	05/2025	11.93	RB07 5322
2		34.19	
3		18.50	
4		26.22	
5		35.77	
6		18.74	
TOTAL PLANTIO		145.35	

ÁREAS	(ha)	(%)
PLANTIO	145.35	95.29
CARREADORES	6.69	4.38
OUTROS	0.00	0.00
SUB TOTAL AGRICULTÁVEL	152.04	99.67
AP.P.	0.00	0.00
ÁRVORES	0.50	0.33
OUTROS	0.00	0.00
SUB TOTAL NÃO AGRICULT.	0.50	0.33
ÁREA TOTAL	152.54	100.00


ESCALA: 1: 11.500

LEGENDA

- FAZENDA
- TALHÃO
- REDE ELÉTRICA
- TERRAÇO BASE LARGA
- TERRAÇO EMBUTIDO
- VAZIO
- CARREGADO

ESPAÇAMENTO: 1.50 x 1.50
TIRO MÉDIO ESTIMADO: 256.69 m
D.V: 4.87 %

CROQUI DE ACESSO

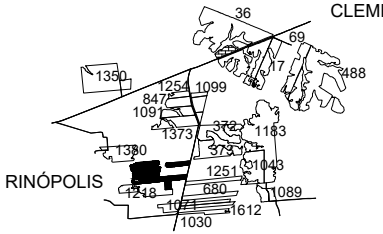

FAZENDA TRIÂNGULO III

PROPRIETÁRIO: FLORINDO PINATTO
COMPRADOR: LUCIANO DE PÁDUA CINTRA
MUNICÍPIO: IACRI

DISTÂNCIAS (km):
UNID. I - Asfalto: 27.00 Terra.: 1.50
UNID.I I - Asfalto: 65.00 Terra.: 1.50

COORDENADAS: E(X): 540814.91 N(Y): 7597994.19
LAT: -21°43'15.8504" LONG: -50°36'19.2814"
CLEALCO - AÇÚCAR E ALCOOL S/A - DEPARTAMENTO DE GEOTECNOLOGIA

SATÉLITE
GPS / VANT
GOOGLE

UNIDADE: I
PARTE: A/A
FUNDO AGRÍCOLA: 300838

M:\01-Mapa de safra\Mapas Atualizados\Acionista\Luciano de Padua Cintra\300838 - Fazenda Triangulo III (Florindo Pinatto)\300838 - Fazenda Triangulo III (Florindo Pinatto).dwg

Bruno Gamboa 22/01/26