ZONA DV	Nº TAL.	DATA PL.	ÁREA (ha)	VARIEDADE
1 4.00 %	1	06/2022	20.91	RB 985476
	2		46.88	
	3		10.21	
	4	04/2024	2.03	
TOTAL PLANTIO			80.03	--------


ÁREAS	(ha)	(%)
PLANTIO	80.03	95.29
CARREADORES	3.46	4.12
OUTROS	0.00	0.00
SUB TOTAL AGRICULTÁVEL	83.49	99.40
AP.P.	0.00	0.00
ÁRVORES	0.04	0.05
OUTROS	0.46	0.55
SUB TOTAL NÃO AGRICULT.	0.50	0.60
ÁREA TOTAL	83.99	100.00

C. NÍVEL: 9691.22 m/l 2.23 ha 2.65 %


LEGENDA

- FAZENDA
- TALHÃO
- CURVA DE NÍVEL
- CARREADOR
- CONFRONTANTE
- REDE ELÉTRICA
- TRAJETO VAZIO
- TRAJETO CARREGADO

PLANTIO MANUAL - ESPAÇAMENTO: 1.50 X 1.50
TIRO MÉDIO ESTIMADO: 438.50 m

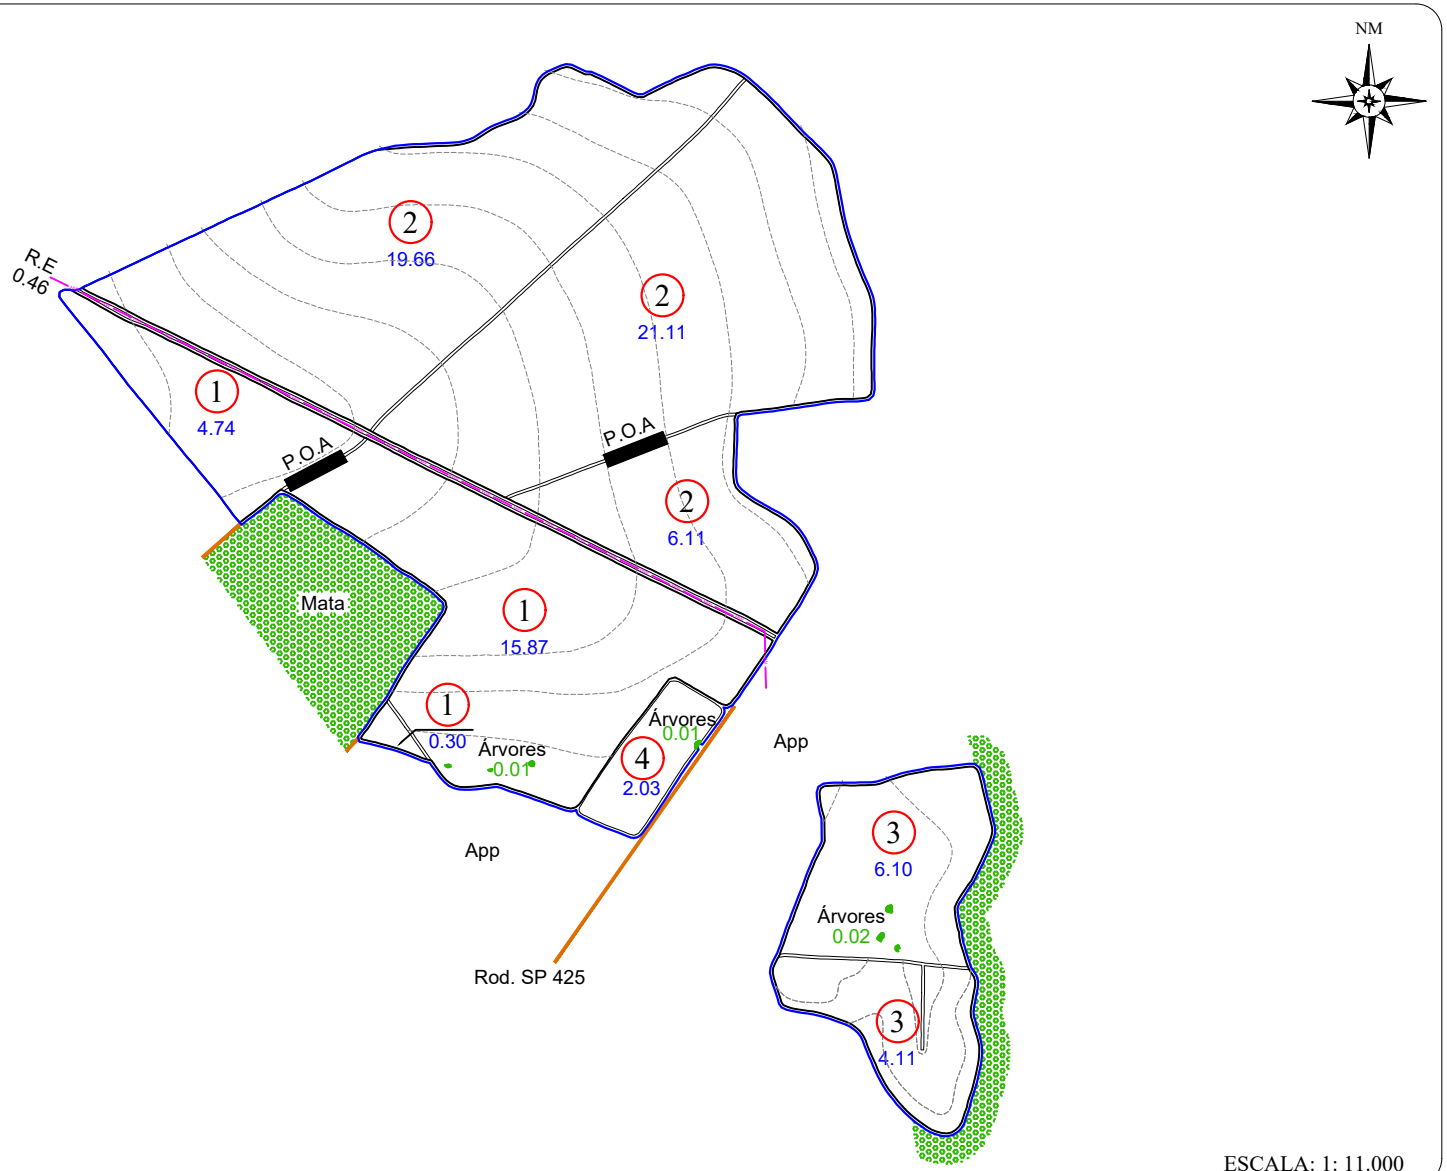

CROQUI DE ACESSO

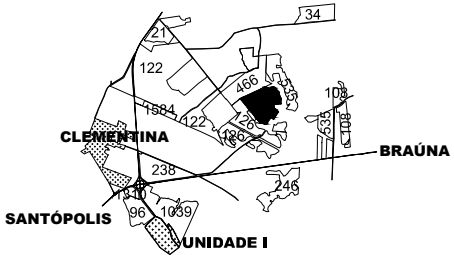

FAZENDA SÃO LUIZ

PROPRIETÁRIO: LUCIANO DE PÁDUA CINTRA
ARRENDATÁRIO: CLEALCO S/A
MUNICÍPIO: CLEMENTINA

DISTÂNCIAS (km):

UNID. I -	Asfalto:	3.30	Terra.:	2.60
UNID.I I -	Asfalto:	59.00	Terra.:	5.00
UNID. III -	Asfalto:	49.60	Terra.:	2.60

COORDENADAS: E(X): 562209.91 N(Y): 7616255.58
LAT: -21°33'19.6770" LONG: -50°23'57.0305"

CLEALCO - AÇÚCAR E ALCOOL S/A - DEPARTAMENTO DE TOPOGRAFIA

UNIDADE: I

PARTE: A/A

FUNDO AGRÍCOLA: 301034