
Clealco
Açúcar, Etanol e Energia

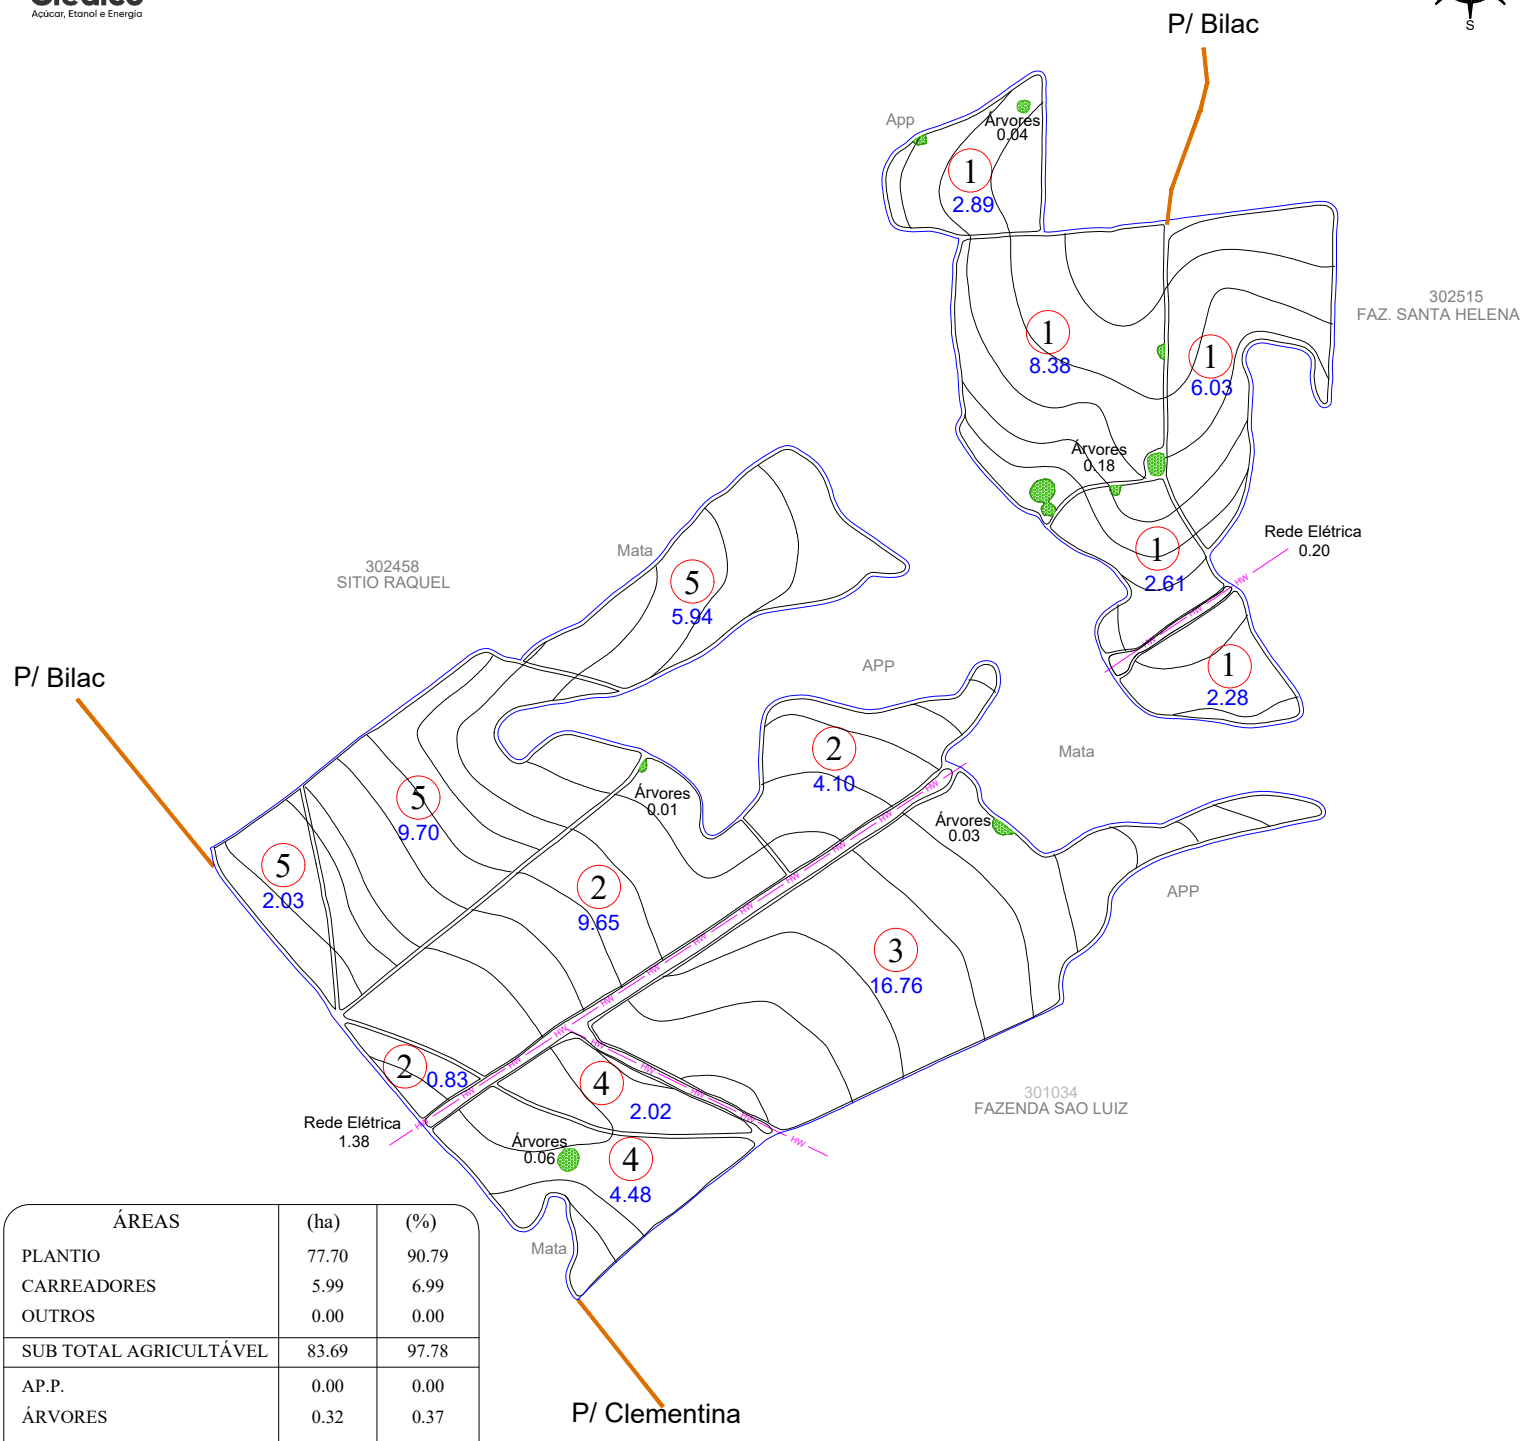

ÁREAS	(ha)	(%)
PLANTIO	77.70	90.79
CARREADORES	5.99	6.99
OUTROS	0.00	0.00
SUB TOTAL AGRICULTÁVEL	83.69	97.78
AP.P.	0.00	0.00
ÁRVORES	0.32	0.37
OUTROS	1.58	1.85
SUB TOTAL NÃO AGRICULT.	1.90	2.22
ÁREA TOTAL	85.59	100.00

C. NÍVEL: 11508.91 m/l 2.65 ha 3.09 %

LEGENDA


- FAZENDA
- TALHÃO
- REDE ELÉTRICA
- TERRAÇO BASE LARGA
- TERRAÇO EMBUTIDO
- (P.O.A) PATIO DE OPERAÇÃO

ESPAÇAMENTO: 1.50 x 1.50
TIRO MÉDIO ESTIMADO: 155.89 m
D.V: 6.00 %

Nº TAL.	DATA PL.	ÁREA (ha)	VARIEDADE
1	06/2024	22.19	RB97 5033
2		14.58	
3		16.76	
4		6.50	
5	2026	17.67	PRÉ PLANTIO
TOTAL PLANTIO		77.70	

ESCALA: 1: 10.000

CROQUI DE ACESSO

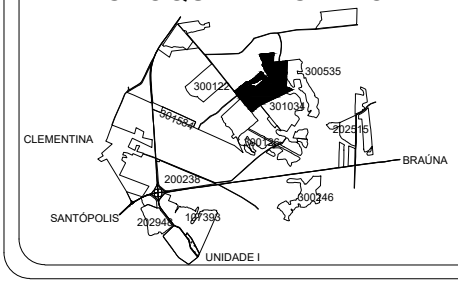

SÍTIO RECANTO III

PROPRIETÁRIO: LUCIANO DE PÁDUA CINTRA
COMPRADOR: CLEALCO
MUNICÍPIO: CLEMENTINA - SP

DISTÂNCIAS (km):
UNID. I - Asfalto: 7.50 Terra.: 3.00
UNID.I I - Asfalto: 66.50 Terra.: 3.00

COORDENADAS: E(X): 560590.0348 N(Y): 7617644.2959
LAT: 21° 32' 34,70990" LONG: 50° 24' 53,53061"

CLEALCO - AÇÚCAR E ALCOOL S/A - DEPARTAMENTO DE GEOTECNOLOGIA

LEVANTAMENTO VIA:
- SATÉLITE
- GPS / VANT
- GOOGLE

UNIDADE: I
PARTE: A/A
FUNDO AGRÍCOLA: 301446

M:\01-Mapa de safra\Mapas Atualizados\Acionista\Luciano de Padua Cintra\301446 - Sítio Recanto III (Luciano de Padua Cintra)\301446 - Sítio Recanto III (Luciano de Padua Cintra).dwg

Bruno Gamboa 03/06/26