
Clealco
Açúcar, Etanol e Energia

Pos Plantio

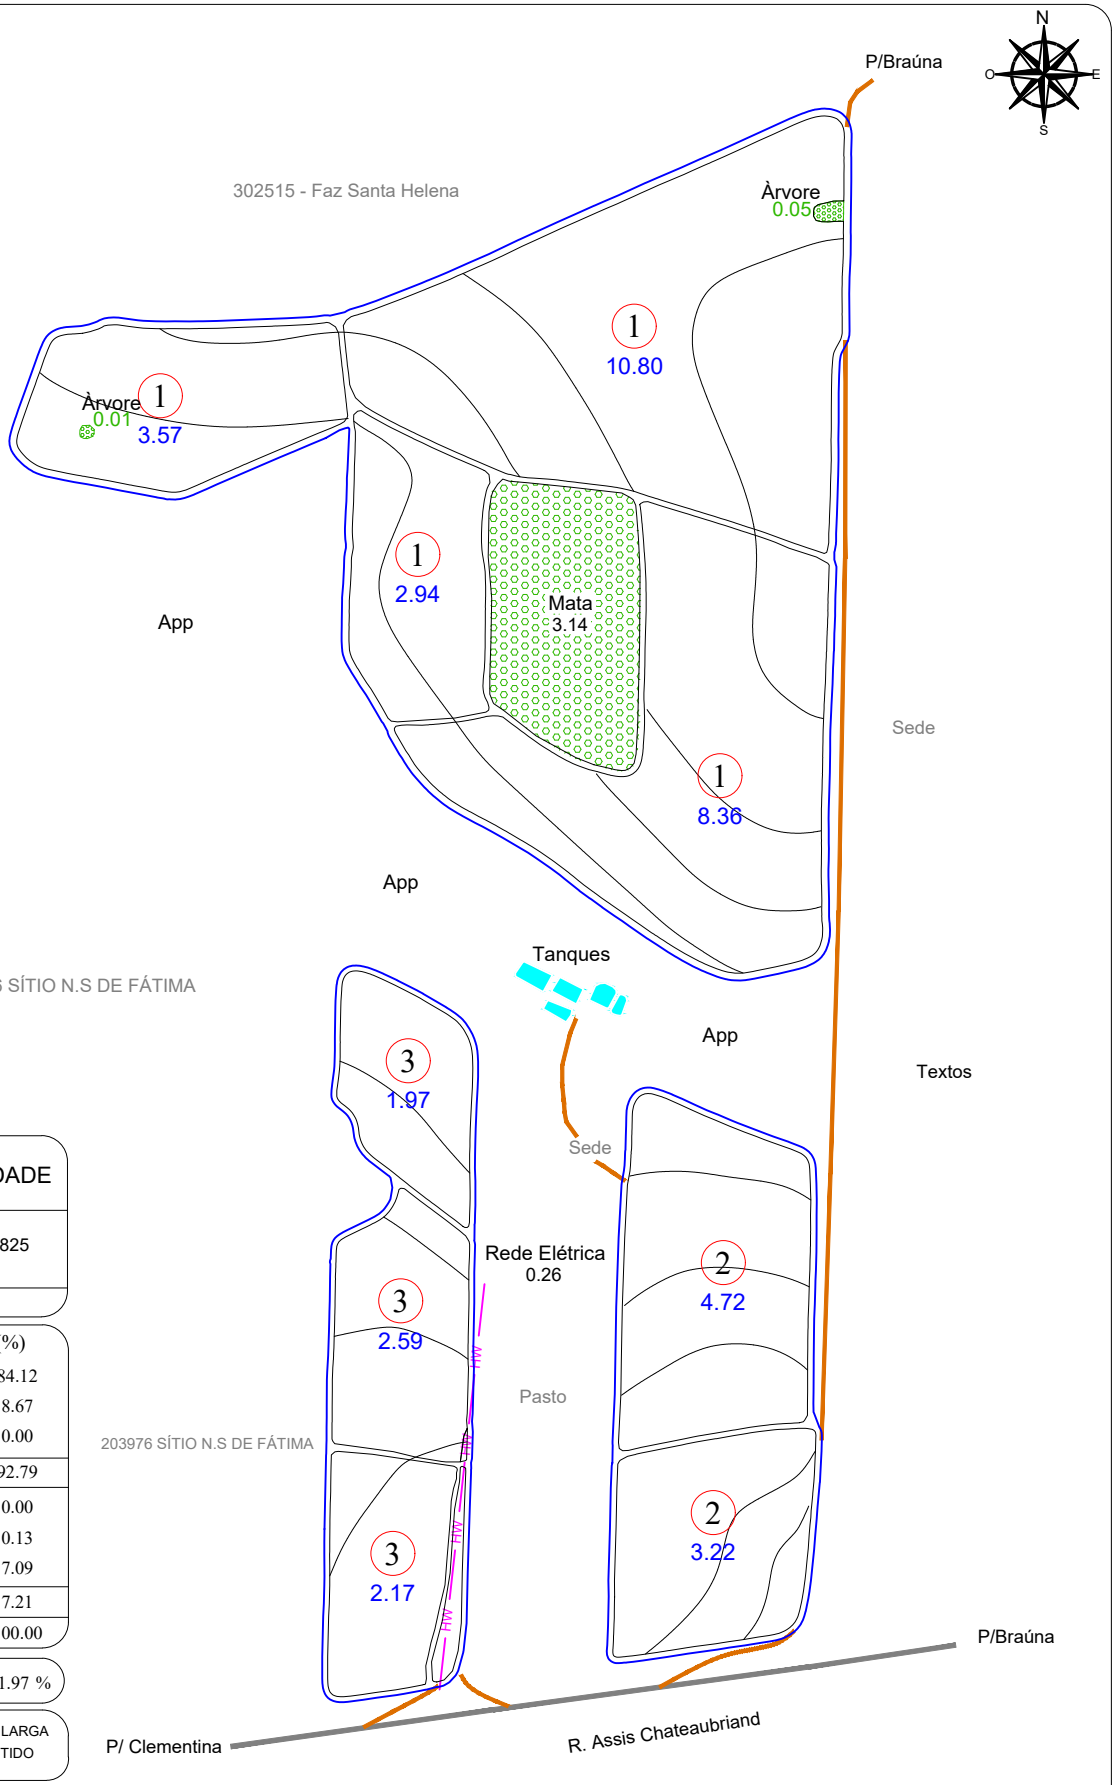


| D.V. | Nº TAL. | DATA PL. | ÁREA (ha) | VARIEDADE |
|---|---|---|---|---|
| 5.09 % | 1 | 03/2025 | 25.67 | RB 127825 |
| | 2 | | 7.94 | |
| | 3 | | 6.73 | |
| TOTAL PLANTIO | | | 40.34 | |

| ÁREAS | (ha) | (%) |
|---|---|---|
| PLANTIO | 40.34 | 84.12 |
| CARREADORES | 4.16 | 8.67 |
| OUTROS | 0.00 | 0.00 |
| SUB TOTAL AGRICULTÁVEL | 44.50 | 92.79 |
| AP.P. | 0.00 | 0.00 |
| ÁRVORES | 0.06 | 0.13 |
| OUTROS | 3.40 | 7.09 |
| SUB TOTAL NÃO AGRICULT. | 3.46 | 7.21 |
| ÁREA TOTAL | 47.96 | 100.00 |

C. NÍVEL: 4103.16 m/l 0.94 ha 1.97 %


LEGENDA

FAZENDA
TALHÃO
REDE ELÉTRICA
TERRAÇO BASE LARGA
TERRAÇO EMBUTIDO

ESPAÇAMENTO: 1.50 x 1.50
TIRO MÉDIO ESTIMADO: 184.78 m

ESCALA: 1: 7.000

## CROQUI DE ACESSO

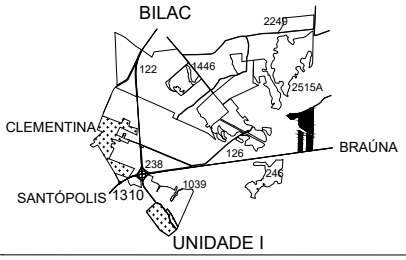


# FAZENDA SANTA HELENA

PROPRIETÁRIO: ANALICE BRANDÃO LEMOS
COMPRADOR: LUCIANO DE PÁDUA CINTRA
MUNICÍPIO: BRAÚNA - SP

DISTÂNCIAS (km):
UNID. I - Asfalto: 7.00 Terra.: 1.50
UNID.I I - Asfalto: 61.90 Terra.: 1.50
UNID. III -Asfalto: 37.00 Terra.: 1.50

COORDENADAS: E(X): 563509.78 N(Y): 7616287.09
LAT: 21º 33' 18, 48743" LONG: 50º 23' 11, 84172"

CLEALCO - AÇÚCAR E ALCOOL S/A - DEPARTAMENTO DE TOPOGRAFIA

UNIDADE:
I
PARTE:
B/B
FUNDO AGRÍCOLA:
302515

M:\01-Mapa de safra\Mapas Atualizados\Acionista\Luciano de Padua Cintra\302515 - Fazenda Santa Helena (Luciano de Pádua Cintra)\302515 B - Fazenda Santa Helena (Luciano de Pádua Cintra).dwg

Benati 02/07/2025