ZONA DV	Nº TAL.	DATA PL.	ÁREA (ha)	VARIEDADE
1 5.71 %	122	05/2022	17.36	RB 975242
	222		20.89	
	322		20.27	
TOTAL PLANTIO			58.52	--------


ÁREAS	(ha)	(%)
PLANTIO	58.52	94.97
CARREADORES	2.93	4.75
OUTROS	0.00	0.00
SUB TOTAL AGRICULTÁVEL	61.45	99.72
AP.P.	0.00	0.00
ÁRVORES	0.01	0.02
OUTROS	0.16	0.26
SUB TOTAL NÃO AGRICULT.	0.17	0.28
ÁREA TOTAL	61.62	100.00

C. NÍVEL: 0.00 m/l 0.00 ha 0.00 %

LEGENDA


- FAZENDA
- TALHÃO
- CURVA DE NÍVEL
- CARREADOR
- CONFRONTANTE
- REDE ELÉTRICA
- TRAJETO VAZIO
- TRAJETO CARREGADO

PLANTIO MANUAL - ESPAÇAMENTO: 1.50 X 1.50
TIRO MÉDIO ESTIMADO: 000.00 m

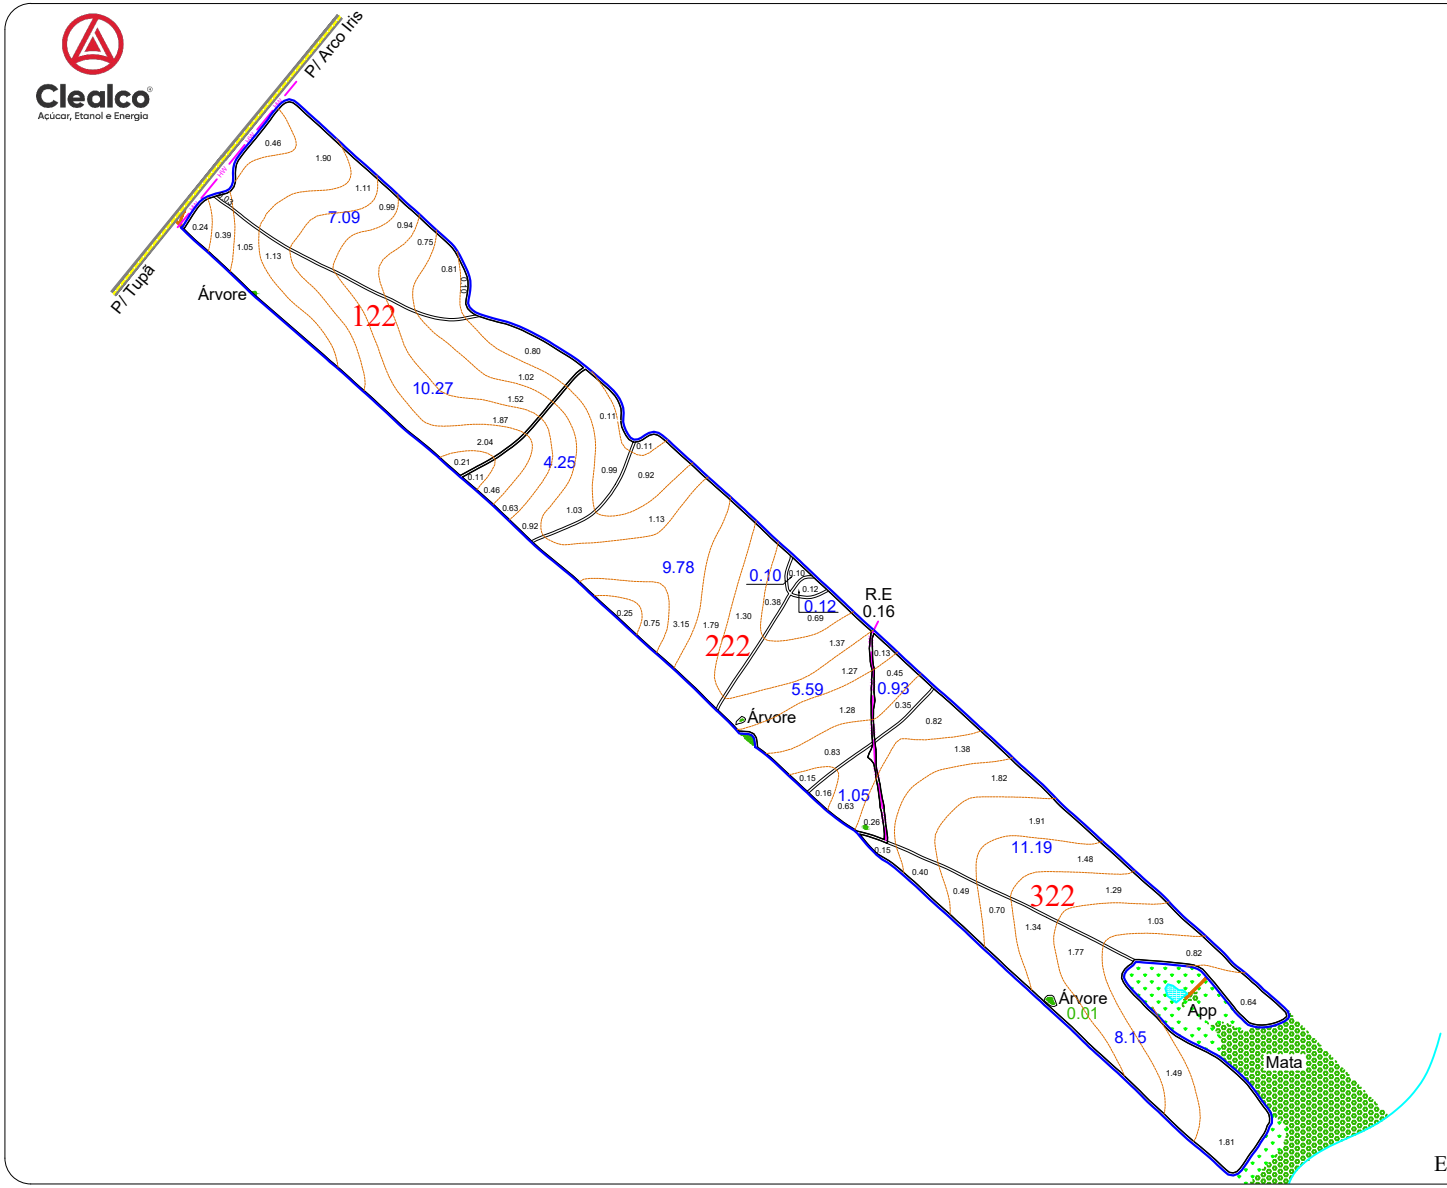

ESCALA: 1: 13.000

CROQUI DE ACESSO

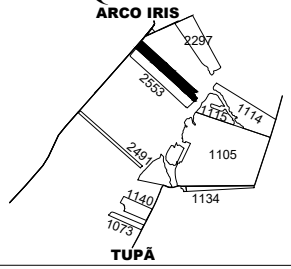

SÍTIO SANTA LUZIA

PROPRIETÁRIO: ROGÉRIO SANCHES VELINI
COMPRADOR: CLEALCO S/A
MUNICÍPIO: TUPÃ

DISTÂNCIAS (km):
UNID. I - Asfalto: 31.00 Terra.: 9.50
UNID.I I - Asfalto: 38.50 Terra.: 9.50
UNID. III -Asfalto: 50.00 Terra.: 9.50

COORDENADAS: E(X): 555671.77 N(Y): 7583348.42
LAT: -21°51'10.7310" LONG: -50°27'40.3673"

CLEALCO - AÇÚCAR E ALCOOL S/A - DEPARTAMENTO DE TOPOGRAFIA

UNIDADE: I
PARTE: A/A
FUNDO AGRÍCOLA: 302552