
Clealco
Açúcar, Etanol e Energia

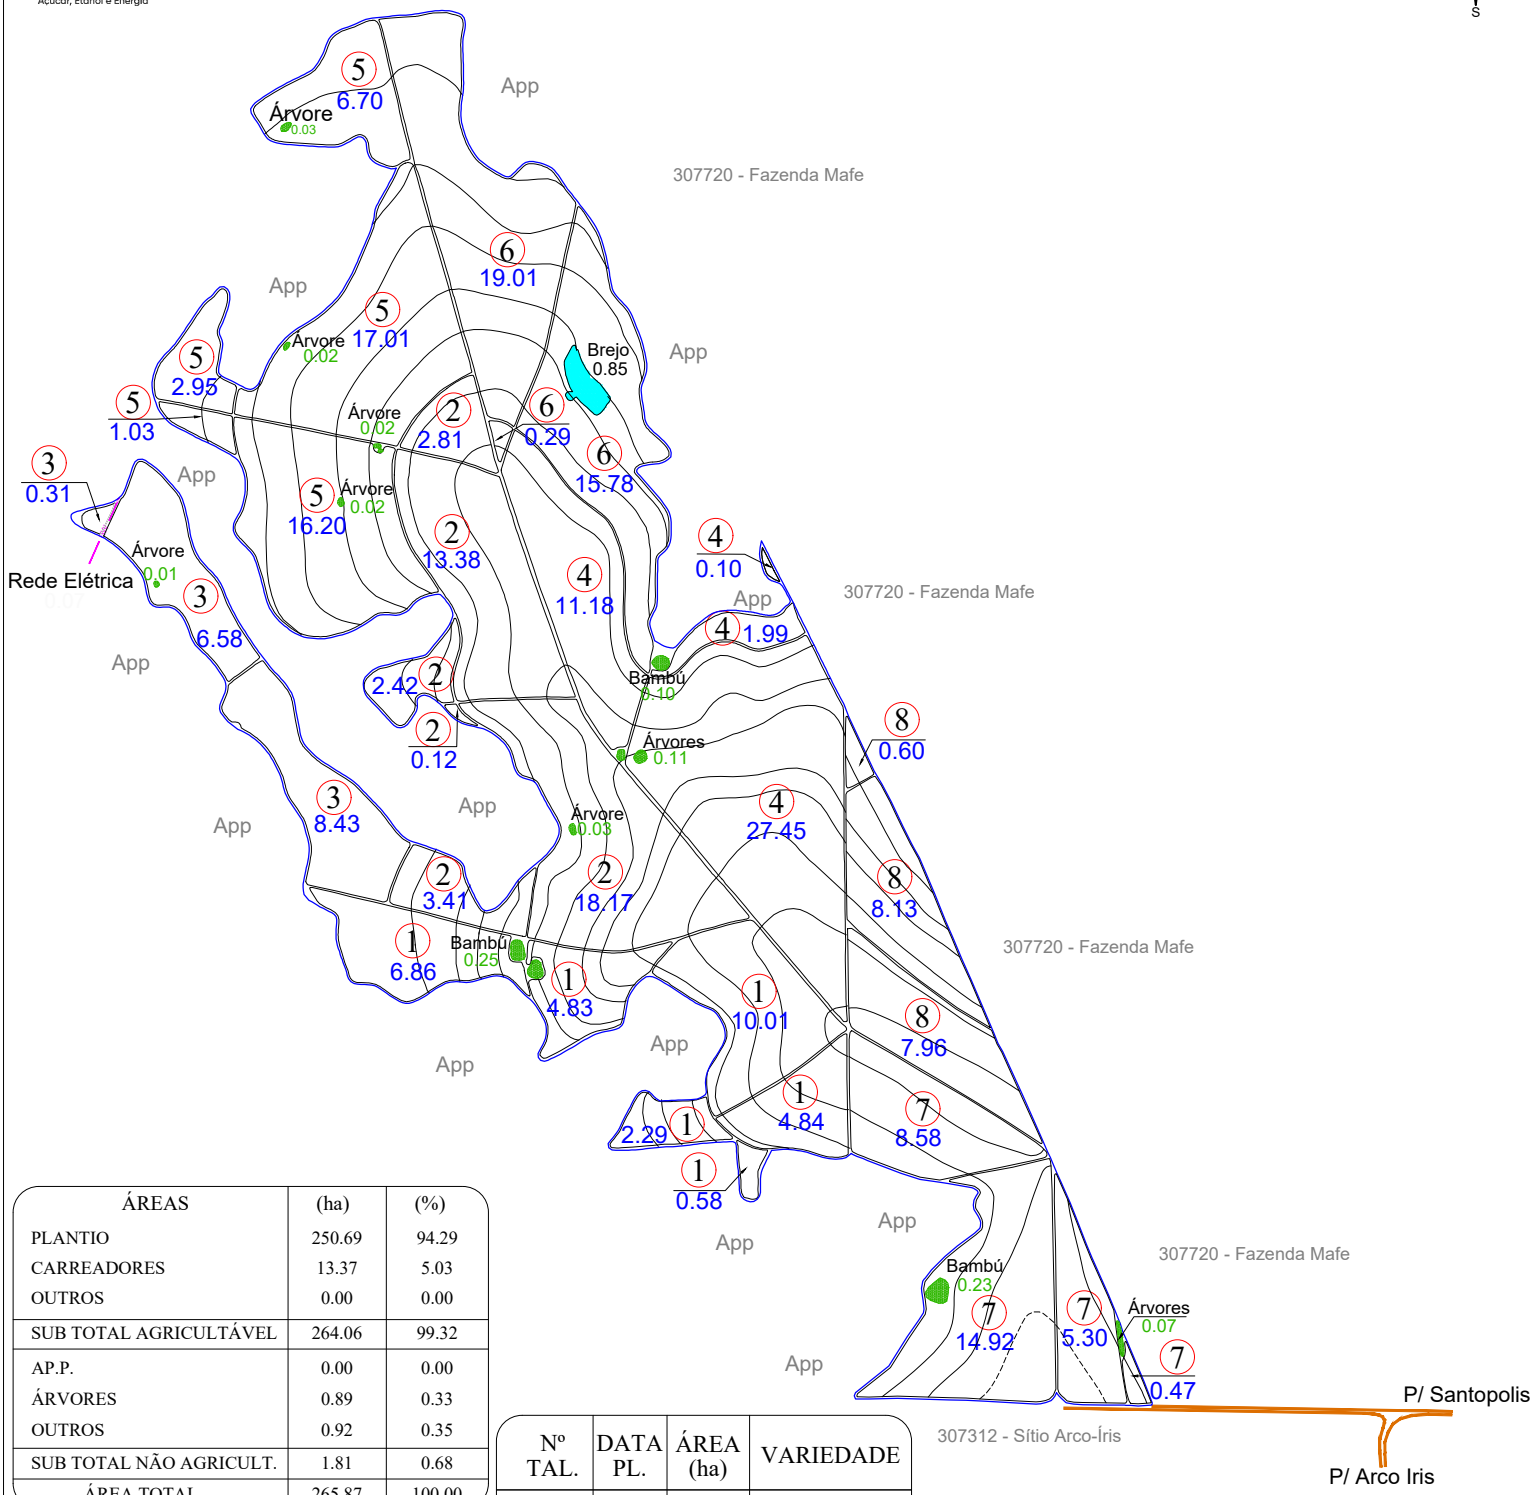


| ÁREAS | (ha) | (%) |
|---|---|---|
| PLANTIO | 250.69 | 94.29 |
| CARREADORES | 13.37 | 5.03 |
| OUTROS | 0.00 | 0.00 |
| SUB TOTAL AGRICULTÁVEL | 264.06 | 99.32 |
| AP.P. | 0.00 | 0.00 |
| ÁRVORES | 0.89 | 0.33 |
| OUTROS | 0.92 | 0.35 |
| SUB TOTAL NÃO AGRICULT. | 1.81 | 0.68 |
| ÁREA TOTAL | 265.87 | 100.00 |

C. NÍVEL: 25941.11 m/l 5.97 ha 2.24 %

LEGENDA


- FAZENDA
- TALHÃO
- REDE ELÉTRICA
- TERRAÇO BASE LARGA
- TERRAÇO EMBUTIDO
- (P.O.A) PATIO DE OPERAÇÃO

ESPAÇAMENTO: 1.50 x 1.50
TIRO MÉDIO ESTIMADO: 202.04m
D.V: 4.80 %

| Nº TAL. | DATA PL. | ÁREA (ha) | VARIEDADE |
|---|---|---|---|
| 1 | 05/2024 | 29.41 | RB975242 |
| 2 | | 40.31 | RB975201 / RB975242 |
| 3 | | 15.32 | RB975242 |
| 4 | | 40.72 | |
| 5 | | 43.89 | RB975201 |
| 6 | | 35.08 | |
| 7 | 05/2025 | 29.27 | RB07 5322 |
| 8 | | 16.69 | |
| TOTAL PLANTIO | | 250.69 | |

ESCALA: 1: 18.000

CROQUI DE ACESSO

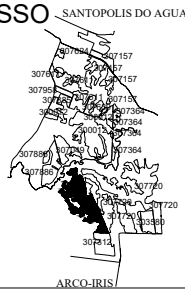


# FAZENDA WR

PROPRIETÁRIO: LUCIANO DE PADUA CINTRA
COMPRADOR: CLEALCO
MUNICÍPIO: ARCO-ÍRIS - SP

DISTÂNCIAS (km):
UNID. I - Asfalto: 20.00 Terra.: 11.50
UNID.I I - Asfalto: 37.00 Terra.: 11.50

COORDENADAS: E(X): 553837.91 N(Y): 7598014.73
LAT: -21°43'13.9302" LONG: -50°28'45.9809"
CLEALCO - AÇÚCAR E ALCOOL S/A - DEPARTAMENTO DE GEOTECNOLOGIA

LEVANTAMENTO VIA:
- SATÉLITE
- GPS / VANT
- GOOGLE

UNIDADE: I
PARTE: A/A
FUNDO AGRÍCOLA: 302953

M:\01-Mapa de safra\Mapas Atualizados\Acionista\Luciano de Padua Cintra\302953 - Fazenda WR (Luciano de Padua Cintra)\302953 - Fazenda WR (Luciano de Padua Cintra).dwg

Bruno Gamboa 15/01/26