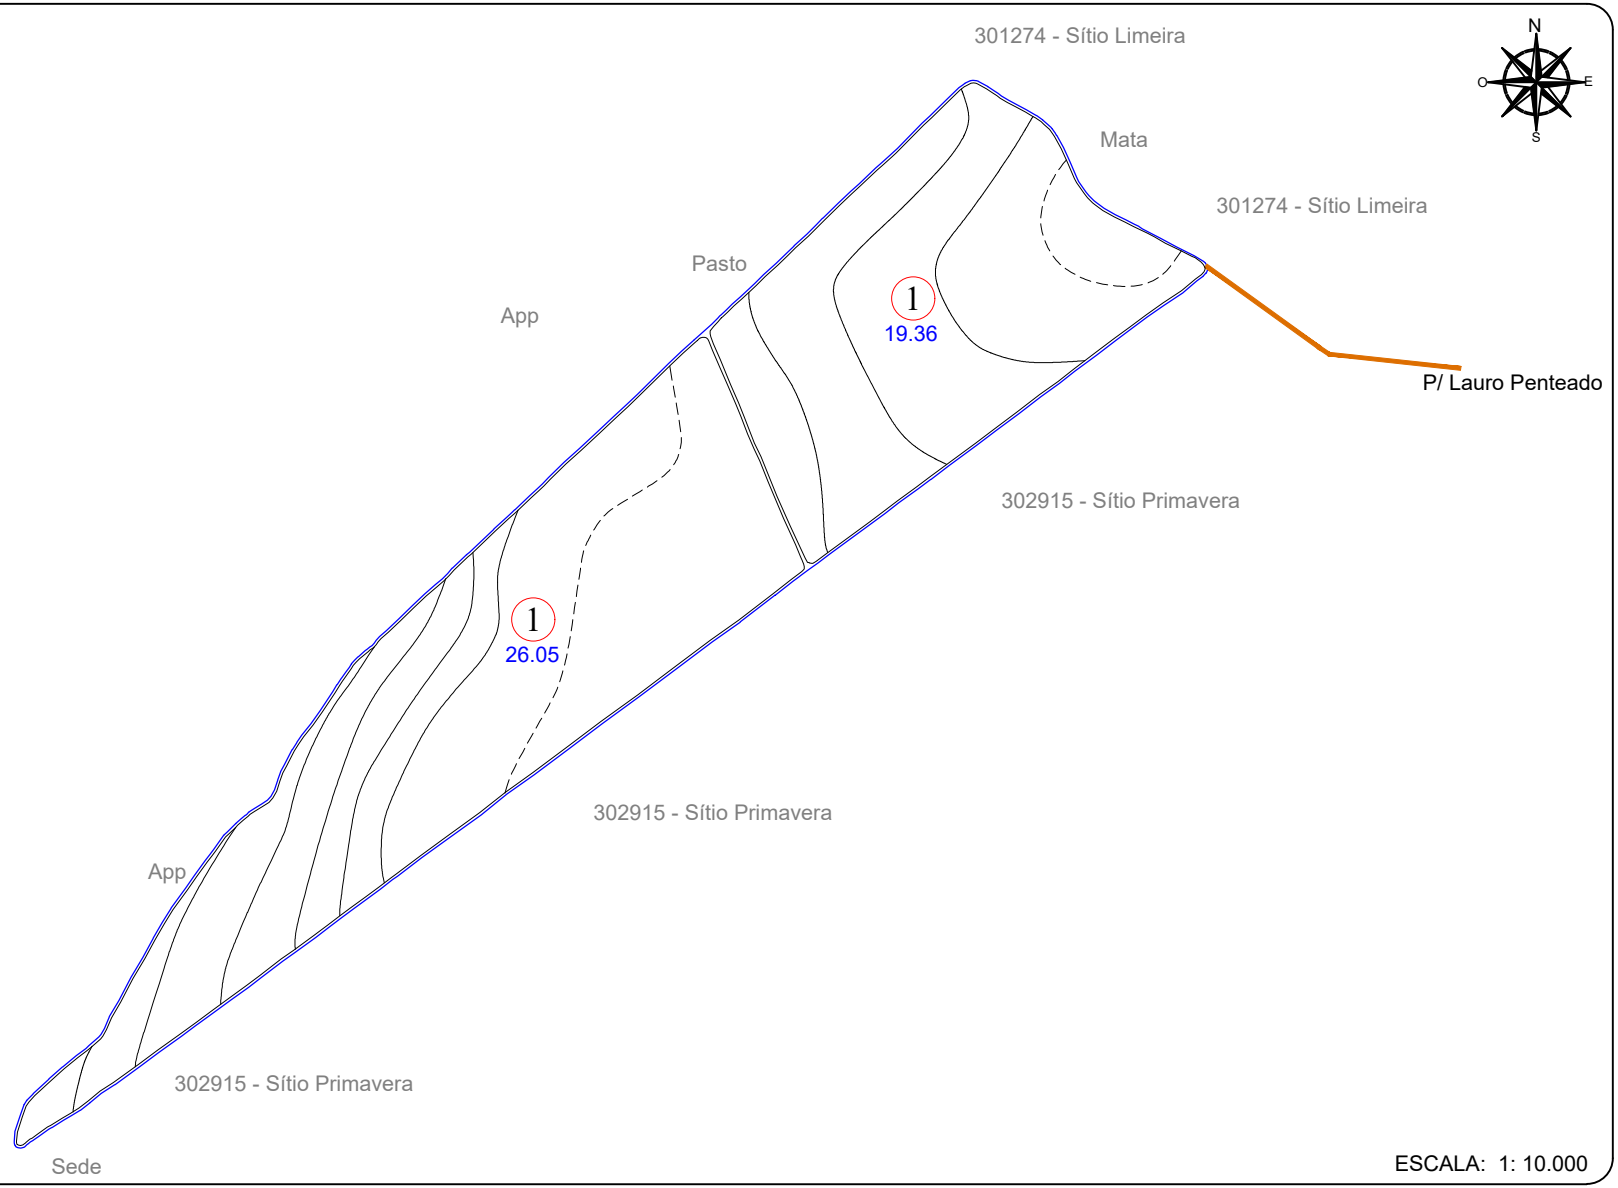


Nº TAL.	DATA PL.	ÁREA (ha)	VARIEDADE
1	04/2026	45.41	RB97 5201 / RB97 5242
TOTAL PLANTIO		45.41	

ÁREAS	(ha)	(%)
PLANTIO	45.41	96.86
CARREADORES	1.47	3.14
OUTROS	0.00	0.00
SUB TOTAL AGRICULTÁVEL	46.88	100.00
AP.P.	0.00	0.00
ÁRVORES	0.00	0.00
OUTROS	0.00	0.00
SUB TOTAL NÃO AGRICULT.	0.00	0.00
ÁREA TOTAL	46.88	100.00

C. NÍVEL: 3963.11 m/l 0.91 ha 1.94 %

ESCALA: 1: 10.000


LEGENDA

- FAZENDA
- TALHÃO
- REDE ELÉTRICA
- TERRAÇO BASE LARGA
- TERRAÇO EMBUTIDO

ESPAÇAMENTO: 1.50 x 1.50
TIRO MÉDIO ESTIMADO: 274.79 m

D.V: 3.07 %

CROQUI DE ACESSO

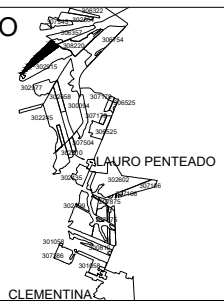

SÍTIO SANTA MARCELINA

PROPRIETÁRIO: ANDRE V. LEMOS DE MELO
COMPRADOR: CLEALCO
MUNICÍPIO: BILAC - SP

DISTÂNCIAS (km):
UNID. I - Asfalto: 11.25 Terra.: 9.40
UNID.I I - Asfalto: 71.25 Terra.: 9.40

COORDENADAS: E(X): 554299.55 N(Y): 7625118.19
LAT: -21°28'32.3489" LONG: -50°28'33.0895"

CLEALCO - AÇÚCAR E ALCOOL S/A - DEPARTAMENTO DE GEOTECNOLOGIA

LEVANTAMENTO VIA:
SATÉLITE
GPS / VANT
GOOGLE

UNIDADE: I
PARTE: A/A
FUNDO AGRÍCOLA: 308098

Bruno Gamboa 11/09/26

M:\01-Mapa de safra\Mapas Atualizados\Acionista\Luciano de Padua Cintra\308098 - Sitio Santa Marcelina (Andre Vasconcelos Lemos De Melo)\308098 - Sitio Santa Marcelina (Andre Vasconcelos Lemos De Melo).dwg