ZONA D.V.	Nº TAL.	DATA PL.	ÁREA (ha)	VARIEDADE
1 8.00 %	1	07/2023	7.80	RB 975033
	2		8.35	
TOTAL PLANTIO			16.15	--------

ÁREAS	(ha)	(%)
PLANTIO	16.15	94.22
CARREADORES	0.99	5.78
OUTROS	0.00	0.00
SUB TOTAL AGRICULTÁVEL	17.14	100.00
AP.P.	0.00	0.00
ÁRVORES	0.00	0.00
OUTROS	0.00	0.00
SUB TOTAL NÃO AGRICULT.	0.00	0.00
ÁREA TOTAL	17.14	100.00

C. NÍVEL:	2622.07 m/l	0.60 ha	3.52 %

LEGENDA

FAZENDA	CONFRONTANTE
TALHÃO	REDE ELÉTRICA
CURVA DE NÍVEL	TRAJETO VAZIO
CARREADOR	TRAJETO CARREGADO

PLANTIO MANUAL - ESPAÇAMENTO: 1.50 X 1.50
TIRO MÉDIO ESTIMADO: 165.00 m

Clealco®
Açúcar, Etanol e Energia

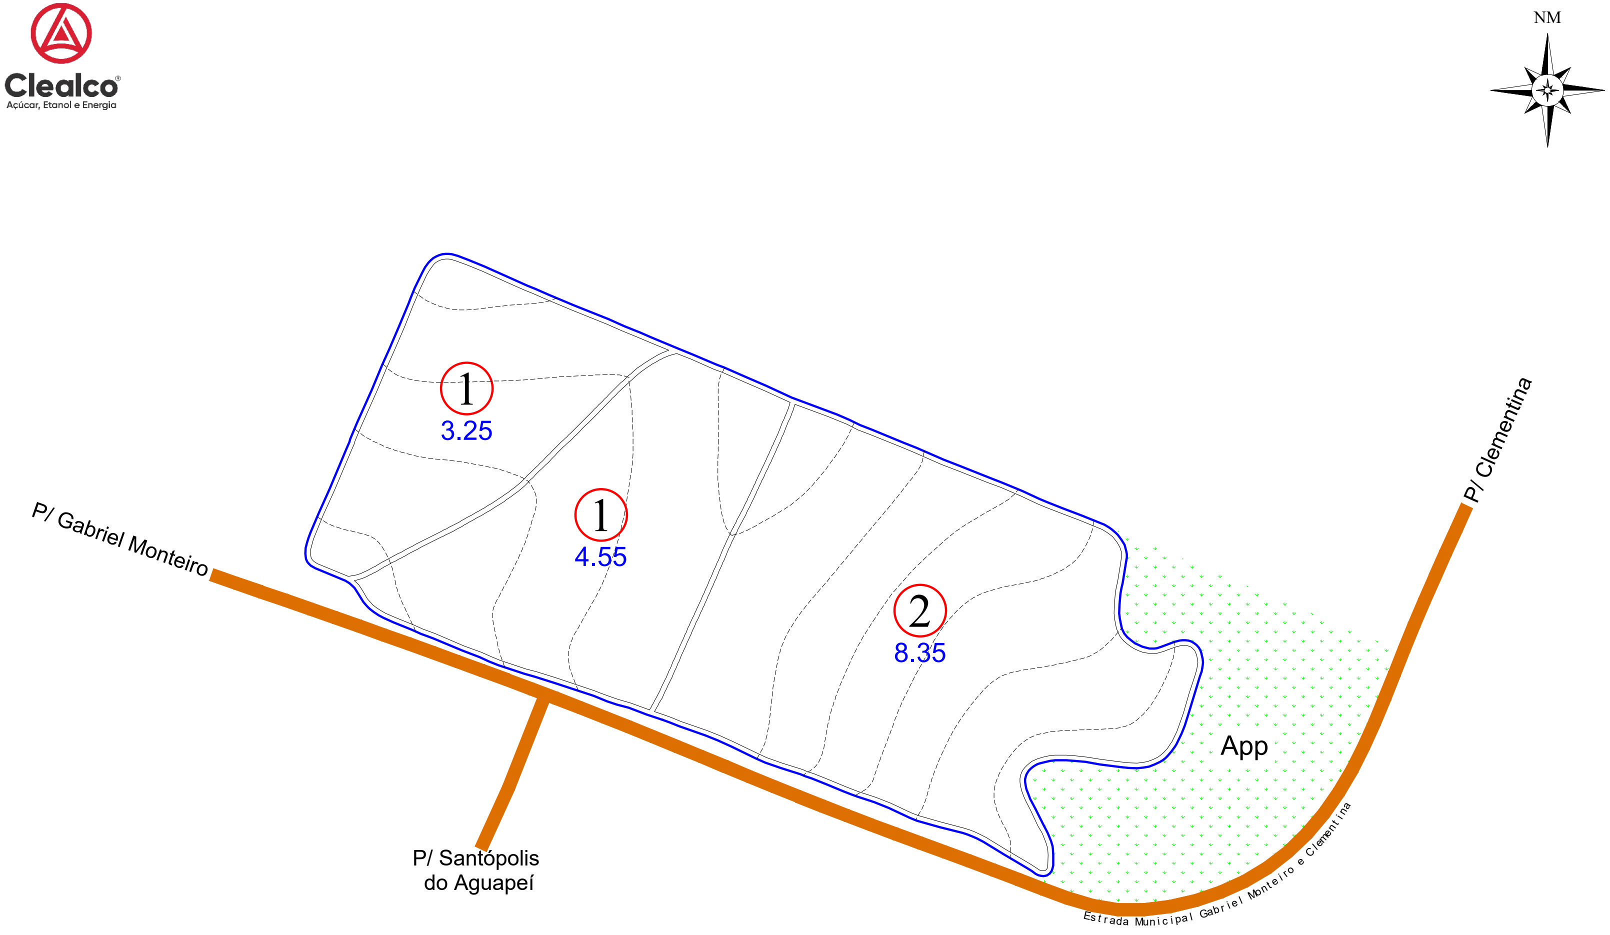

ESCALA: 1: 6.000

CROQUI DE ACESSO

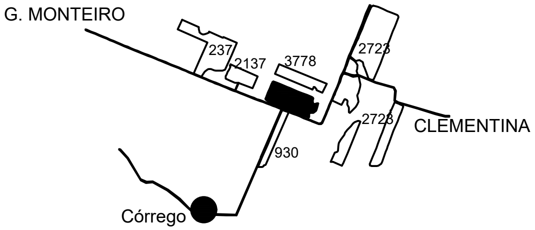

SÍTIO TOMÉ

PROPRIETÁRIO:	MANOEL TOMÉ
COMPRADOR:	CLEALCO S/A
MUNICÍPIO:	CLEMENTINA

DISTÂNCIAS (km):

UNID. I -	Asfalto:	05.50	Terra.:	07.00
UNID.I I -	Asfalto:	68.00	Terra.:	07.00
UNID. III -	Asfalto:	44.00	Terra.:	07.00

COORDENADAS: E(X):	553799.74	N(Y):	7615755.44
LAT:	-21°33'36.9265"	LONG:	-50°28'49.3748"

CLEALCO - AÇÚCAR E ALCOOL S/A - DEPARTAMENTO DE TOPOGRAFIA

UNIDADE:
I

PARTE:
A/A

FUNDO AGRÍCOLA:
300022

M:\01-Mapa de safra\Mapas Atualizados\Acionista\Manoel Tomé\300022 - Sítio Tomé (Manoel Tomé)\300022 - Sítio Tomé (Manoel Tomé).dwg

Fernanda Bezerra 26/07/23