
Clealco
Açúcar, Etanol e Energia

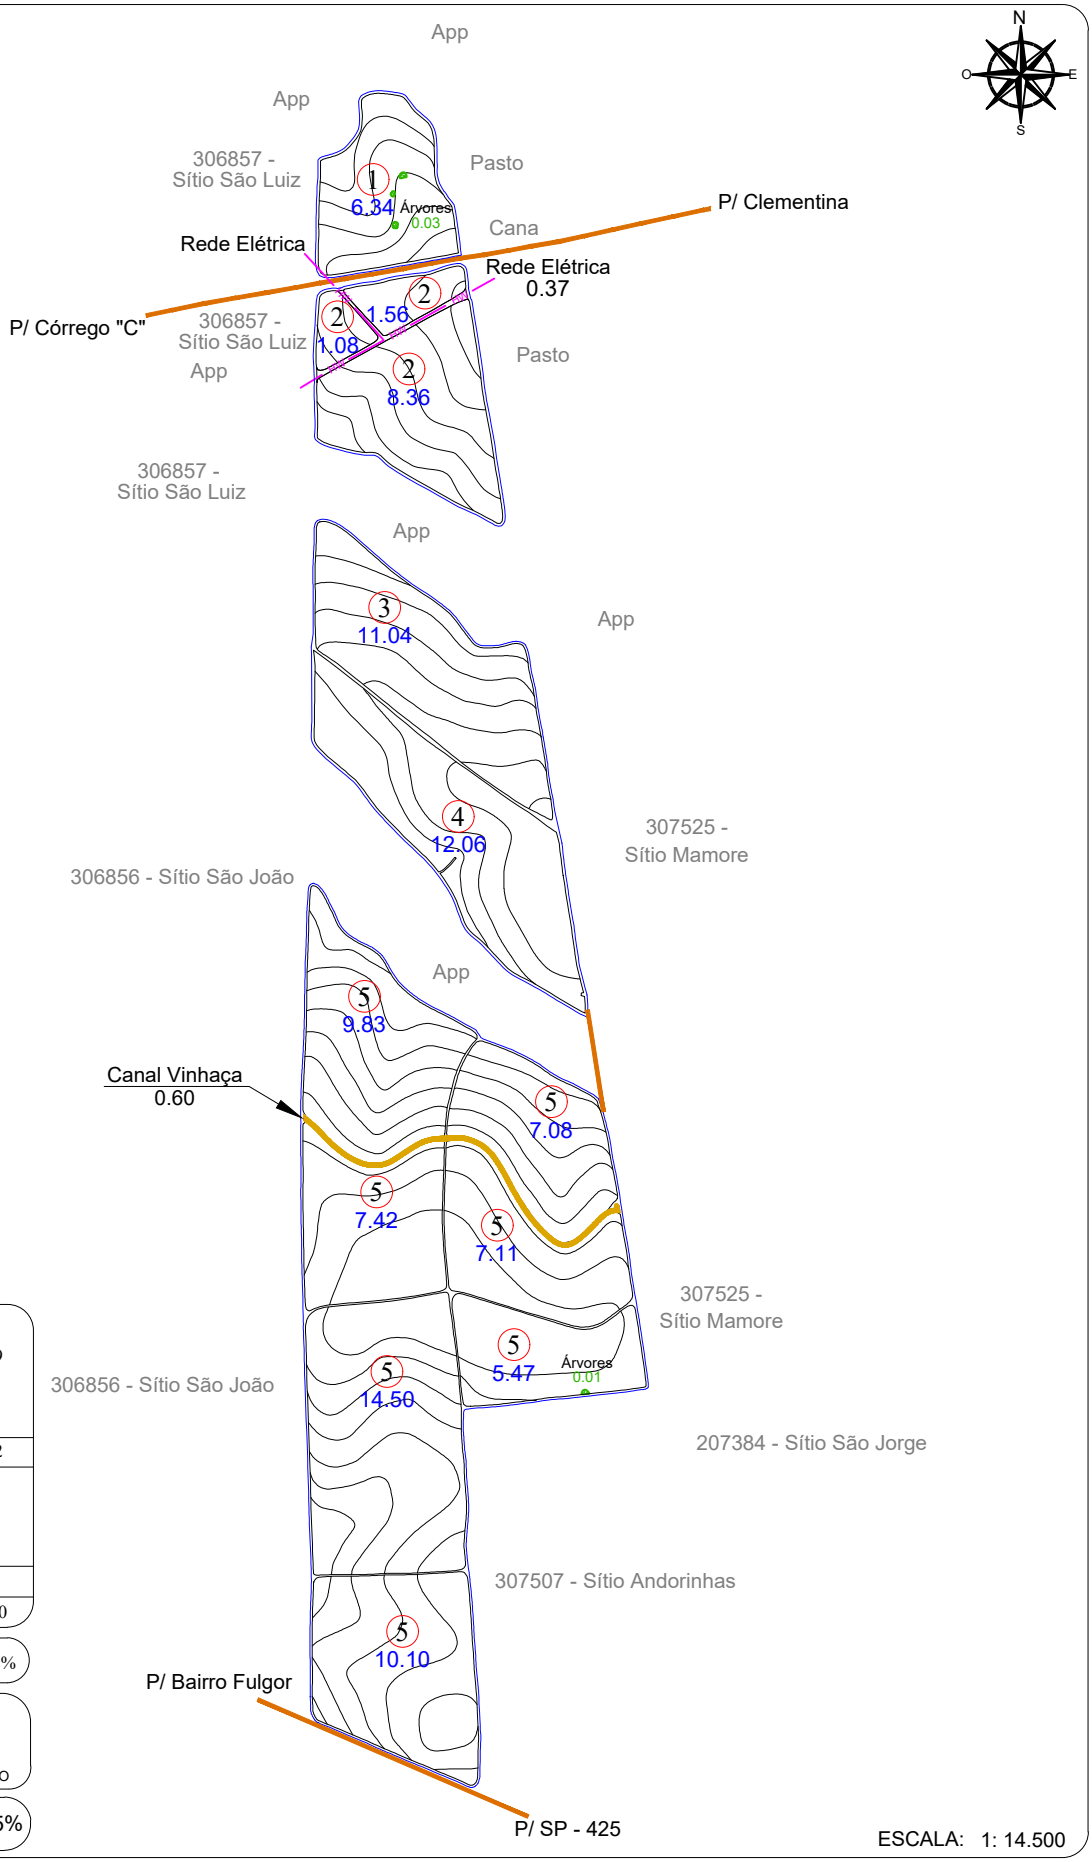

Nº TAL.	DATA PL.	ÁREA (ha)	VARIEDADE
1	06/2023	6.34	RB 975033
2	04/2025	11.00	RB97 5201
3	06/2024	11.04	RB 975033
4	05/2021	12.06	RB 988082
5	06/2024	61.51	RB 975033
TOTAL PLANTIO		101.95	

ÁREAS	(ha)	(%)
PLANTIO	101.95	94.59
CARREADORES	4.82	4.47
OUTROS	0.60	0.56
SUB TOTAL AGRICULTÁVEL	107.37	99.62
AP.P.	0.00	0.00
ÁRVORES	0.04	0.04
OUTROS	0.37	0.34
SUB TOTAL NÃO AGRICULT.	0.41	0.38
ÁREA TOTAL	107.78	100.00

C. NÍVEL: 19003.54 m/l 4.37 ha 4.06 %


LEGENDA

- FAZENDA
- TALHÃO
- REDE ELÉTRICA
- TERRAÇO BASE LARGA
- TERRAÇO EMBUTIDO
- (P.O.A) PATIO DE OPERAÇÃO

ESPAÇAMENTO: 1.50 x 1.50
TIRO MÉDIO ESTIMADO: 000.00 m
D.V: 5.55%

ESCALA: 1: 14.500

CROQUI DE ACESSO

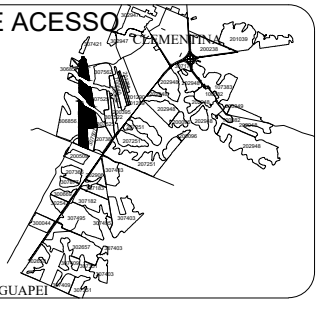

SÍTIO DOIS IRMÃOS

PROPRIETÁRIO: MANOEL TOMÉ
COMPRADOR: CLEALCO
MUNICÍPIO: CLEMENTINA - SP

DISTÂNCIAS (km):
UNID. I - Asfalto: 6.50 Terra.: 1.50
UNID.I I - Asfalto: 53.00 Terra.: 1.50

COORDENADAS: E(X): 554651.31 N(Y): 7612442.24
LAT: -21°35'24.5942" LONG: -50°28'19.3765"

CLEALCO - AÇÚCAR E ALCOOL S/A - DEPARTAMENTO DE GEOTECNOLOGIA

LEVANTAMENTO VIA:
- SATÉLITE
- GPS / VANT
- GOOGLE

UNIDADE: I
PARTE: A/A
FUNDO AGRÍCOLA: 300162

M:\01-Mapa de safra\Mapas Atualizados\Acionista\Manoel Tomé\300162 - Sítio Dois Irmãos (Manoel Tomé)\300162 - Sítio Dois Irmãos (Manoel Tomé).dwg

Bruno Gamboa 24/11/25