
Clealco
Açúcar, Etanol e Energia

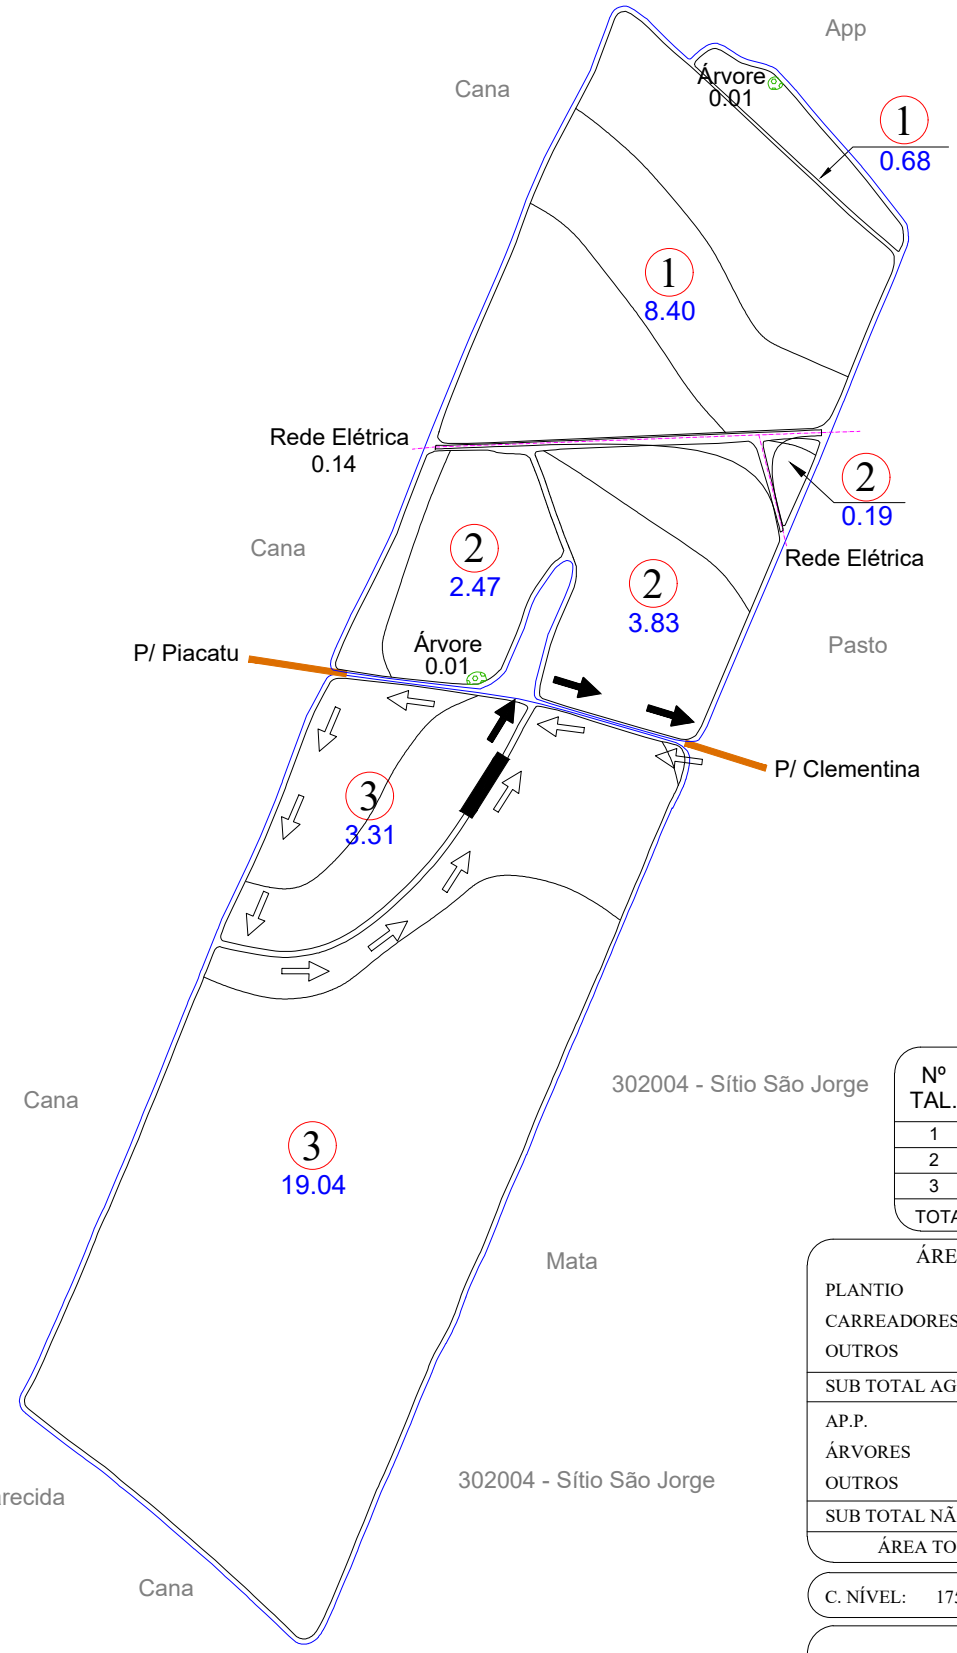

Nº TAL.	DATA PL.	ÁREA (ha)	VARIEDADE
1	04/2026	9.08	RB97 5201
2		6.49	
3		22.35	
TOTAL PLANTIO		37.92	

ÁREAS	(ha)	(%)
PLANTIO	37.92	94.48
CARREADORES	2.05	5.12
OUTROS	0.00	0.00
SUB TOTAL AGRICULTÁVEL	39.97	99.60
AP.P.	0.00	0.00
ÁRVORES	0.02	0.05
OUTROS	0.14	0.35
SUB TOTAL NÃO AGRICULT.	0.16	0.40
ÁREA TOTAL	40.13	100.00

C. NÍVEL: 1755.70 m/l 0.40 ha 1.01 %


LEGENDA

- FAZENDA
- TALHÃO
- REDE ELÉTRICA
- TERRAÇO BASE LARGA
- TERRAÇO EMBUTIDO
- (P.O.A) PATIO DE OPERAÇÃO

ESPAÇAMENTO: 1.50 x 1.50
TIRO MÉDIO ESTIMADO: 199.12 m
D.V: 3.49 %

ESCALA: 1: 6.500

CROQUI DE ACESSO

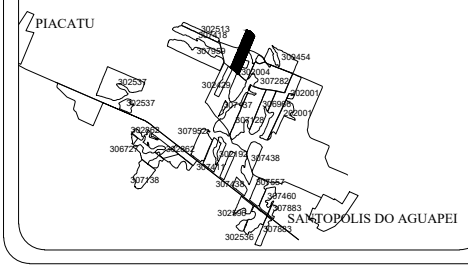

SÍTIO NOSSA SENHORA DA APARECIDA

PROPRIETÁRIO: MANOEL TOMÉ
COMPRADOR: CLEALCO
MUNICÍPIO: CLEMENTINA - SP

DISTÂNCIAS (km):
UNID. I - Asfalto: 5.50 Terra.: 7.50
UNID.I I - Asfalto: 52.00 Terra.: 7.50

COORDENADAS: E(X): 549197.89 N(Y): 7612734.77
LAT: -21°35'15.6512" LONG: -50°31'29.0574"

CLEALCO - AÇÚCAR E ALCOOL S/A - DEPARTAMENTO DE GEOTECNOLOGIA

LEVANTAMENTO VIA:
- SATÉLITE
- GPS / VANT
- GOOGLE

UNIDADE: I
PARTE: A/A
FUNDO AGRÍCOLA: 300534

M:\01-Mapa de safra\Mapas Atualizados\Acionista\Manoel Tomé\300534 - Sitio Nossa Senhora Aparecida (Manoel Tomé)\300534 - Sitio Nossa Senhora Aparecida (Manoel Tomé).dwg

Bruno Gamboa 17/09/26