
Clealco
Açúcar, Etanol e Energia

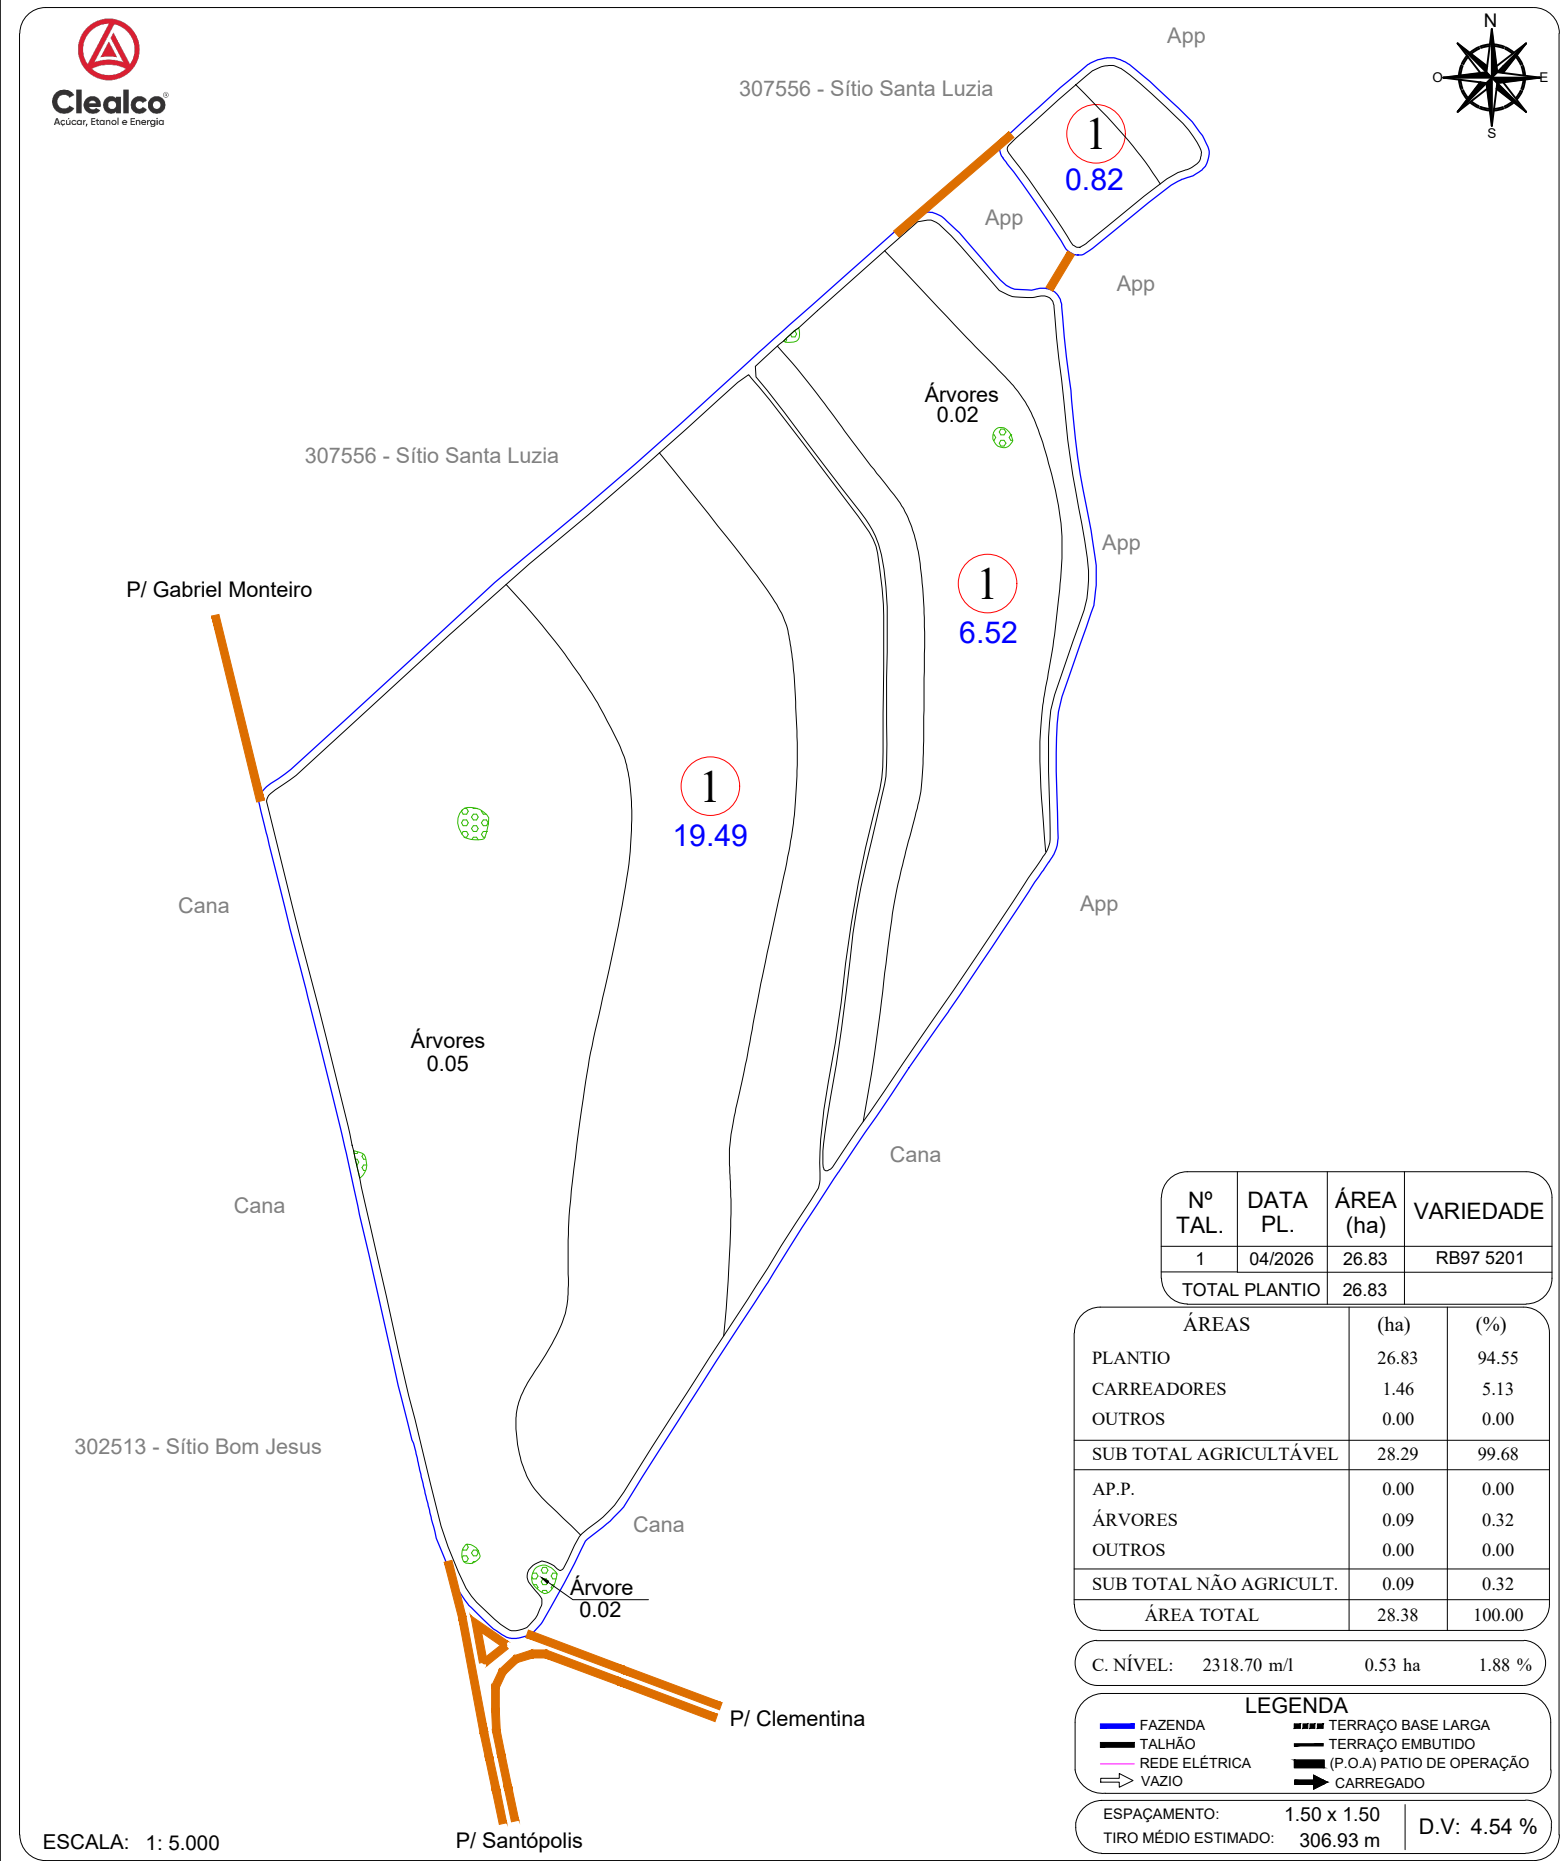

ESCALA: 1: 5.000

Nº TAL.	DATA PL.	ÁREA (ha)	VARIEDADE
1	04/2026	26.83	RB97 5201
TOTAL PLANTIO		26.83	

ÁREAS	(ha)	(%)
PLANTIO	26.83	94.55
CARREADORES	1.46	5.13
OUTROS	0.00	0.00
SUB TOTAL AGRICULTÁVEL	28.29	99.68
AP.P.	0.00	0.00
ÁRVORES	0.09	0.32
OUTROS	0.00	0.00
SUB TOTAL NÃO AGRICULT.	0.09	0.32
ÁREA TOTAL	28.38	100.00


C. NÍVEL: 2318.70 m/l 0.53 ha 1.88 %

LEGENDA

- FAZENDA
- TALHÃO
- REDE ELÉTRICA
- VAZIO
- TERRAÇO BASE LARGA
- TERRAÇO EMBUTIDO
- (P.O.A) PATIO DE OPERAÇÃO
- CARREGADO

ESPAÇAMENTO: 1.50 x 1.50
TIRO MÉDIO ESTIMADO: 306.93 m
D.V: 4.54 %

CROQUI DE ACESSO

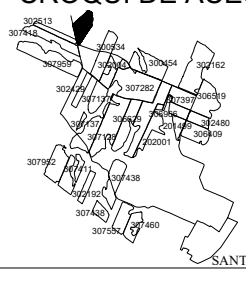

SÍTIO SÃO JOSÉ III

PROPRIETÁRIO: MANOEL TOMÉ
COMPRADOR: CLEALCO
MUNICÍPIO: CLEMENTINA - SP

DISTÂNCIAS (km):
UNID. I - Asfalto: 06.50 Terra.: 09.50
UNID.I I - Asfalto: 53.00 Terra.: 09.50

COORDENADAS: E(X): 548691.77 N(Y): 7613488.73
LAT: -21°34'51.1786" LONG: -50°31'46.7373"

CLEALCO - AÇÚCAR E ALCOOL S/A - DEPARTAMENTO DE GEOTECNOLOGIA

LEVANTAMENTO VIA:
SATÉLITE
GPS / VANT
GOOGLE

UNIDADE: I
PARTE: A/A
FUNDO AGRÍCOLA: 300811

M:\01-Mapa de safra\Mapas Atualizados\Acionista\Manoel Tomé\300811 - Sítio São José III (Manoel Tomé)\300811 - Sítio São José III (Manoel Tomé).dwg

Bruno Gamboa 09/09/26