
Clealco
Açúcar, Etanol e Energia

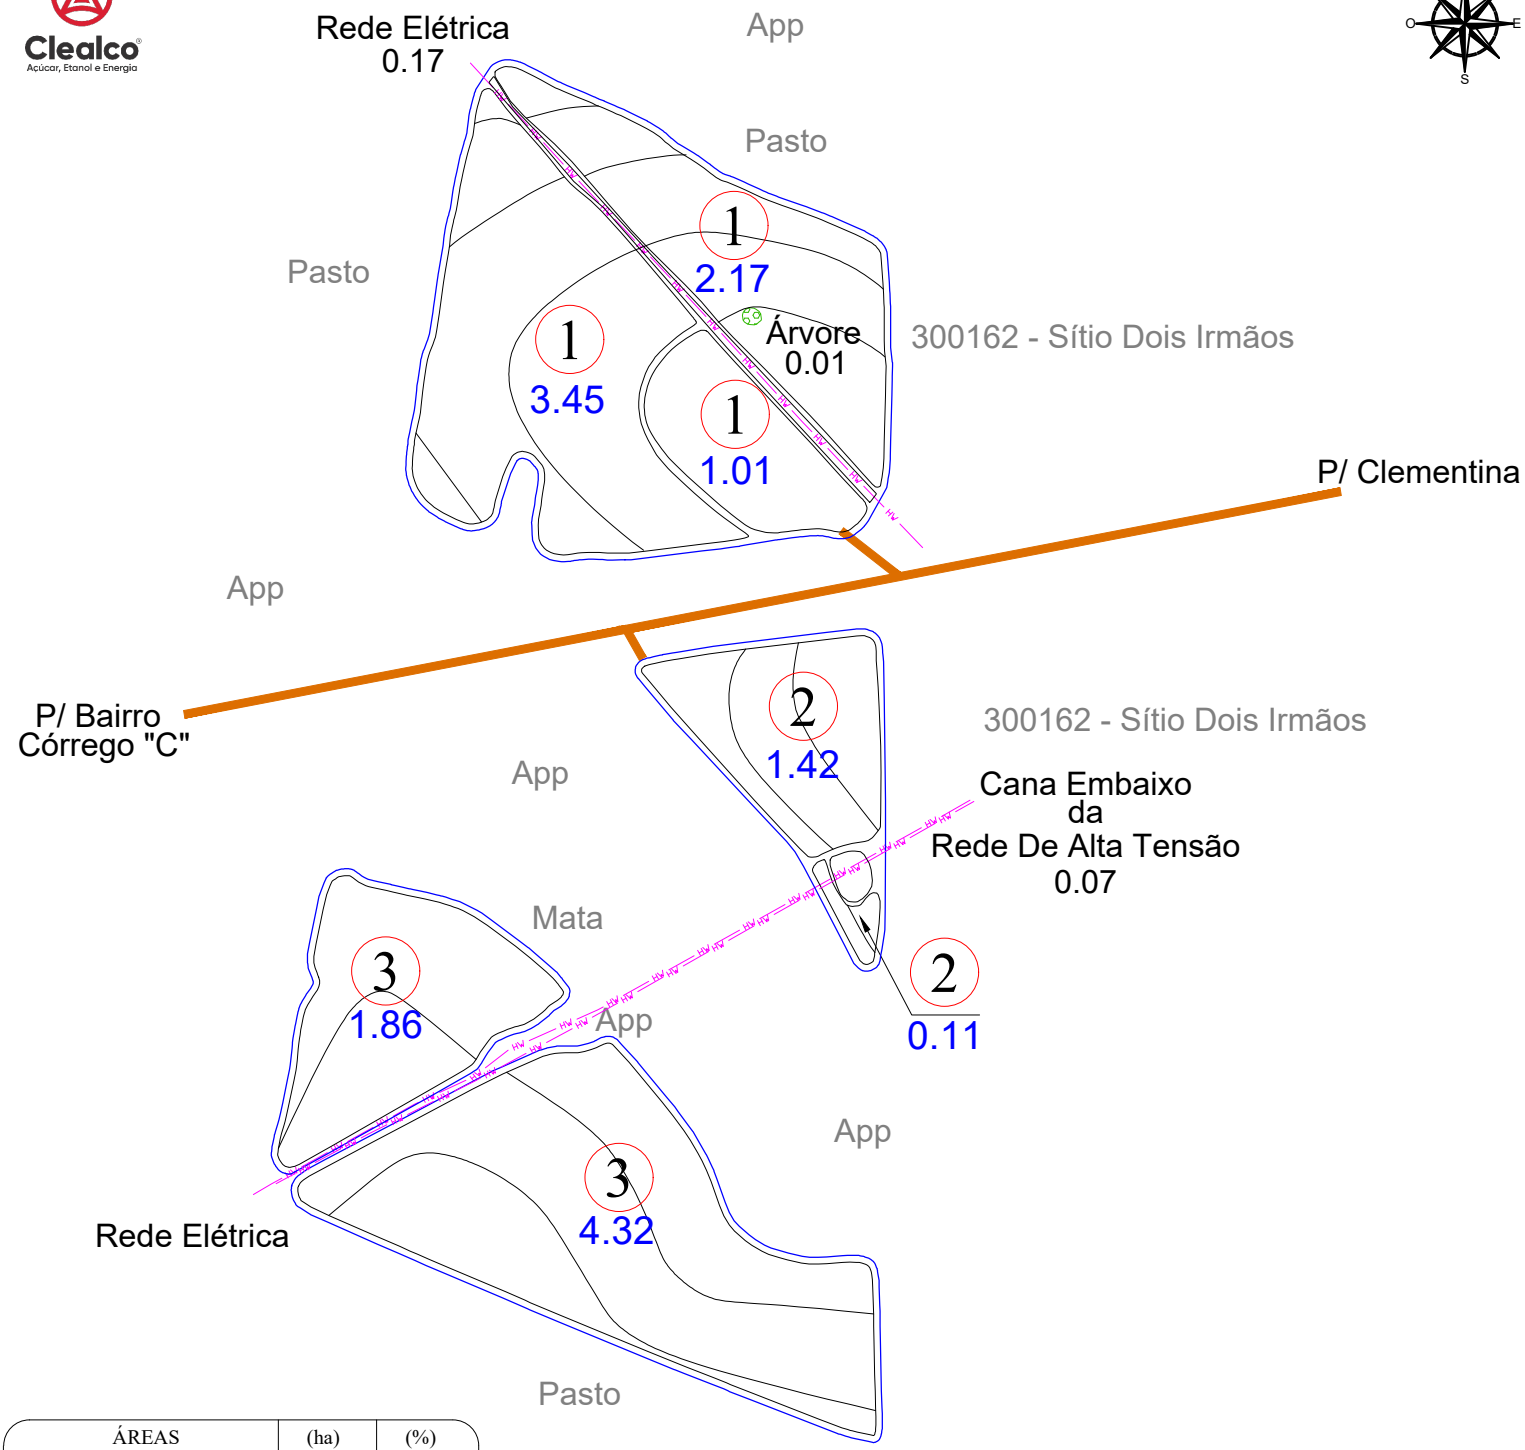

ÁREAS	(ha)	(%)
PLANTIO	14.34	88.02
CARREADORES	1.70	10.45
OUTROS	0.00	0.00
SUB TOTAL AGRICULTÁVEL	16.04	98.47
AP.P.	0.00	0.00
ÁRVORES	0.01	0.06
OUTROS	0.24	1.47
SUB TOTAL NÃO AGRICULT.	0.25	1.53
ÁREA TOTAL	16.29	100.00

C. NÍVEL: 2129.40 m/l 0.49 ha 3.01 %

Nº TAL.	DATA PL.	ÁREA (ha)	VARIEDADE
1	04/2026	6.63	RB97 5201
2		1.53	RB12 7825
3		6.18	
TOTAL PLANTIO		14.34	


LEGENDA

- FAZENDA
- TALHÃO
- REDE ELÉTRICA
- TERRAÇO BASE LARGA
- TERRAÇO EMBUTIDO
- (P.O.A) PATIO DE OPERAÇÃO

ESPAÇAMENTO: 1.50 x 1.50
TIRO MÉDIO ESTIMADO: 108.17 m
D.V: 6.46 %

ESCALA: 1: 5.000

CROQUI DE ACESSO

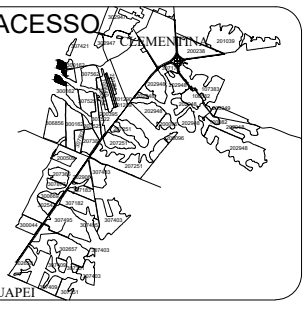

SÍTIO SÃO LUIZ

PROPRIETÁRIO: MANOEL TOME
COMPRADOR: CLEALCO
MUNICÍPIO: CLEMENTINA - SP

DISTÂNCIAS (km):
UNID. I - Asfalto: 3.00 Terra.: 3.00
UNID.I I - Asfalto: 47.00 Terra.: 4.50

COORDENADAS: E(X): 554308.10 N(Y): 7614264.91
LAT: -21°34'25.3504" LONG: -50°28'31.5254"

CLEALCO - AÇÚCAR E ALCOOL S/A - DEPARTAMENTO DE GEOTECNOLOGIA

LEVANTAMENTO VIA:
SATÉLITE
GPS / VANT
GOOGLE

UNIDADE: I
PARTE: A/A
FUNDO AGRÍCOLA: 302439

M:\01-Mapa de safra\Mapas Atualizados\Acionista\Manoel Tome\302439 - Sitio São Luiz (Manoel Tome)\302439 - Sitio São Luiz (Manoel Tome).dwg

Bruno Gamboa 18/09/26