
Clealco
Açúcar, Etanol e Energia

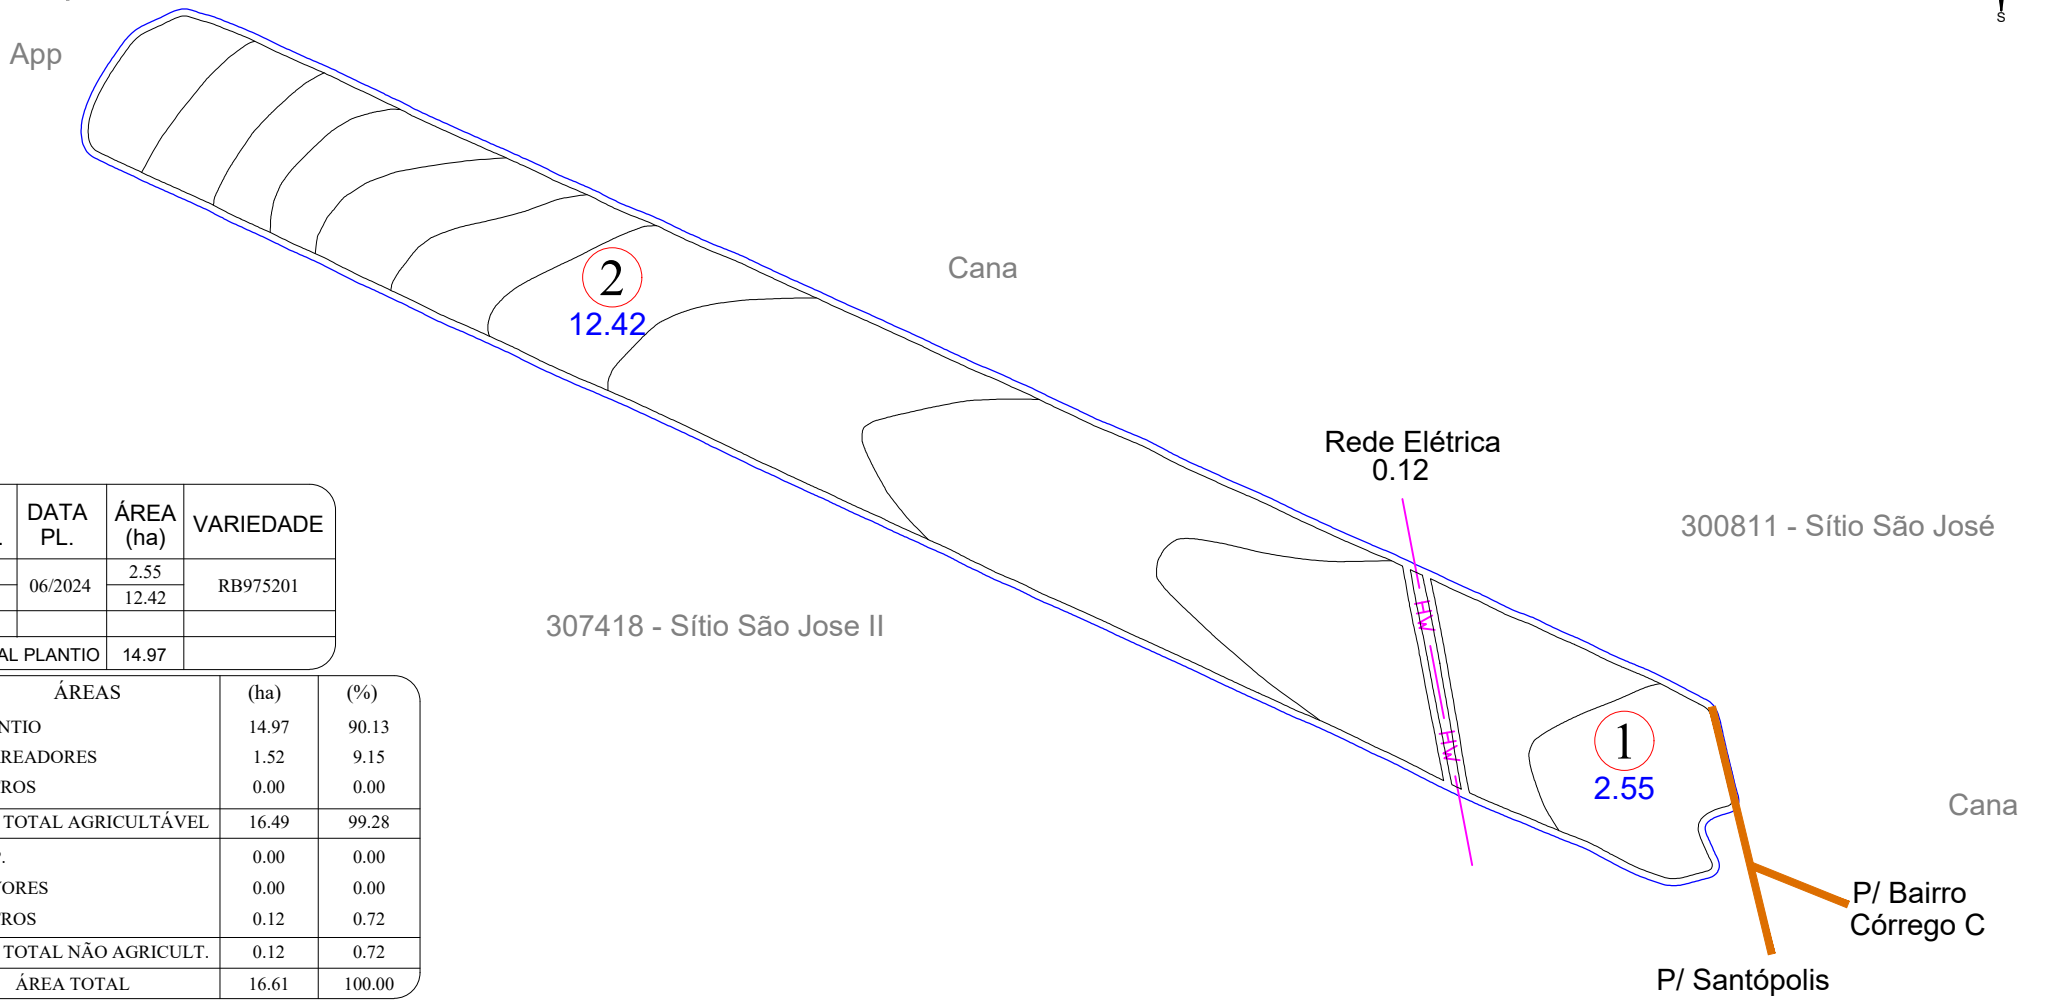

Nº TAL.	DATA PL.	ÁREA (ha)	VARIEDADE
1	06/2024	2.55	RB975201
2		12.42	
TOTAL PLANTIO		14.97	

ÁREAS	(ha)	(%)
PLANTIO	14.97	90.13
CARREADORES	1.52	9.15
OUTROS	0.00	0.00
SUB TOTAL AGRICULTÁVEL	16.49	99.28
AP.P.	0.00	0.00
ÁRVORES	0.00	0.00
OUTROS	0.12	0.72
SUB TOTAL NÃO AGRICULT.	0.12	0.72
ÁREA TOTAL	16.61	100.00


C. NÍVEL:	1784.75 m/l	0.41 ha	2.47 %

ESCALA: 1: 5.500

LEGENDA
- FAZENDA
- TALHÃO
- REDE ELÉTRICA
- TERRAÇO BASE LARGA
- TERRAÇO EMBUTIDO

ESPAÇAMENTO: 1.50 x 1.50
TIRO MÉDIO ESTIMADO: 115.91 m
D.V: 4.66 %

CROQUI DE ACESSO

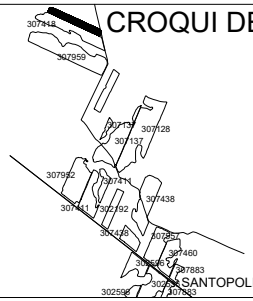

SÍTIO BOM JESUS

PROPRIETÁRIO: JOSÉ FERNANDES GUIMARÃES
COMPRADOR: CLEALCO
MUNICÍPIO: CLEMENTINA - SP

DISTÂNCIAS (km):
UNID. I - Asfalto: 6.50 Terra.: 8.50
UNID.I I - Asfalto: 53.00 Terra.: 8.50

COORDENADAS: E(X): 547531.06 N(Y): 7612847.54
LAT: -21°35'12.1462" LONG: -50°32'27.0342"
CLEALCO - AÇÚCAR E ALCOOL S/A - DEPARTAMENTO DE GEOTECNOLOGIA

LEVANTAMENTO VIA:
- SATÉLITE
- GPS / VANT
- GOOGLE

UNIDADE: I
PARTE: A/A
FUNDO AGRÍCOLA: 302513

M:\01-Mapa de safra\Mapas Atualizados\Acionista\Manoel Tome\302513 - Sitio Bon Jesus (José Fernandes Guimarães)\302513 - Sitio Bon Jesus (José Fernandes Guimarães).dwg

Bruno Gamboa 31/08/26