ZONA DV	CLA	Nº TAL.	DATA PL.	ÁREA (ha)	VAR.
1 4.60 %	SR	121	05/2021	3.41	RB 988082
		221		26.14	
		321		28.22	
		421		30.72	
TOTAL PLANTIO				88.49	--------


ÁREAS	(ha)	(%)
PLANTIO	88.49	96.45
CARREADORES	3.17	3.45
OUTROS	-	-
SUB TOTAL AGRICULTÁVEL	91.66	--------
VÁRZEA	-	-
ÁRVORES	0.09	0.10
OUTROS	-	-
SUB TOTAL NÃO AGRICULT.	0.09	--------
ÁREA TOTAL	91.75	100.00

C. NÍVEL:13847.49 m/l 3.18 ha 3.60 %


LEGENDA

- FAZENDA
- TALHÃO
- CURVA DE NÍVEL
- CARREADOR
- CONFRONTANTE
- REDE ELÉTRICA
- TRAJETO VAZIO
- TRAJETO CARREGADO

PLANTIO MANUAL - ESPAÇAMENTO: 1.50 x 1.50

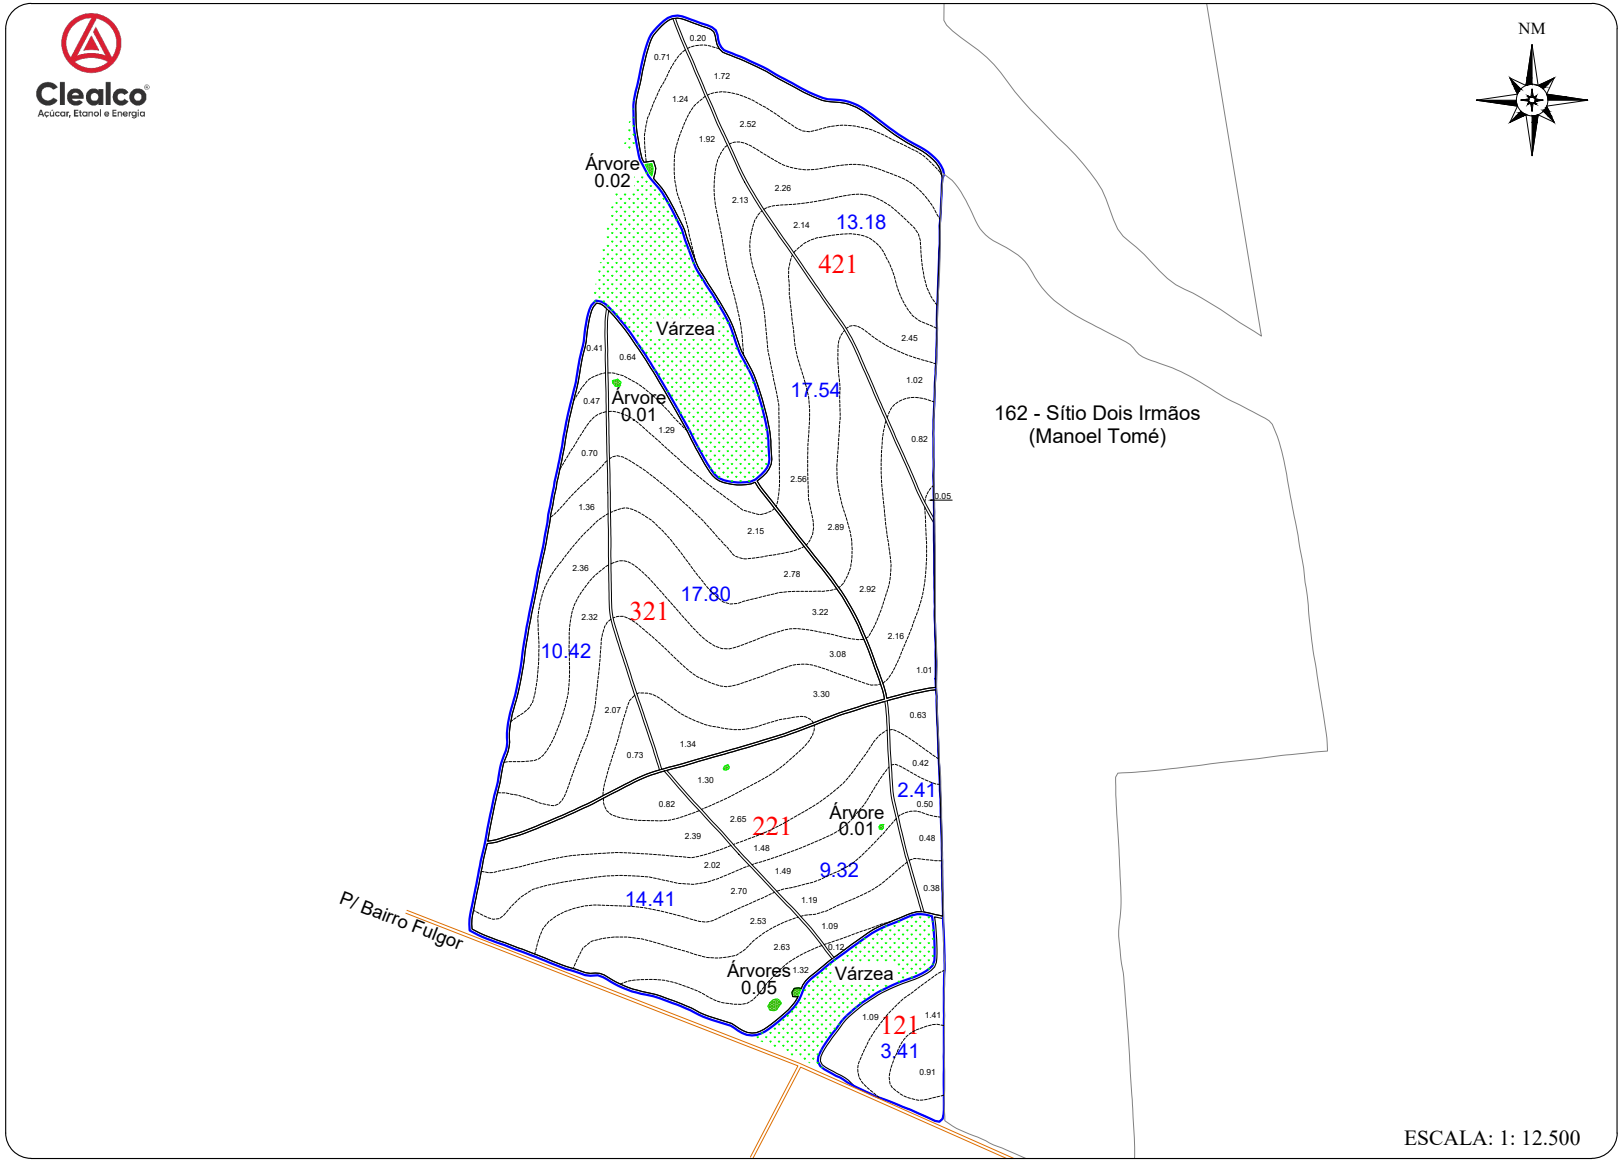

CROQUI DE ACESSO

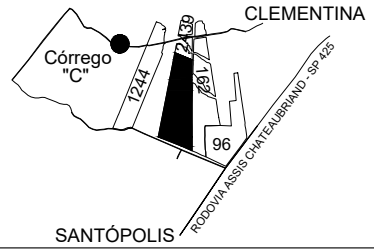

SÍTIO SÃO JOÃO

PROPRIETÁRIO: RAFAEL YUKIO R. TIDA
ARRENDATÁRIO: MANOEL TOMÉ
MUNICÍPIO: CLEMENTINA

DISTÂNCIAS (km):
UNID. I - Asfalto: 6.50 Terra.: 2.50
UNID.I I - Asfalto: 53.00 Terra.: 2.50
UNID. III -Asfalto: 38.00 Terra.: 2.50

COORDENADAS: E(X): 554096 N(Y): 7612777
LAT: 21° 35' 13,76735" LONG: 50° 28' 38,72698"

CLEALCO - AÇÚCAR E ALCOOL S/A - DEPARTAMENTO DE TOPOGRAFIA

UNIDADE: I

PARTE: A/A

FUNDO AGRÍCOLA: 306856

M:\01-Mapa de safra\Mapas Atualizados\Acionista\Manoel Tomé\306856 - Sítio São João (Manoel Tomé)\306856 - Sítio São João (Manoel Tomé).dwg

Fernanda Bezerra 09/06/21