ZONA D.V.	Nº TAL.	DATA PL.	ÁREA (ha)	VAR.
1 3.83 %	1	04/2022	0.81	RB 975242
	2		24.94	
TOTAL PLANTIO			25.75	--------


ÁREAS	(ha)	(%)
PLANTIO	25.75	93.33
CARREADORES	1.45	5.26
OUTROS	0.00	0.00
SUB TOTAL AGRICULTÁVEL	27.20	98.59
AP.P.	0.00	0.00
ÁRVORES	0.00	0.00
OUTROS	0.39	1.41
SUB TOTAL NÃO AGRICULT.	0.39	1.41
ÁREA TOTAL	27.59	100.00

C. NÍVEL: 3661.74 m/l 0.84 ha 3.05 %

LEGENDA


- FAZENDA
- TALHÃO
- CURVA DE NÍVEL
- CARREADOR
- CONFRONTANTE
- REDE ELÉTRICA
- TRAJETO VAZIO
- TRAJETO CARREGADO

PLANTIO MANUAL - ESPAÇAMENTO: 1.50 X 1.50
TIRO MÉDIO ESTIMADO: 377.59m

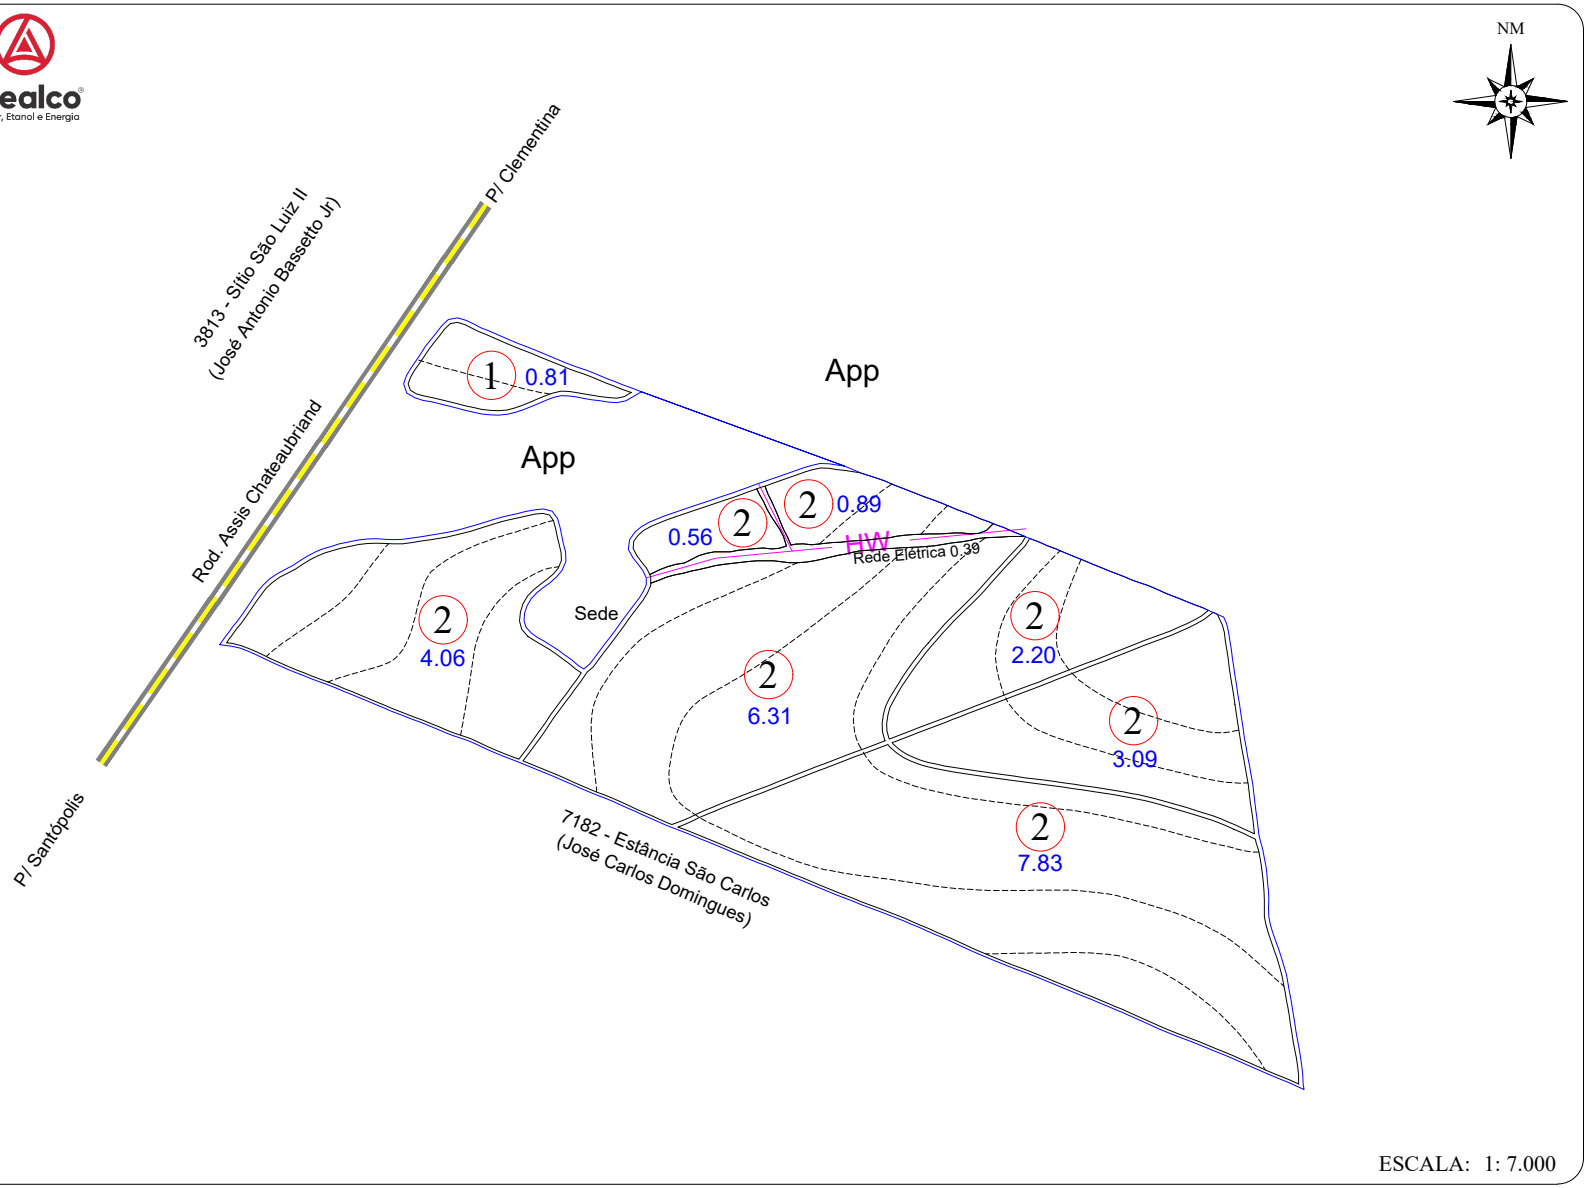

ESCALA: 1: 7.000

CROQUI DE ACESSO

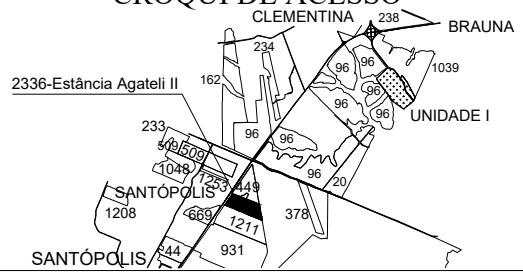

ESTÂNCIA AGATELI II

PROPRIETÁRIO: PAULO CESAR AGATELI
ARRENDATÁRIO: MANOEL TOMÉ
MUNICÍPIO: CLEMENTINA - SP

DISTÂNCIAS (km):
UNID. I - Asfalto: 8.00 Terra.: 0.50
UNID.I I - Asfalto: 50.00 Terra.: 0.50
UNID. III -Asfalto: 50.00 Terra.: 0.50

COORDENADAS: E(X): 554524.30 N(Y): 7610184.16
LAT: -21°36'38.0515" LONG: -50°28'23.5273"

CLEALCO - AÇÚCAR E ALCOOL S/A - DEPARTAMENTO DE TOPOGRAFIA

UNIDADE: I
PARTE: A/A
FUNDO AGRÍCOLA: 307183