ZONA D.V.	Nº TAL.	DATA PL.	ÁREA (ha)	VAR.
1 4.27%	1	05/2022	24.37	RB 975242
	2		15.52	
TOTAL PLANTIO			39.89	--------


ÁREAS	(ha)	(%)
PLANTIO	39.89	93.89
CARREADORES	1.00	2.34
OUTROS	0.00	0.00
SUB TOTAL AGRICULTÁVEL	40.89	96.23
AP.P.	0.00	0.00
ÁRVORES	0.00	0.00
OUTROS	1.60	3.77
SUB TOTAL NÃO AGRICULT.	1.60	3.77
ÁREA TOTAL	42.49	100.00

C. NÍVEL: 4578.50 m/l 1.05 ha 2.48 %


LEGENDA

- FAZENDA
- TALHÃO
- CURVA DE NÍVEL
- CARREADOR
- CONFRONTANTE
- REDE ELÉTRICA
- TRAJETO VAZIO
- TRAJETO CARREGADO

PLANTIO MANUAL - ESPAÇAMENTO: 1.50 X 1.50
TIRO MÉDIO ESTIMADO: 447.77m

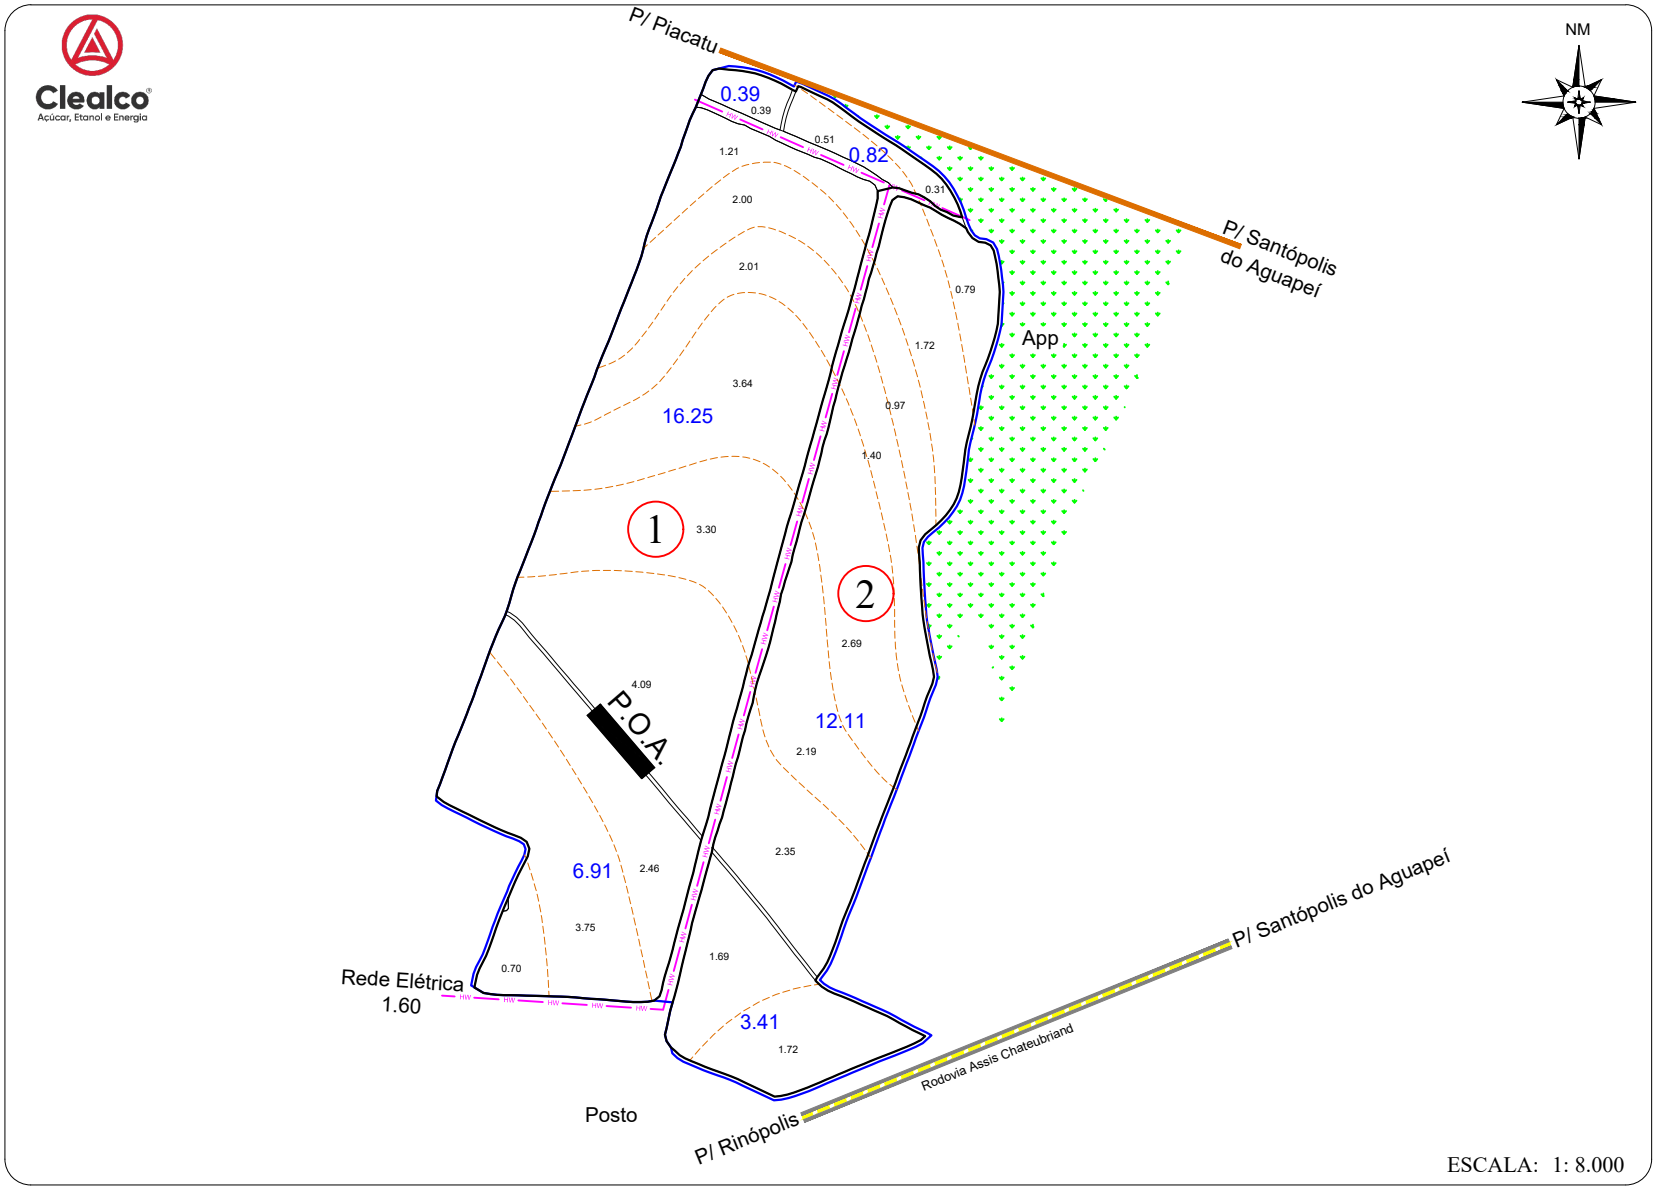

CROQUI DE ACESSO

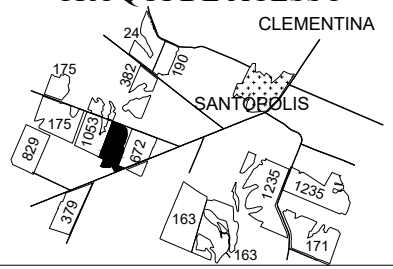

SÍTIO SANTO EXPEDITO

PROPRIETÁRIO: JEFFERSON PINHEIRO TOMÉ
COMPRADOR: CLEALCO S/A
MUNICÍPIO: SANTÓPOLIS DO AGUAPEI

DISTÂNCIAS (km):
UNID. I - Asfalto: 15.50 Terra.: 2.00
UNID.I I - Asfalto: 50.20 Terra.: 1.50
UNID. III -Asfalto: 57.00 Terra.: 3.50

COORDENADAS: E(X): 548289.07 N(Y): 7605899.77
LAT: -21°38'58.0480" LONG: -50°31'59.9489"

CLEALCO - AÇÚCAR E ALCOOL S/A - DEPARTAMENTO DE TOPOGRAFIA

UNIDADE: I
PARTE: A/A
FUNDO AGRÍCOLA: 307417