ZONA	Nº TAL.	DATA PL.	ÁREA (ha)	VAR.
999	1	04/2021	41.59	RB 86 7515
	2		5.23	
TOTAL PLANTIO			46.82	--------

ÁREAS	(ha)	(%)
PLANTIO	46.82	94.61
CARREADORES	2.65	5.35
OUTROS	0.00	0.00
SUB TOTAL AGRICULTÁVEL	49.47	99.96
AP.P.	0.00	0.00
MATA	0.02	0.04
OUTROS	0.00	0.00
SUB TOTAL NÃO AGRICULT.	0.02	0.04
ÁREA TOTAL	49.49	100.00


C. NÍVEL: 6549.13 m/l 1.51 ha 3.04 %

LEGENDA

- FAZENDA
- TALHÃO
- CURVA DE NÍVEL
- CARREADOR
- CONFRONTANTE
- REDE ELÉTRICA
- TRAJETO VAZIO
- TRAJETO CARREGADO


PLANTIO MANUAL - ESPAÇAMENTO: 1.50 X 1.50

Clealco
Açúcar, Etanol e Energia

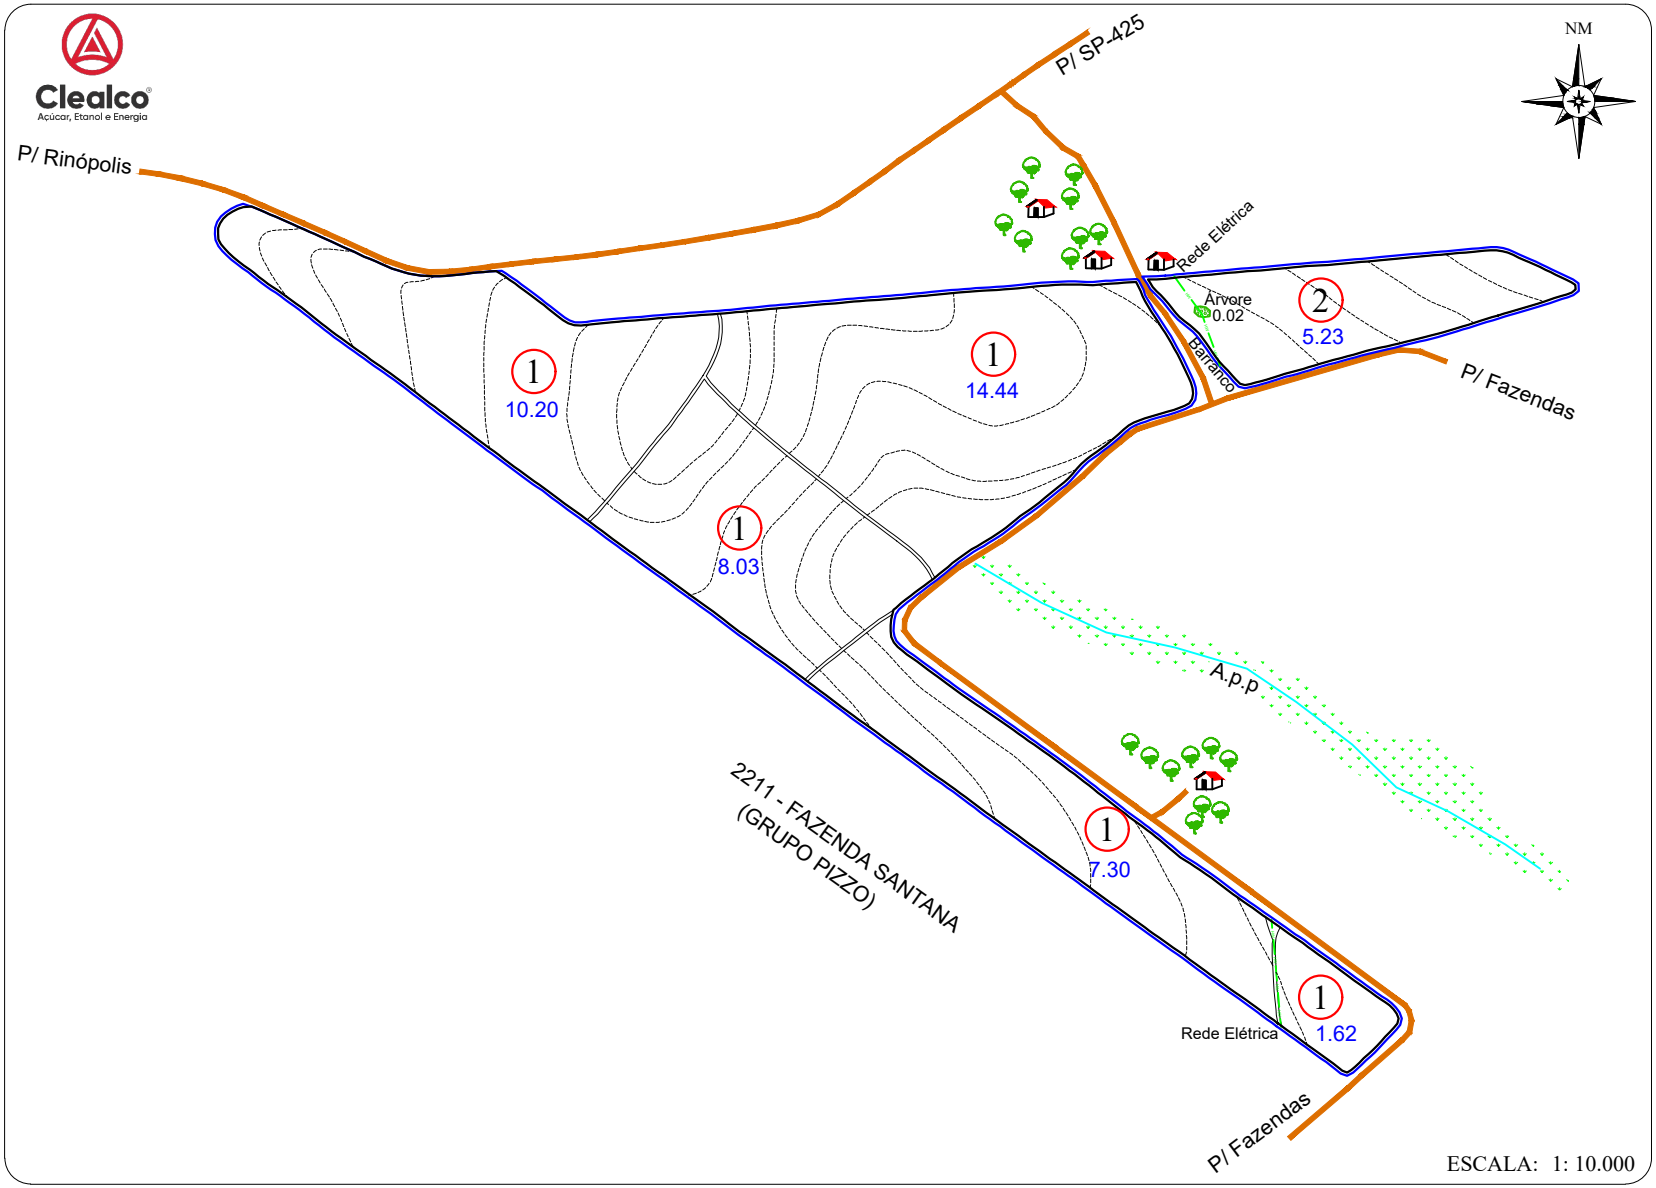

ESCALA: 1: 10.000

CROQUI DE ACESSO

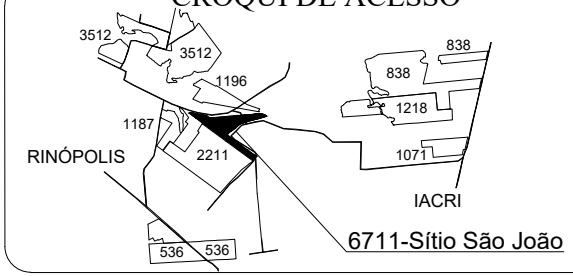

SÍTIO SÃO JOÃO

☐ CLEALCO ■ TERCEIRO ☐ PRÓPRIA ☐ FORNECEDOR

PROPRIETÁRIO: PRIMO BARALDI
ARRENDATÁRIO: GIL CARMO G. MACHADO
MUNICÍPIO: RINÓPOLIS

DISTÂNCIAS (km):
UNID. I - Asfalto: 35.00 Terra.: 8.50
UNID.I I - Asfalto: 69.50 Terra.: 8.50
UNID. III -Asfalto: 78.00 Terra.: 6.00

COORDENADAS: E(X): 535.404,20 N(Y): 7.596.379,05
LAT: 21°44'8.8013" LONG: 50°39'27.4946"

CLEALCO - AÇÚCAR E ALCOOL S/A - DEPARTAMENTO DE TOPOGRAFIA

UNIDADE: I
SETOR: D 16
FUNDO AGRÍCOLA: 306711

M:\01-Mapa de safra\Mapas Atualizados\Acionista\Regina Rahall Machado\306711 - Sítio São João (Gil Carmo Guaragna Machado)\306711 - Sítio São João (Gil Carmo Guaragna Machado).dwg

Pedro Becker 00/09/21