ZONA DV	Nº TAL.	DATA PL.	ÁREA (ha)	VARIEDADE
1 5.69 %	1	03/2022	27.66	RB 966928
	2		9.62	
	3		1.20	
TOTAL PLANTIO			38.48	--------

ÁREAS	(ha)	(%)
PLANTIO	38.48	92.12
CARREADORES	1.83	4.39
OUTROS	0.00	0.00
SUB TOTAL AGRICULTÁVEL	40.31	96.50
AP.P.	1.33	3.18
MATA	0.13	0.31
OUTROS	0.00	0.00
SUB TOTAL NÃO AGRICULT.	1.46	3.50
ÁREA TOTAL	41.77	100.00

C. NÍVEL: 4318.40 m/l 0.99 ha 2.38 %


LEGENDA

- FAZENDA
- TALHÃO
- CURVA DE NÍVEL
- CARREADOR
- CONFRONTANTE
- REDE ELÉTRICA
- TRAJETO VAZIO
- TRAJETO CARREGADO

PLANTIO MANUAL - ESPAÇAMENTO: 1.50 X 1.50
TIRO MÉDIO ESTIMADO: XXX.XX m


Clealco
Açúcar, Etanol e Energia

PÓS PLANTIO

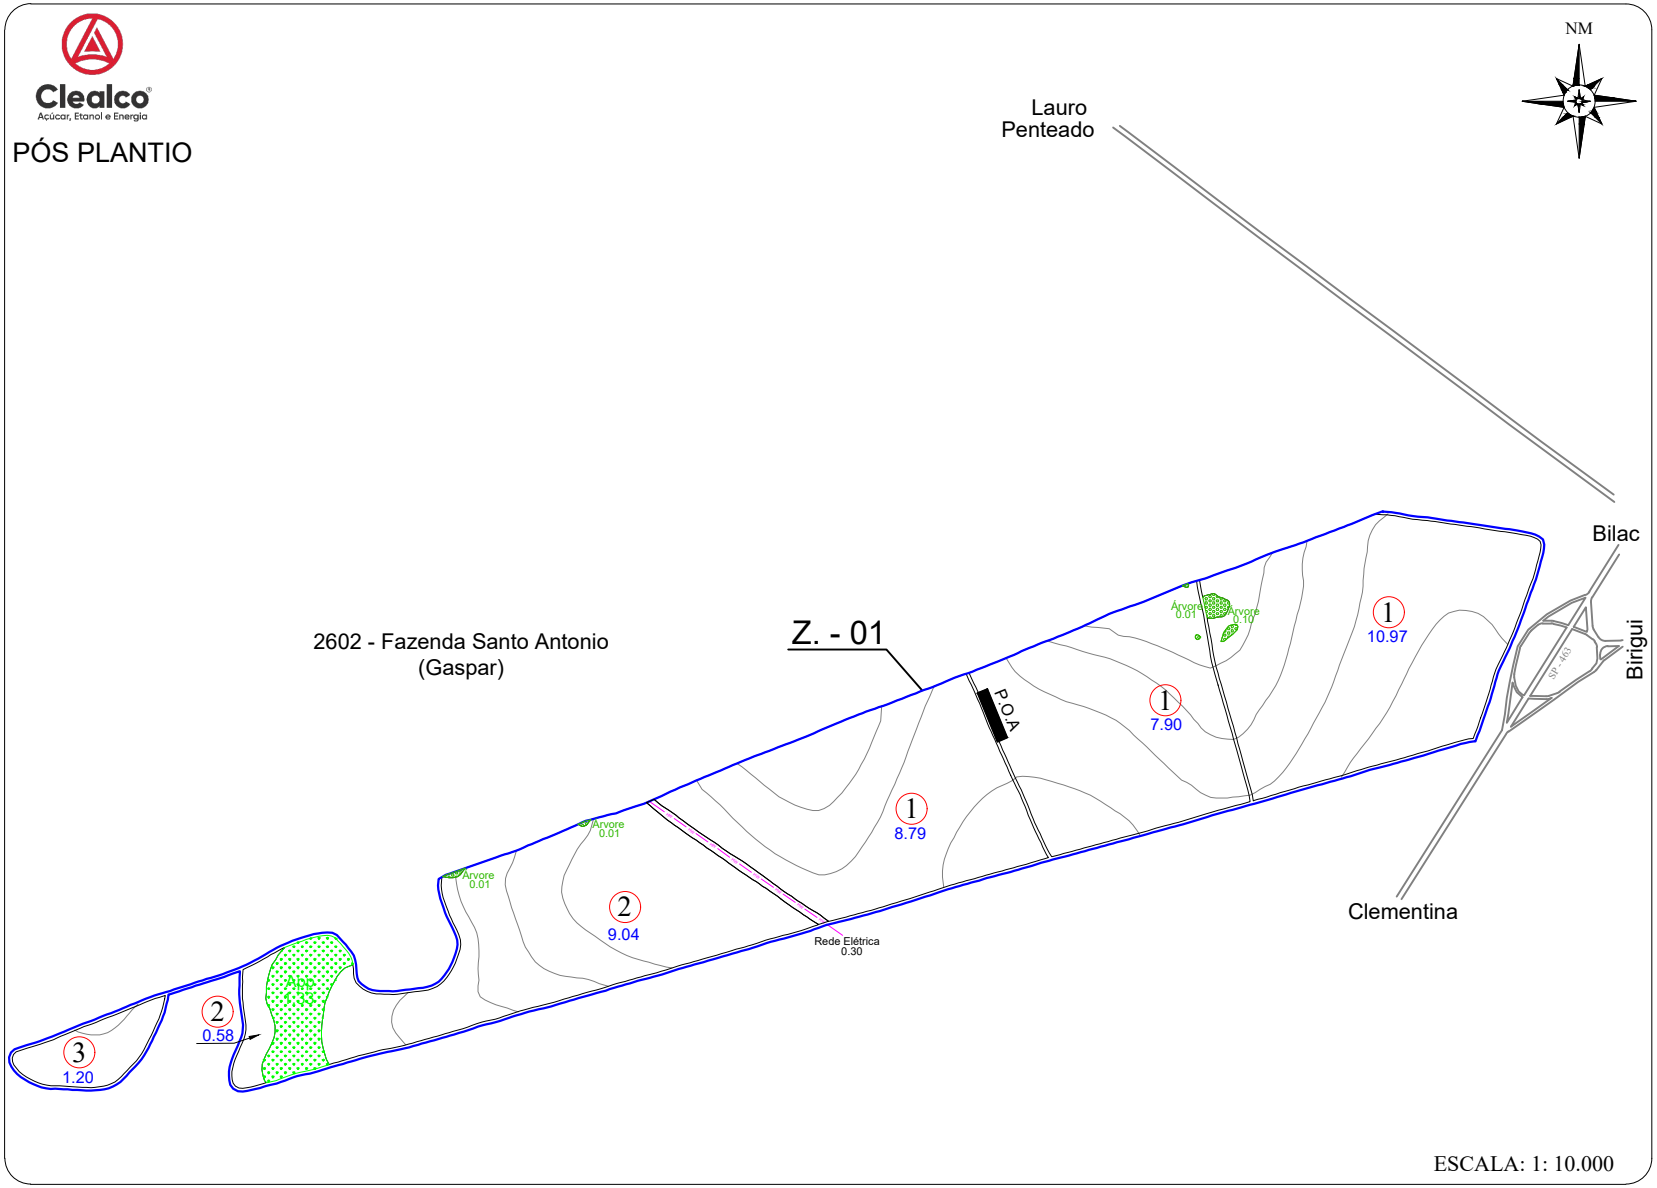

ESCALA: 1: 10.000

CROQUI DE ACESSO

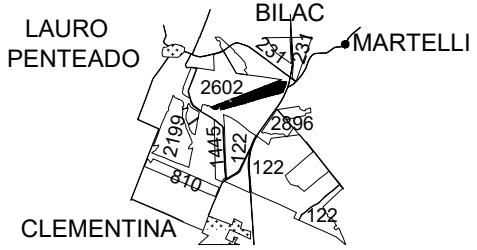

SÍTIO MARAVILHA

PROPRIETÁRIO: ANDRE V. LEMOS DE MELLO
COMPRADOR: CLEALCO S/A
MUNICÍPIO: CLEMENTINA

DISTÂNCIAS (km):

UNID. I - Asfalto:	7.00	Terra.:	0.50
UNID.I I - Asfalto:	55.00	Terra.:	0.50
UNID. III -Asfalto:	52.00	Terra.:	0.50

COORDENADAS: E(X): 558350,4396 N(Y): 7619890,8884
LAT: 21°31'21,90828" LONG: 50°26'11,67122"

CLEALCO - AÇÚCAR E ALCOOL S/A - DEPARTAMENTO DE TOPOGRAFIA

UNIDADE: I

PARTE: A/A

FUNDO AGRÍCOLA: 307166

M:\01-Mapa de safra\Mapas Safra 2023 - PIMS\Acionista\Susana Lemos\307166 - Sítio Maravilha (Andre Lemos de Melo) - 2023.dwg

Benati 02/06/2022