
Clealco
Açúcar, Etanol e Energia

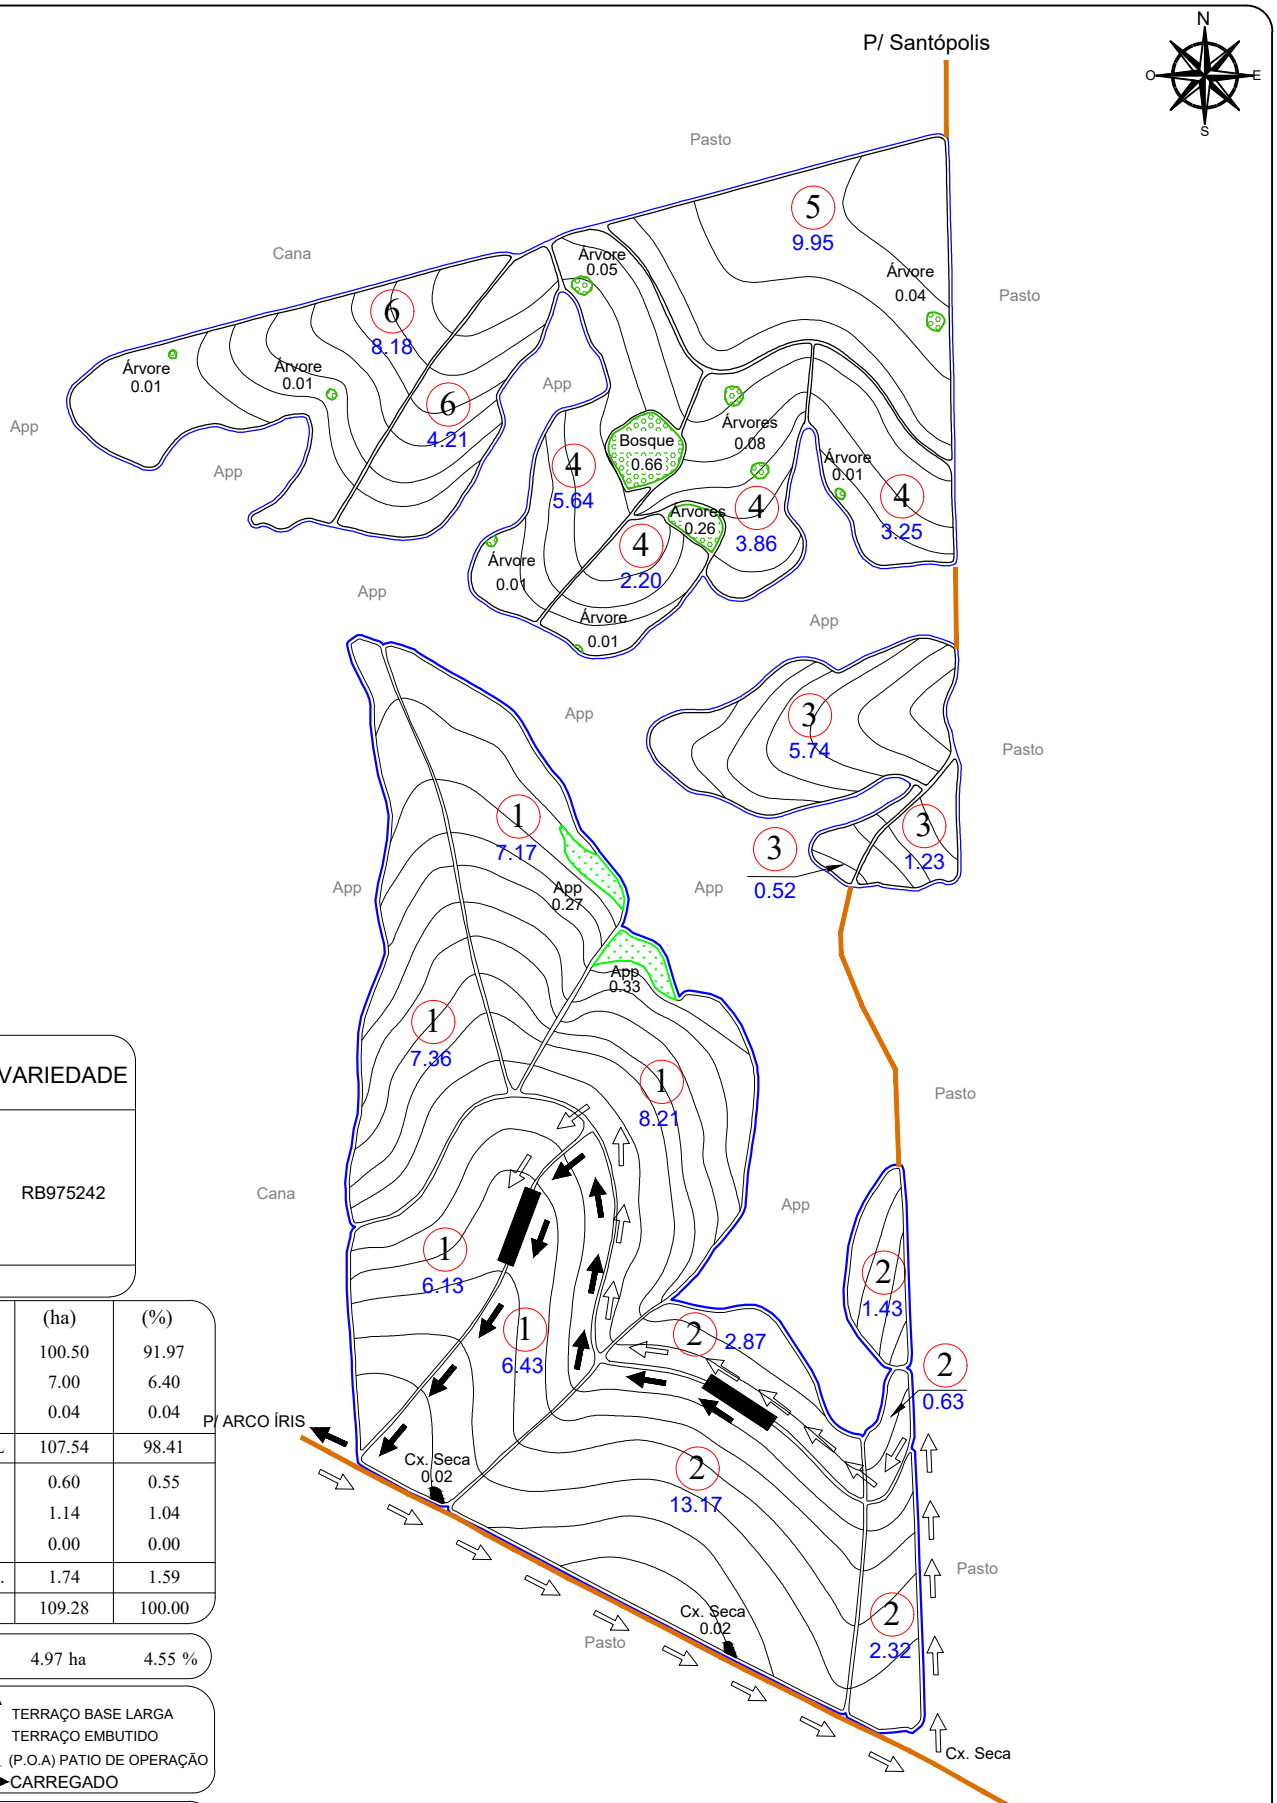

Nº TAL.	DATA PL.	ÁREA (ha)	VARIEDADE
1	05/2025	35.30	RB975242
2		20.42	
3	06/2024	7.48	
4		14.95	
5		9.95	
6		12.40	
TOTAL PLANTIO		100.50	

ÁREAS	(ha)	(%)
PLANTIO	100.50	91.97
CARREADORES	7.00	6.40
OUTROS	0.04	0.04
SUB TOTAL AGRICULTÁVEL	107.54	98.41
AP.P.	0.60	0.55
ÁRVORES	1.14	1.04
OUTROS	0.00	0.00
SUB TOTAL NÃO AGRICULT.	1.74	1.59
ÁREA TOTAL	109.28	100.00

C. NÍVEL: 21604.69 m/l 4.97 ha 4.55 %


LEGENDA

- FAZENDA
- TALHÃO
- REDE ELÉTRICA
- VAZIO
- TERRAÇO BASE LARGA
- TERRAÇO EMBUTIDO
- (P.O.A) PATIO DE OPERAÇÃO
- CARREGADO

ESPAÇAMENTO: 1.50 x 1.50
TIRO MÉDIO ESTIMADO: 163.77 m
D.V: 8.80 %

ESCALA: 1: 10.000

CROQUI DE ACESSO

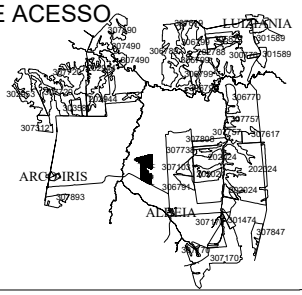

SÍTIO IRACEMA

PROPRIETÁRIO: VERA LUCIA PIZZO DOS REIS
COMPRADOR: CLEALCO
MUNICÍPIO: TUPÃ - SP

DISTÂNCIAS (km):
UNID. I - Asfalto: 48.00 Terra.: 40.00
UNID.I I - Asfalto: 29.00 Terra.: 27.00

COORDENADAS: E(X): 561830.43 N(Y): 7592869.10
LAT: -21°46'0.3462" LONG: -50°24'7.0915"

CLEALCO - AÇÚCAR E ALCOOL S/A - DEPARTAMENTO DE GEOTECNOLOGIA

LEVANTAMENTO VIA:
- SATÉLITE
- GPS / VANT
- GOOGLE

UNIDADE: I
PARTE: A/A
FUNDO AGRÍCOLA: 300643

M:\01-Mapa de safra\Mapas Atualizados\Acionista\Vera Lucia Pizzo dos Reis\300643 - Sitio Iracema (Vera Lucia Pizzo Dos Reis)\300643 - Sitio Iracema (Vera Lucia Pizzo Dos Reis).dwg

Bruno Gamboa 21/01/26