ZONA DV	CLA	Nº TAL.	DATA PL.	ÁREA (ha)	VAR.
1		1	04/2021	16.61	CTC 04
8.42 %		2		21.53	
TOTAL PLANTIO				38.14	--------


ÁREAS	(ha)	(%)
PLANTIO	38.14	93.76
CARREADORES	2.21	5.43
OUTROS	0.00	0.00
SUB TOTAL AGRICULTÁVEL	40.35	99.19
VÁRZEA	0.33	0.81
MATA	0.00	0.00
OUTROS	0.00	0.00
SUB TOTAL NÃO AGRICULT.	0.33	0.81
ÁREA TOTAL	40.68	100.00

C. NÍVEL: 7021.92 m/l 1.62 ha 4.34 %


LEGENDA

- FAZENDA
- TALHÃO
- CURVA DE NÍVEL
- CARREADOR
- CONFRONTANTE
- REDE ELÉTRICA
- TRAJETO VAZIO
- TRAJETO CARREGADO

PLANTIO MANUAL - ESPAÇAMENTO: 1.50 x 1.50

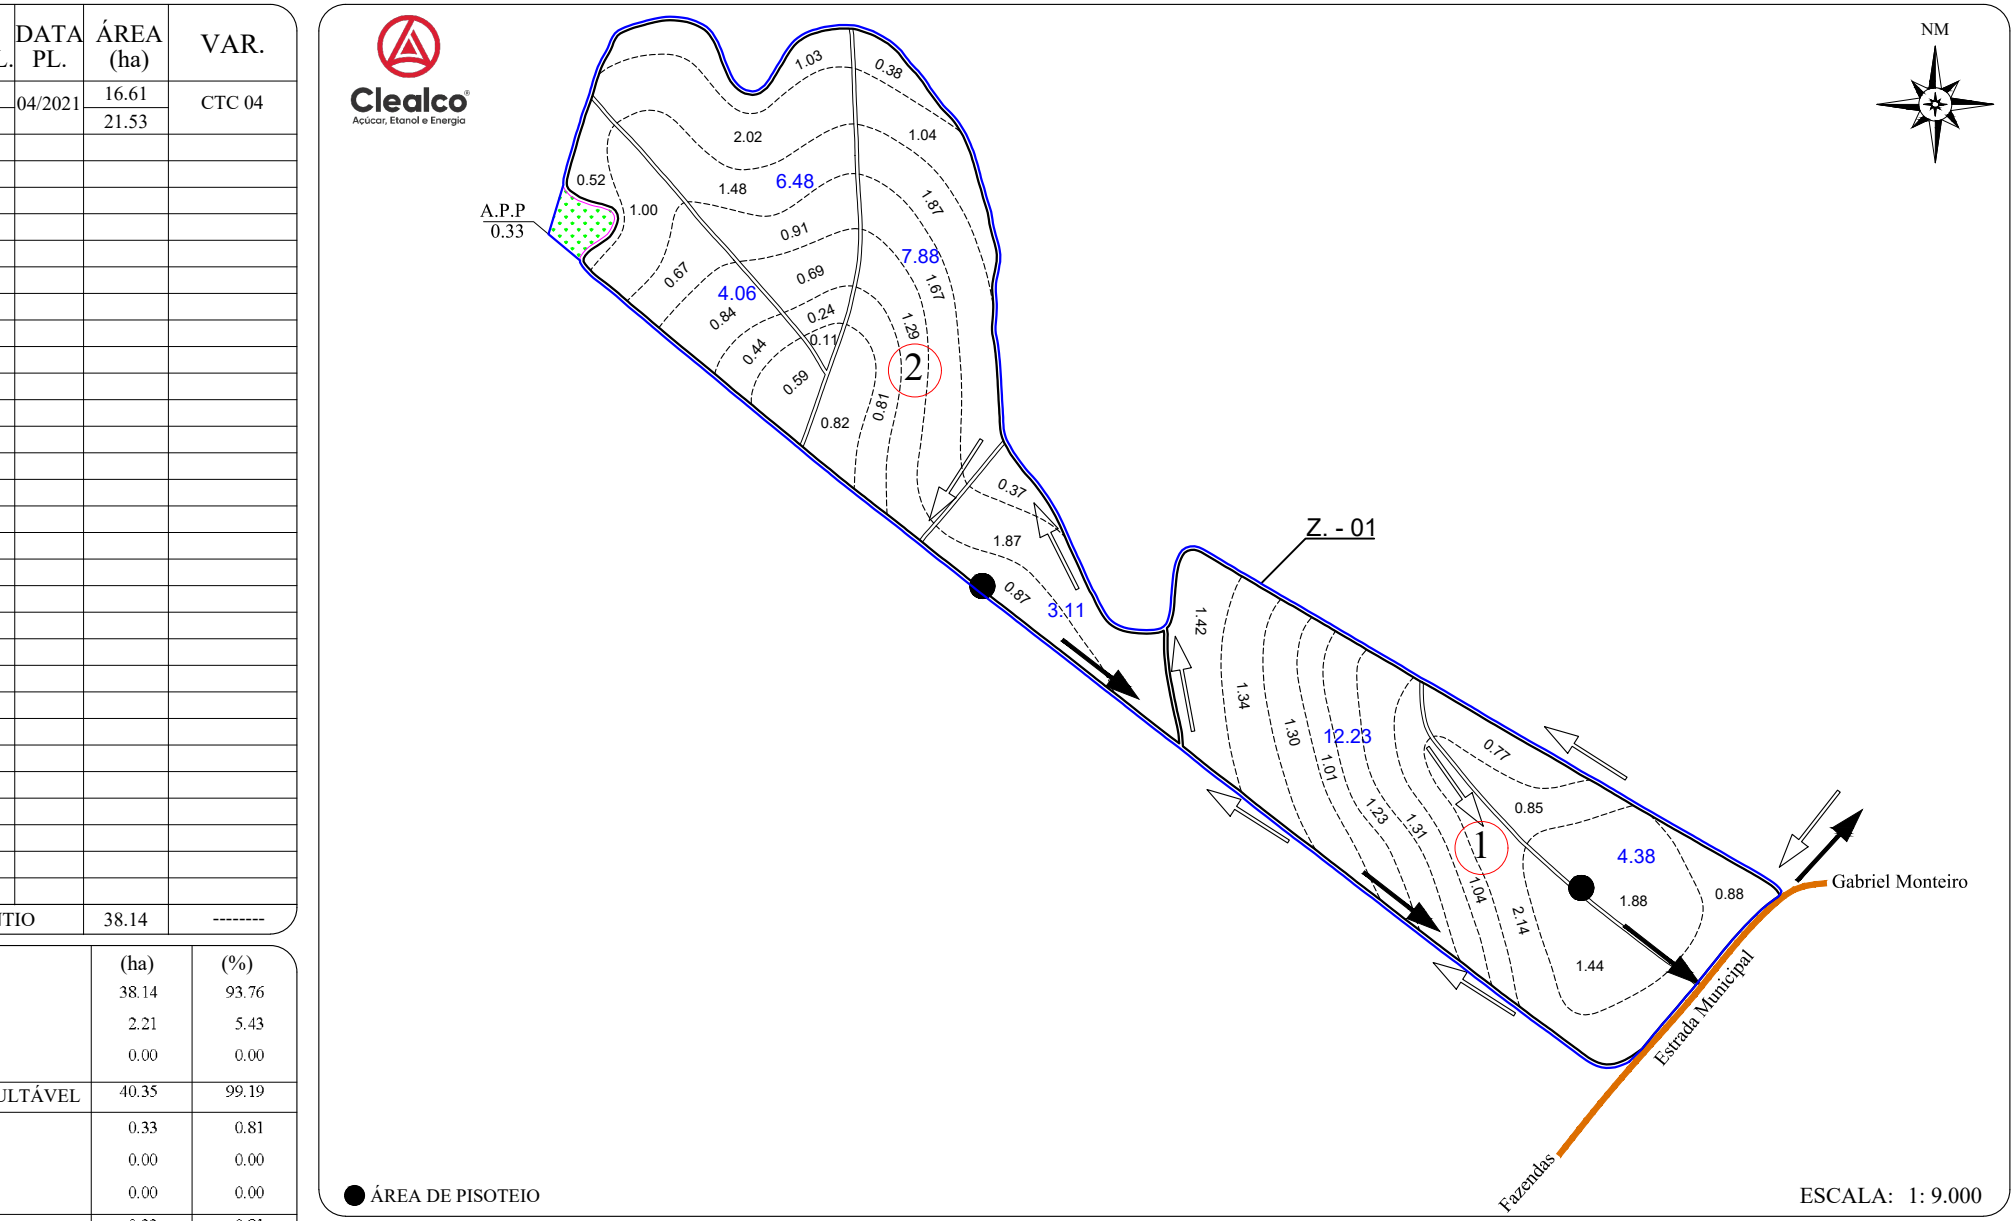

CROQUI DE ACESSO

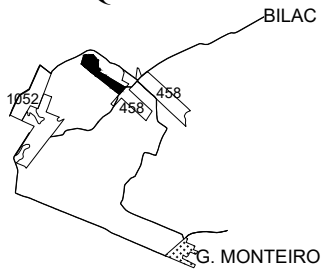

SÍTIO SÃO JOSÉ

PROPRIETÁRIO: ADÃO MAZIEIRO
ARRENDATÁRIO: VERA LÚCIA PIZZO DOS REIS
MUNICÍPIO: GABRIEL MONTEIRO

DISTÂNCIAS (km):
UNID. I - Asfalto: 8.80 Terra.: 18.70
UNID.I I - Asfalto: 57.00 Terra.: 18.70
UNID. III -Asfalto: 62.30 Terra.: 18.70

COORDENADAS: E(X): 543438.5023 N(Y): 7625455.931
LAT: 21º 28' 22" LONG: 50º 34' 50"

CLEALCO - AÇÚCAR E ALCOOL S/A - DEPARTAMENTO DE TOPOGRAFIA

UNIDADE: I
PARTE: A/A
FUNDO AGRÍCOLA: 301243

Pedro Becker 01/06/21