ZONA	Nº TAL.	DATA PL.	ÁREA (ha)	VARIEDADE
1	121	05/2021	33.83	RB 975242
	221		27.32	
	321		27.43	
	421		28.91	
	521		24.25	
TOTAL PLANTIO			141.74	--------


ÁREAS	(ha)	(%)
PLANTIO	141.74	96.84
CARREADORES	4.46	3.05
OUTROS	0.00	0.00
SUB TOTAL AGRICULTÁVEL	146.20	99.89
AP.P.	0.00	0.00
MATA	0.16	0.11
OUTROS	0.00	0.00
SUB TOTAL NÃO AGRICULT.	0.16	0.11
ÁREA TOTAL	146.36	100.00

C. NÍVEL: 15221.11 m/l 3.50 ha 2.39 %


LEGENDA

- FAZENDA
- TALHÃO
- CURVA DE NÍVEL
- CARREADOR
- CONFRONTANTE
- REDE ELÉTRICA
- TRAJETO VAZIO
- TRAJETO CARREGADO

PLANTIO MANUAL - ESPAÇAMENTO: 1.50 X 1.50

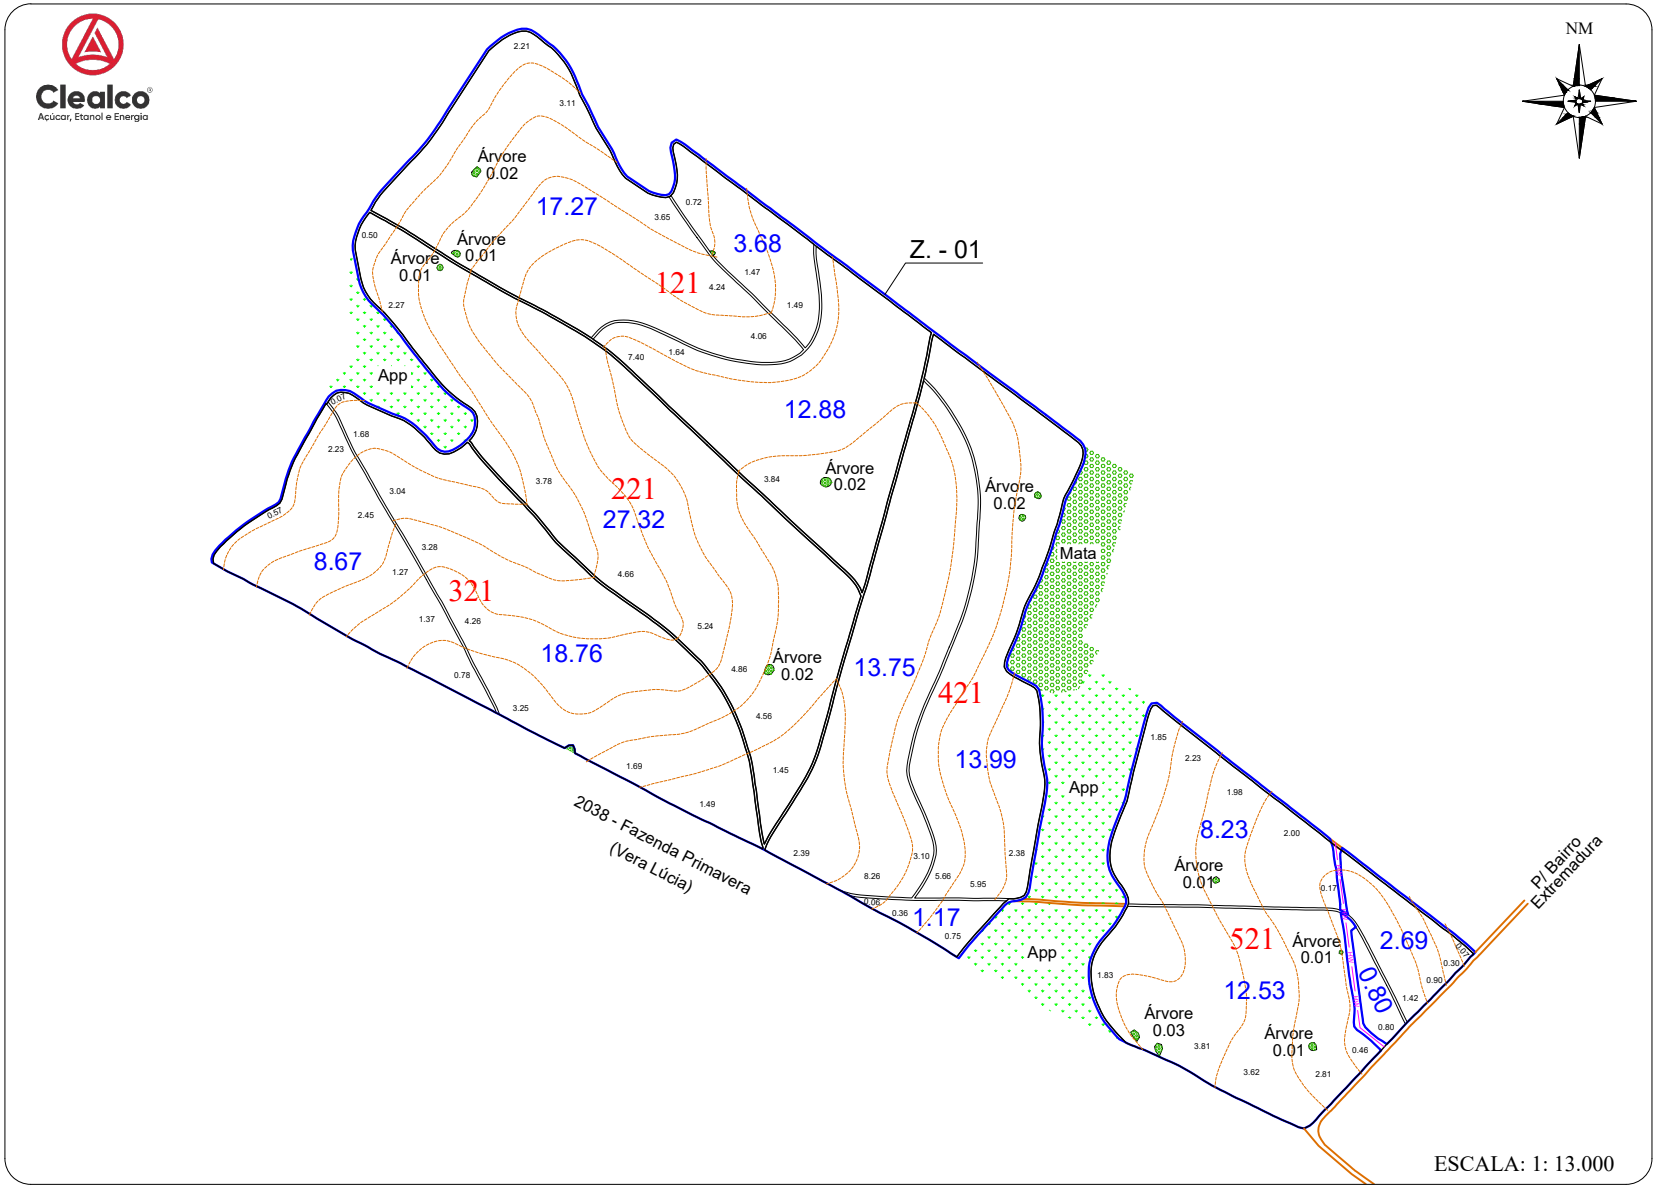

CROQUI DE ACESSO

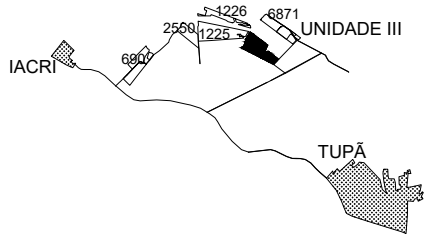

FAZENDA SÃO JOÃO

PROPRIETÁRIO: JOÃO GONÇALVEZ LOPES
ARRENDATÁRIO: VERA LÚCIA PIZZO DOS REIS
MUNICÍPIO: IACRI

DISTÂNCIAS (km):
UNID. I - Asfalto: 36.10 Terra.: 11.30
UNID.I I - Asfalto: 29.00 Terra.: 25.40
UNID. III -Asfalto: 82.10 Terra.: 11.30

COORDENADAS: E(X): 543651.7543 N(Y): 7583301.7207
LAT: 21°51'13,47064" LONG: 50°34'39,13650"

CLEALCO - AÇÚCAR E ALCOOL S/A - DEPARTAMENTO DE TOPOGRAFIA

UNIDADE: I

PARTE: A/A

FUNDO AGRÍCOLA: 302356

M:\01-Mapa de safra\Mapas Atualizados\Acionista\Vera Lucia Pizzo dos Reis\302356 - Fazenda São João (João Gonçalves Lopes)\302356 - Fazenda São João (João Gonçalves Lopes).dwg

Fernanda Laura 24/08/21