| ZONA DV | Nº TAL. | DATA PL. | ÁREA (ha) | VARIEDADE |
|---|---|---|---|---|
| 999 | 1 | 05/2022 | 30.06 | CTC 04 |
| | 2 | | 22.66 | |
| | 3 | | 34.18 | |
| | 4 | | 9.74 | |
| | 5 | | 1.42 | |
| | 6 | | 29.24 | |
| | 7 | | 25.49 | |
| | 8 | 05/2021 | 19.13 | |
| TOTAL PLANTIO | | | 171.92 | -------- |


| ÁREAS | (ha) | (%) |
|---|---|---|
| PLANTIO | 171.92 | 95.27 |
| CARREADORES | 6.98 | 3.87 |
| OUTROS | 0.00 | 0.00 |
| SUB TOTAL AGRICULTÁVEL | 178.90 | 99.14 |
| AP.P. | 0.00 | 0.00 |
| ÁRVORES | 0.06 | 0.03 |
| OUTROS | 1.50 | 0.83 |
| SUB TOTAL NÃO AGRICULT. | 1.56 | 0.86 |
| ÁREA TOTAL | 180.46 | 100.00 |

C. NÍVEL: 24219.24 m/l 5.57 ha 3.09 %

LEGENDA

- FAZENDA
- TALHÃO
- CURVA DE NÍVEL
- CARREADOR
- CONFRONTANTE
- REDE ELÉTRICA
- TRAJETO VAZIO
- TRAJETO CARREGADO


PLANTIO MANUAL - ESPAÇAMENTO: 1.50 X 1.50

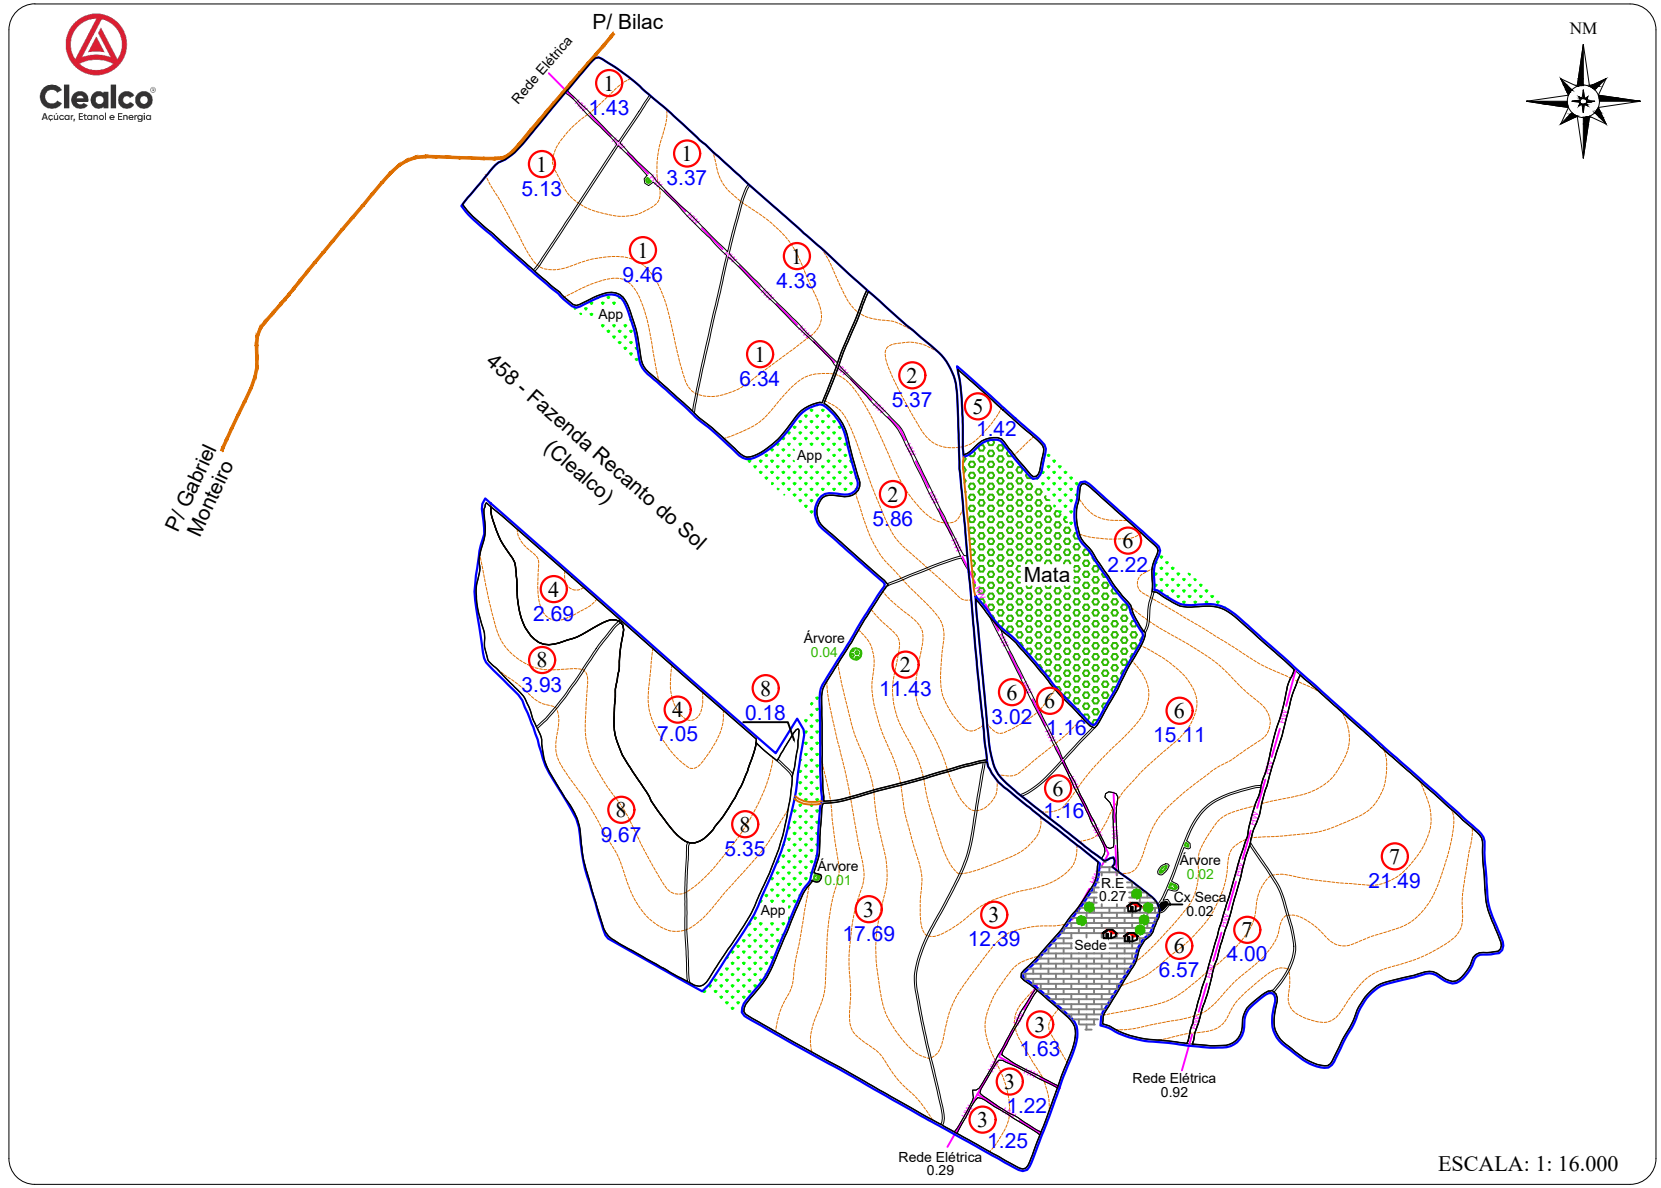


NM

ESCALA: 1: 16.000

CROQUI DE ACESSO

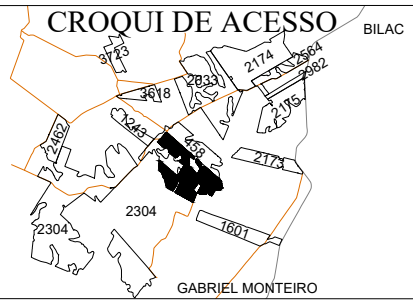


# FAZENDA CALIB

PROPRIETÁRIO: VERA LÚCIA PIZZO DOS REIS
COMPRADOR: CLEALCO S/A
MUNICÍPIO: GABRIEL MONTEIRO

DISTÂNCIAS (km):
UNID. I - Asfalto: 33.60 Terra.: 6.95
UNID.I I - Asfalto: 90.60 Terra.: 6.95
UNID. III -Asfalto: 75.00 Terra.: 6.95

COORDENADAS: E(X): 545431.02 N(Y): 7623685.03
LAT: 21° 29' 19,85039" LONG: 50° 33' 41,12387"

CLEALCO - AÇÚCAR E ALCOOL S/A - DEPARTAMENTO DE TOPOGRAFIA

UNIDADE: I

PARTE: A/A

FUNDO AGRÍCOLA: 302379

M:\01-Mapa de safra\Mapas Atualizados\Acionista\Vera Lucia Pizzo dos Reis\302379 - Fazenda Calib (Zaira Martinelli)\302379 - Fazenda Calib (Zaira Martinelli).dwg

Fernanda Bezerra 01/06/22