
Clealco
Açúcar, Etanol e Energia

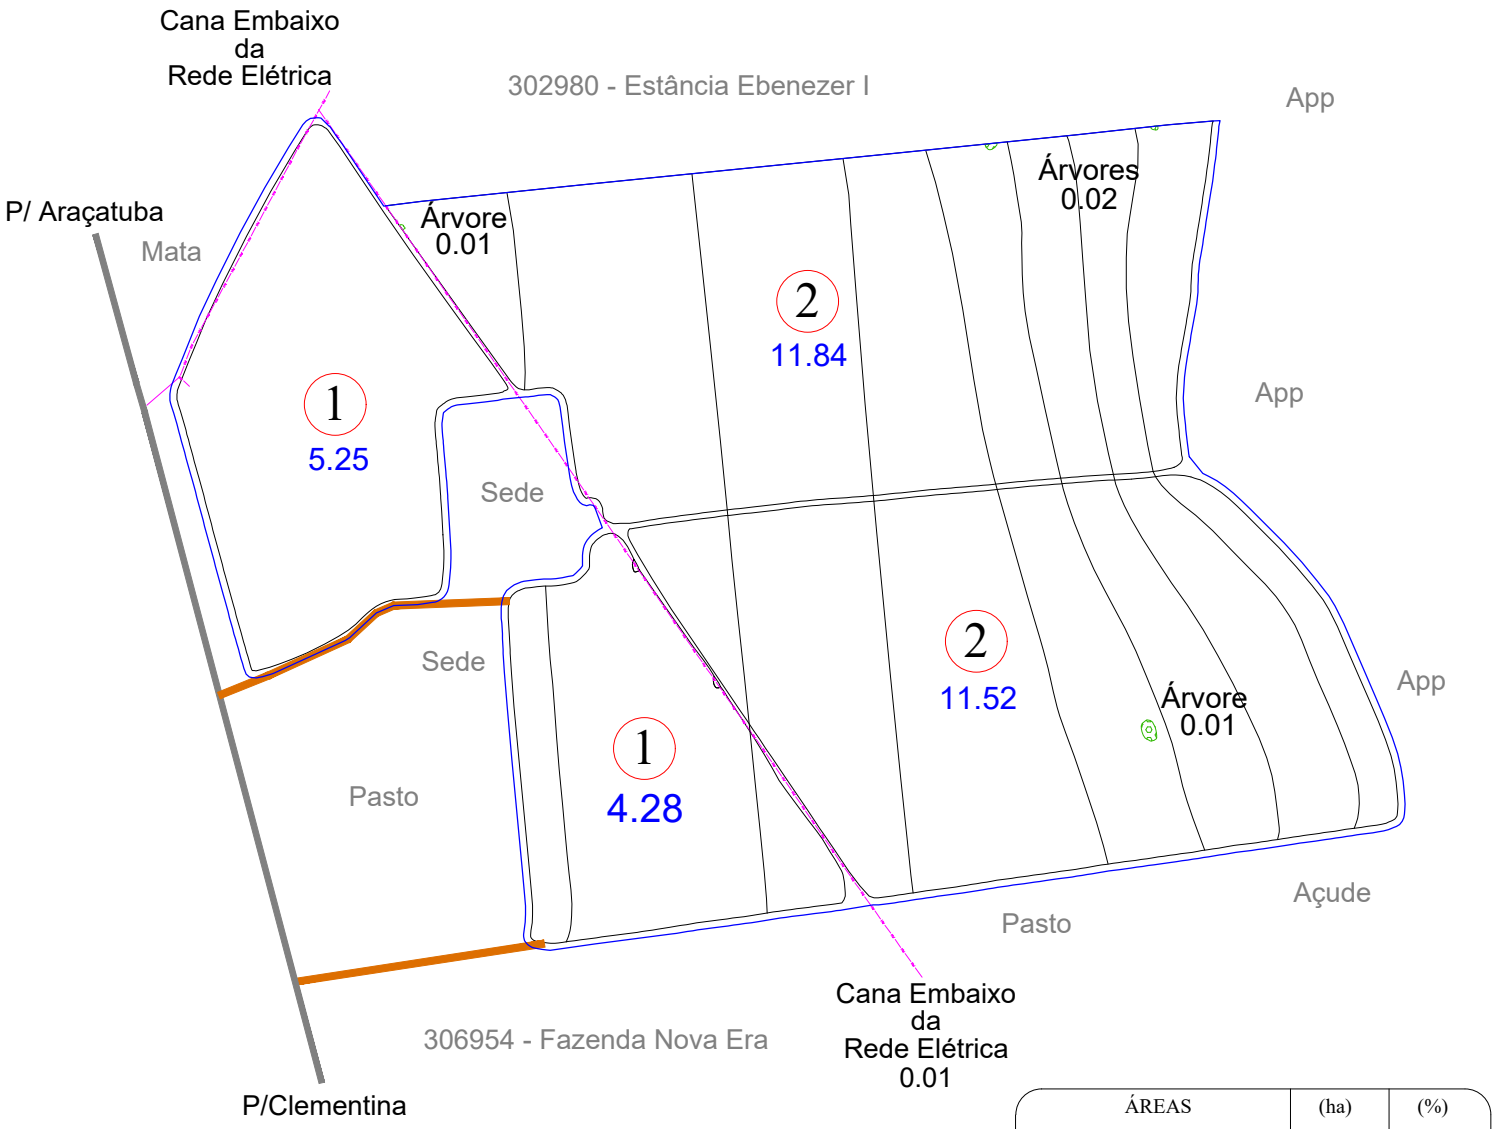

ÁREAS	(ha)	(%)
PLANTIO	32.89	95.32
CARREADORES	1.56	4.53
OUTROS	0.00	0.00
SUB TOTAL AGRICULTÁVEL	34.45	99.86
AP.P.	0.00	0.00
ÁRVORES	0.04	0.12
OUTROS	0.01	0.03
SUB TOTAL NÃO AGRICULT.	0.05	0.14
ÁREA TOTAL	34.50	100.00

C. NÍVEL: 3583.97 m/l 0.82 ha 2.39 %


Nº TAL.	DATA PL.	ÁREA (ha)	VARIEDADE
1	04/2026	9.53	RB97 5033
2		23.36	
TOTAL PLANTIO		32.89	

LEGENDA
- FAZENDA
- TALHÃO
- REDE ELÉTRICA
- TERRAÇO BASE LARGA
- TERRAÇO EMBUTIDO
- (P.O.A) PATIO DE OPERAÇÃO

ESPAÇAMENTO: 1.50 x 1.50
TIRO MÉDIO ESTIMADO: 271.78 m
D.V: 6.32 %

ESCALA: 1: 5.500

CROQUI DE ACESSO

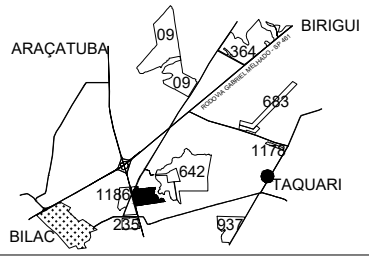

SÍTIO SANTO ANTONIO I

PROPRIETÁRIO: VERA LÚCIA PIZZO DOS REIS
COMPRADOR: CLEALCO
MUNICÍPIO: BILAC - SP

DISTÂNCIAS (km):
UNID. I - Asfalto: 22.00 Terra.: 0.50
UNID.I I - Asfalto: 77.50 Terra.: 0.50

COORDENADAS: E(X): 556922.67 N(Y): 7634265.26
LAT: -21°23'34.5463" LONG: -50°27'3.0524"

CLEALCO - AÇÚCAR E ALCOOL S/A - DEPARTAMENTO DE GEOTECNOLOGIA

LEVANTAMENTO VIA:
- SATÉLITE
- GPS / VANT
- GOOGLE

UNIDADE: I
PARTE: A/A
FUNDO AGRÍCOLA: 302979

M:\01-Mapa de safra\Mapas Atualizados\Acionista\Vera Lucia Pizzo dos Reis\302979 - Sitio Santo Antonio I (Adelino Nogueira)\302979 - Sitio Santo Antonio I (Vera Lucia Pizzo).dwg

Bruno Gamboa 01/09/26