
Clealco
Açúcar, Etanol e Energia

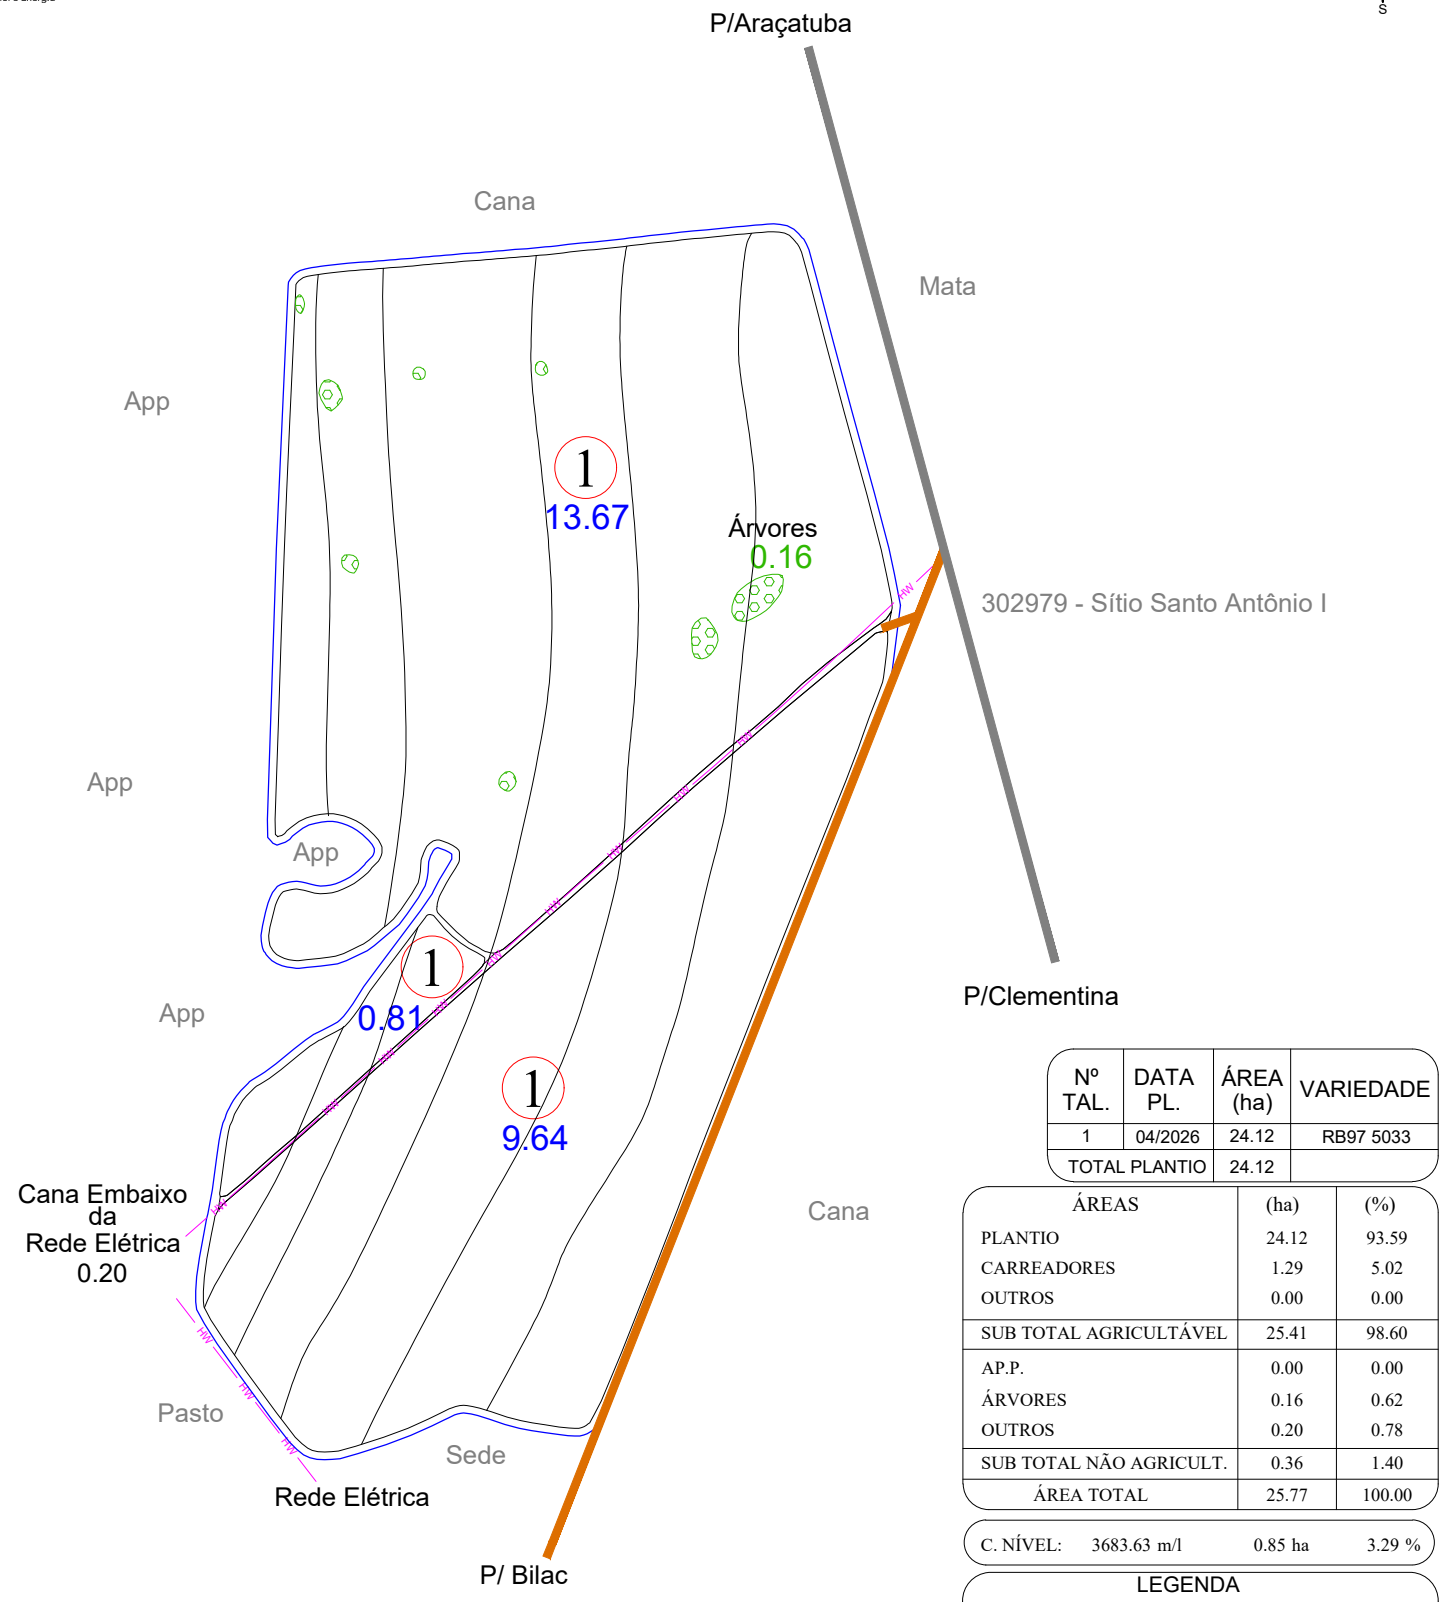

Nº TAL.	DATA PL.	ÁREA (ha)	VARIEDADE
1	04/2026	24.12	RB97 5033
TOTAL PLANTIO		24.12	

ÁREAS	(ha)	(%)
PLANTIO	24.12	93.59
CARREADORES	1.29	5.02
OUTROS	0.00	0.00
SUB TOTAL AGRICULTÁVEL	25.41	98.60
AP.P.	0.00	0.00
ÁRVORES	0.16	0.62
OUTROS	0.20	0.78
SUB TOTAL NÃO AGRICULT.	0.36	1.40
ÁREA TOTAL	25.77	100.00

C. NÍVEL: 3683.63 m/l 0.85 ha 3.29 %


LEGENDA

- FAZENDA
- TALHÃO
- REDE ELÉTRICA
- TERRAÇO BASE LARGA
- TERRAÇO EMBUTIDO
- (P.O.A) PATIO DE OPERAÇÃO

ESPAÇAMENTO: 1.50 x 1.50
TIRO MÉDIO ESTIMADO: 242.72 m
D.V: 3.69 %

ESCALA: 1: 5.000

CROQUI DE ACESSO

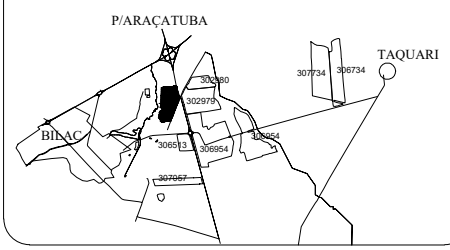

SÍTIO NOSSA SENHORA APARECIDA

PROPRIETÁRIO: VERA LÚCIA PIZZO DOS REIS
COMPRADOR: CLEALCO
MUNICÍPIO: BILAC - SP

DISTÂNCIAS (km):
UNID. I - Asfalto: 22.00 Terra.: 0.50
UNID.I I - Asfalto: 77.50 Terra.: 0.50

COORDENADAS: E(X): 556274.66 N(Y): 7634178.40
LAT: -21°23'37.4446" LONG: -50°27'25.5468"

CLEALCO - AÇÚCAR E ALCOOL S/A - DEPARTAMENTO DE GEOTECNOLOGIA

LEVANTAMENTO VIA:
SATÉLITE
GPS / VANT
GOOGLE

UNIDADE: I
PARTE: A/A
FUNDO AGRÍCOLA: 302981

M:\01-Mapa de safra\Mapas Atualizados\Acionista\Vera Lucia Pizzo dos Reis\302981 - Sitio Nossa Senhora Aparecida (José Adelino Nagorato)\302981 - Sitio Nossa Senhora Aparecida (José Adelino Nagorato).dwg

Bruno Gamboa 02/09/26