ZONA D.V.	Nº TAL.	DATA PL.	ÁREA (ha)	VAR.
01 6.44%	1	5/2022	22.50	RB975242
	2		22.83	
	3		22.58	
	4		14.52	
	5		1.96	
	6		26.95	
	7		4.58	
	8		5.74	
	9		1.39	
TOTAL PLANTIO			123.05	--------


ÁREAS	(ha)	(%)
PLANTIO	123.05	93.13
CARREADORES	8.10	6.13
OUTROS	0.00	0.00
SUB TOTAL AGRICULTÁVEL	131.15	99.26
AP.P.	0.00	0.00
ÁRVORES	0.00	0.00
OUTROS	0.98	0.74
SUB TOTAL NÃO AGRICULT.	0.98	0.74
ÁREA TOTAL	132.13	100.00

C. NÍVEL: 15137.24 m/l 3.48 ha 2.63 %


LEGENDA

- FAZENDA
- TALHÃO
- CURVA DE NÍVEL
- CARREADOR
- CONFRONTANTE
- REDE ELÉTRICA
- TRAJETO VAZIO
- TRAJETO CARREGADO

PLANTIO MANUAL - ESPAÇAMENTO: 1.50 X 1.50
TIRO MÉDIO ESTIMADO: 000.00m

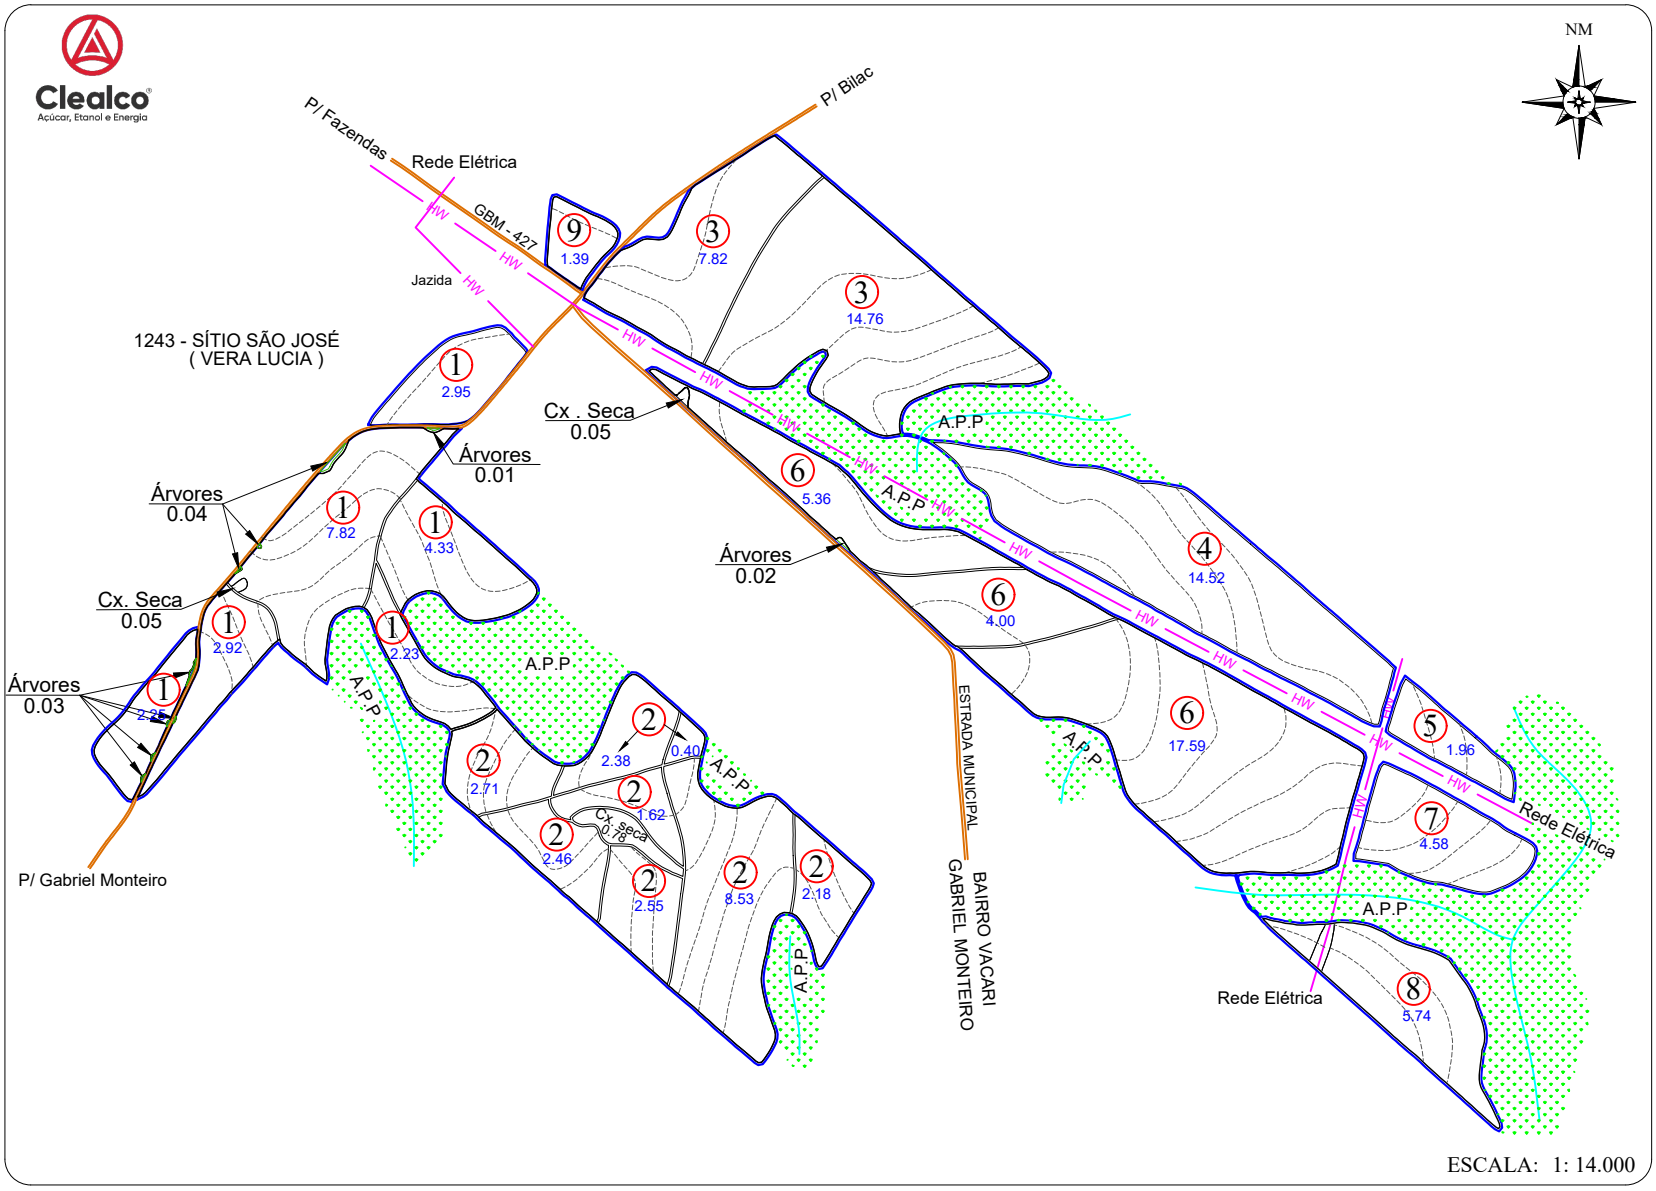

CROQUI DE ACESSO

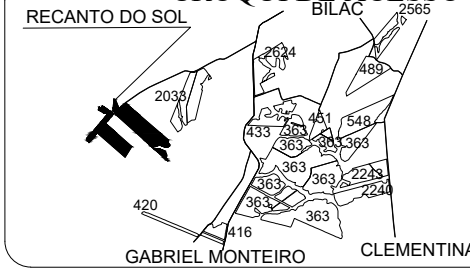

FAZENDA RECANTO DO SOL

PROPRIETÁRIO: REBECA W. MASCHIETTO
ARRENDATARIO: VERA LÚCIA PIZZO DOS REIS
MUNICÍPIO: GABRIEL MONTEIRO - SP

DISTÂNCIAS (km):
UNID. I - Asfalto: 8.80 Terra.: 18.70
UNID.I I - Asfalto: 57.00 Terra.: 17.50
UNID. III -Asfalto: 63.00 Terra.: 18.70

COORDENADAS: E(X): N(Y):
LAT: LONG:

CLEALCO - AÇÚCAR E ALCOOL S/A - DEPARTAMENTO DE TOPOGRAFIA

UNIDADE: I
PARTE: A/A
FUNDO AGRÍCOLA: 307155