D.V.	Nº TAL.	DATA PL.	ÁREA (ha)	VAR.
3.77 %	1	02/2023	38.09	RB975201
TOTAL PLANTIO			38.09	--------

ÁREAS	(ha)	(%)
PLANTIO	38.09	95.96
CARREADORES	1.59	3.99
OUTROS	0.00	0.00
SUB TOTAL AGRICULTÁVEL	39.68	99.95
AP.P.	0.00	0.00
ÁRVORES	0.02	0.05
OUTROS	0.00	0.00
SUB TOTAL NÃO AGRICULT.	0.02	0.05
ÁREA TOTAL	39.70	100.00

C. NÍVEL:	0.00 m/l	0.00 ha	0.00 %

LEGENDA

▬ FAZENDA	▬ CONFRONTANTE
▬ TALHÃO	▬ REDE ELÉTRICA
▬ CURVA DE NÍVEL	─▷ TRAJETO VAZIO
─ CARREADOR	─► TRAJETO CARREGADO

PLANTIO MANUAL - ESPAÇAMENTO: 1.50 X 1.50
TIRO MÉDIO ESTIMADO: 452.36m

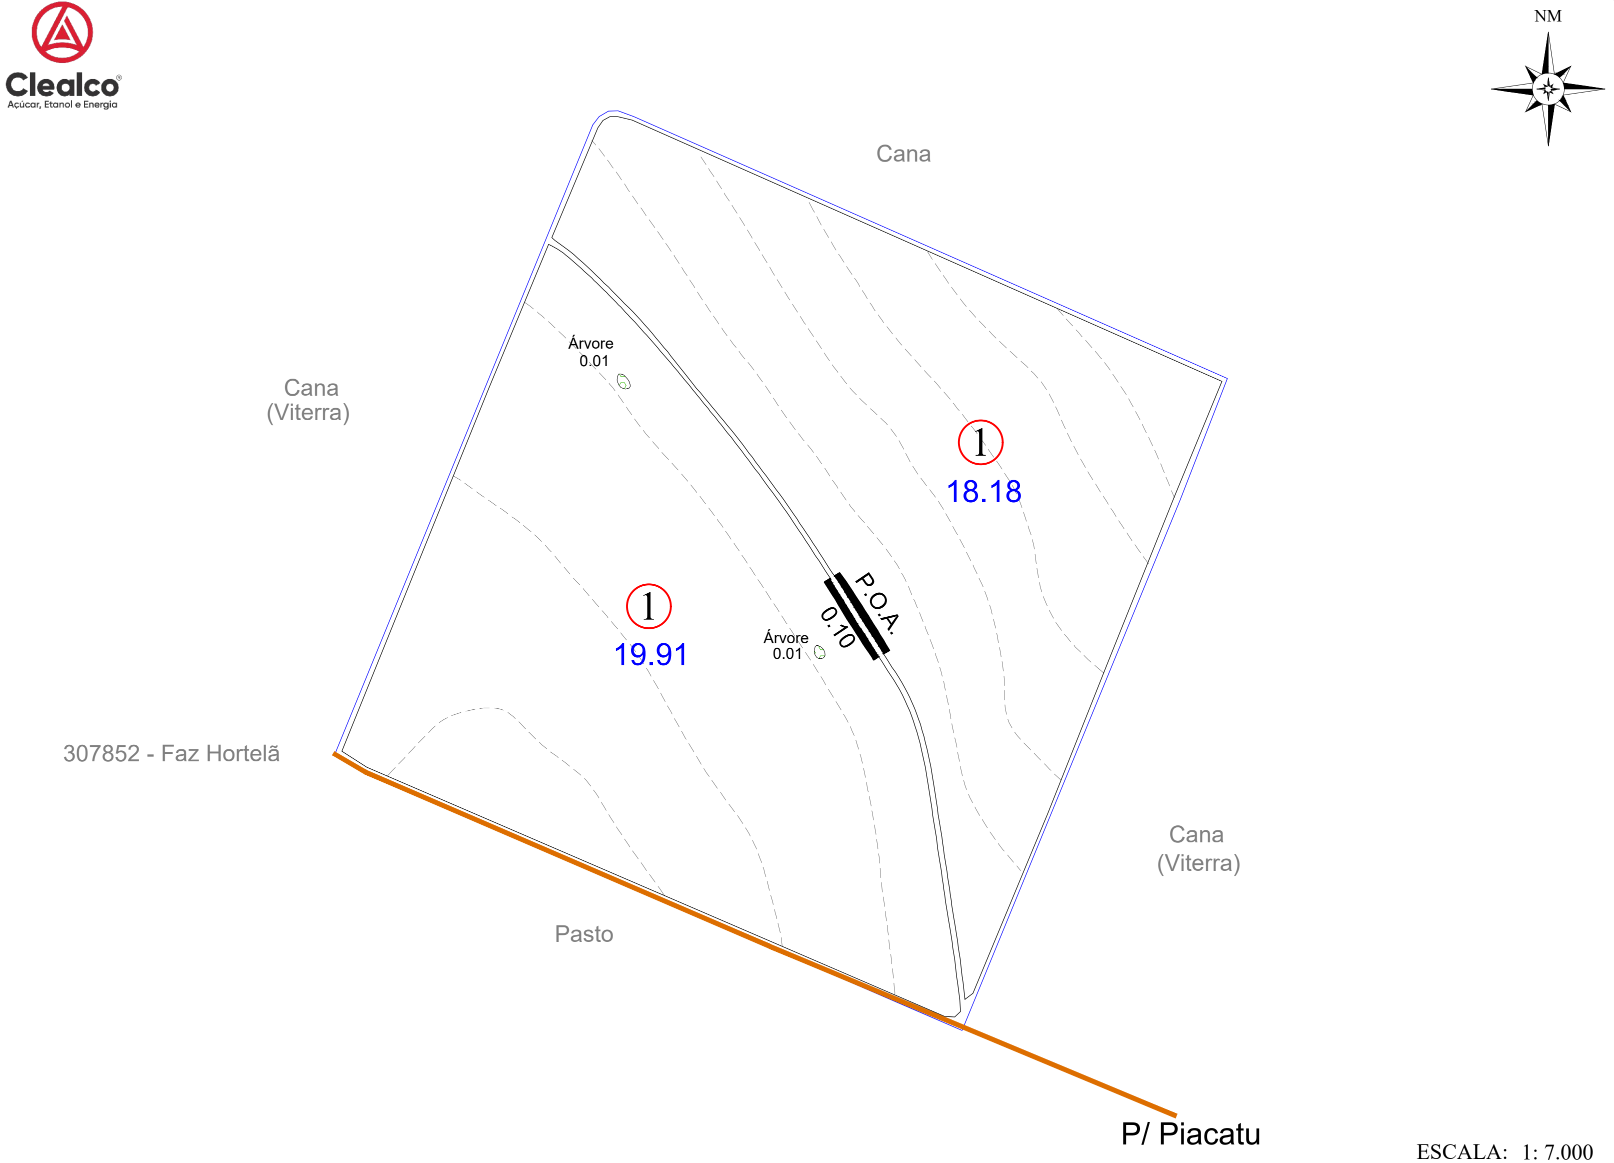

ESCALA: 1: 7.000

CROQUI DE ACESSO

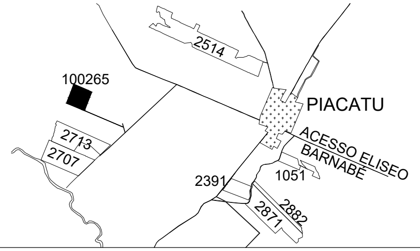

SITIO SÃO PEDRO

PROPRIETÁRIO:	CLEALCO S/A
COMPRADOR:	CLEALCO S/A
MUNICÍPIO:	PIACATU - SP

DISTÂNCIAS (km):

UNID. I -	Asfalto:	26.50	Terra.:	3.45
UNID.I I -	Asfalto:	63.20	Terra.:	3.45
UNID. III -	Asfalto:	71.95	Terra.:	3.45

COORDENADAS:	E(X):	535335.40	N(Y):	7612957.62
	LAT:	-21°35'9.5851"	LONG:	-50°39'31.1588"

CLEALCO - AÇÚCAR E ALCOOL S/A - DEPARTAMENTO DE TOPOGRAFIA

UNIDADE:
I

PARTE:
A/A

FUNDO AGRÍCOLA:
100265

M:\01-Mapa de safra\Mapas Atualizados\Clealco\100265 - Sítio São Pedro (Clealco)\100265 - Sítio São Pedro (Clealco).dwg

Peterson Santos 03/07/2023