
Clealco
Açúcar, Etanol e Energia

Nº TAL.	DATA PL.	ÁREA (ha)	VARIEDADE
1	2026	54.95	Pré Plantio
2	05/2022	64.02	VIVEIRO
3	2026	21.07	Pré Plantio
TOTAL PLANTIO		140.04	

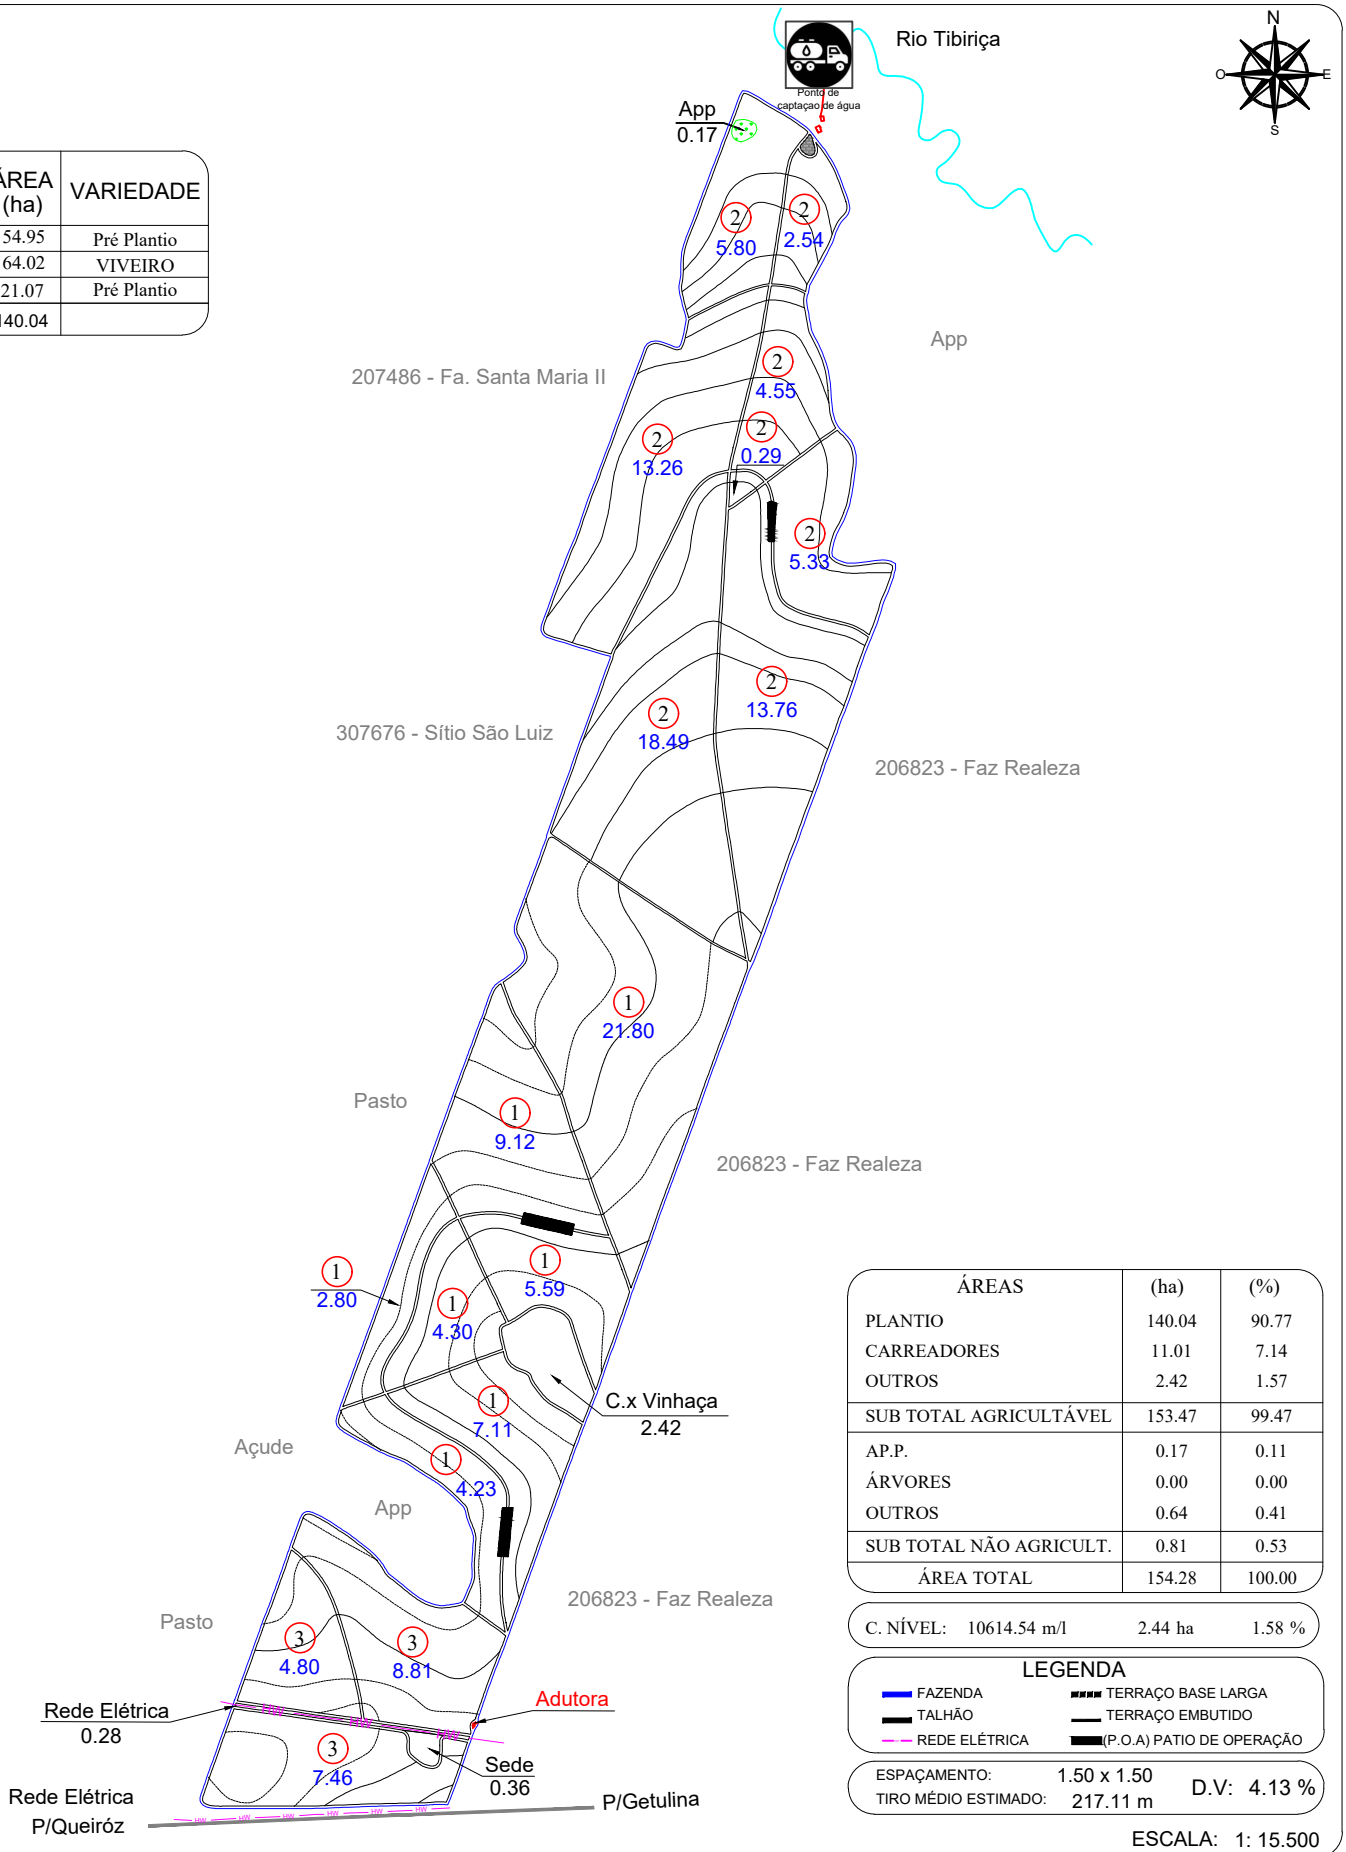

ÁREAS	(ha)	(%)
PLANTIO	140.04	90.77
CARREADORES	11.01	7.14
OUTROS	2.42	1.57
SUB TOTAL AGRICULTÁVEL	153.47	99.47
AP.P.	0.17	0.11
ÁRVORES	0.00	0.00
OUTROS	0.64	0.41
SUB TOTAL NÃO AGRICULT.	0.81	0.53
ÁREA TOTAL	154.28	100.00

C. NÍVEL: 10614.54 m/l 2.44 ha 1.58 %


LEGENDA

- FAZENDA
- TALHÃO
- REDE ELÉTRICA
- TERRAÇO BASE LARGA
- TERRAÇO EMBUTIDO
- (P.O.A) PATIO DE OPERAÇÃO

ESPAÇAMENTO: 1.50 x 1.50
TIRO MÉDIO ESTIMADO: 217.11 m
D.V: 4.13 %

ESCALA: 1: 15.500

CROQUI DE ACESSO

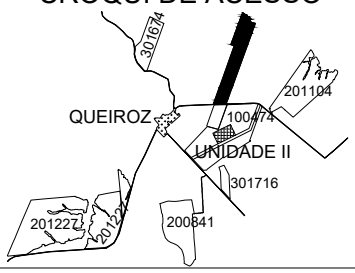

FAZENDA PAIQUERE

PROPRIETÁRIO: CLEALCO
COMPRADOR: CLEALCO
MUNICÍPIO: QUEIROZ - SP

DISTÂNCIAS (km):
UNID. I - Asfalto: 53.00 Terra.: 1.50
UNID.I I - Asfalto: 4.50 Terra.: 1.50

COORDENADAS: E(X): 581078.59 N(Y): 7590830.25
LAT: -21°47'3.8541" LONG: -50°12'56.5606"

CLEALCO - AÇÚCAR E ALCOOL S/A - DEPARTAMENTO DE GEOTECNOLOGIA

LEVANTAMENTO VIA:
SATÉLITE
GPS / VANT
GOOGLE

UNIDADE: II
PARTE: A/A
FUNDO AGRÍCOLA: 100542

M:\01-Mapa de safra\Mapas Atualizados\Clealco\100542 - Fazenda Paiquere (Clealco)\100542 - Fazenda Paiquere (Clealco) .dwg

Peterson Santos 19/05/2026