
Clealco
Açúcar, Etanol e Energia

Pós Plantio

ÁREAS	(ha)	(%)
PLANTIO	218.84	90.75
CARREADORES	16.75	6.95
OUTROS	0.00	0.00
SUB TOTAL AGRICULTÁVEL	235.59	97.70
AP.P.	4.76	1.97
ÁRVORES	0.08	0.03
OUTROS	0.70	0.29
SUB TOTAL NÃO AGRICULT.	5.54	2.30
ÁREA TOTAL	241.13	100.00

C. NÍVEL: 4130.95 m/l 0.95 ha 0.39 %

D.V.	Nº TAL.	DATA PL.	ÁREA (ha)	VARIEDADE
8.12%	1	2025	6.02	RB 975033
	2		15.35	
	3		14.09	
	4		18.52	
	5		15.07	
	6		15.58	
	7		19.89	
	8		16.23	
	9		14.65	
	10		10.51	
	11		6.88	
	12		28.78	
	13		15.27	
	14		7.59	
	15		14.41	
TOTAL PLANTIO			218.84	----------

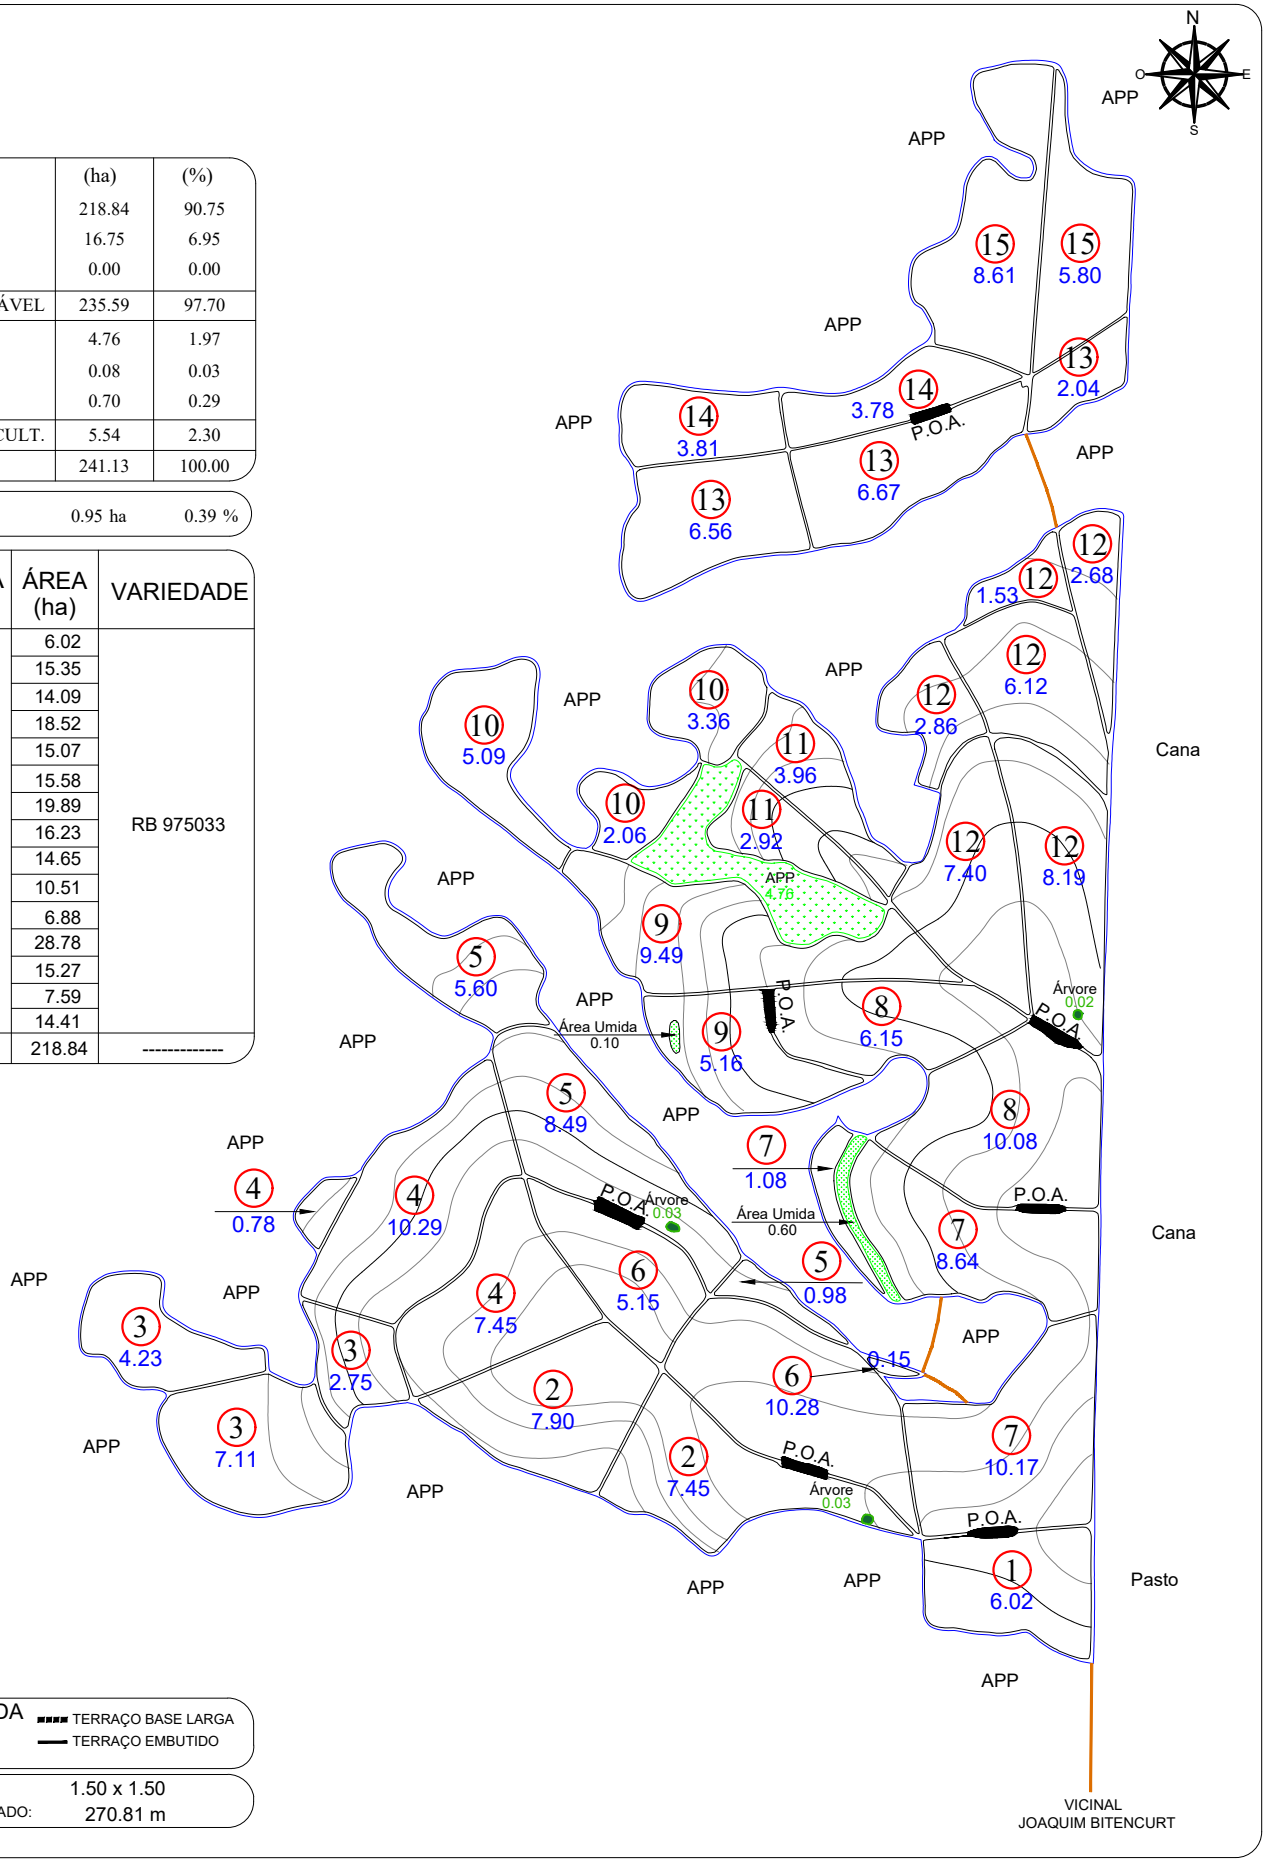

LEGENDA


- FAZENDA
- TALHÃO
- REDE ELÉTRICA
- TERRAÇO BASE LARGA
- TERRAÇO EMBUTIDO

ESPAÇAMENTO: 1.50 x 1.50

TIRO MÉDIO ESTIMADO: 270.81 m

ESCALA: 1: 14.500

CROQUI DE ACESSO

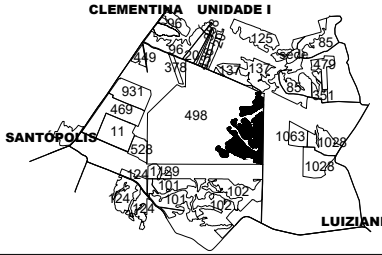

FAZENDA LUIZIÂNIA

PROPRIETÁRIO: CLEALCO S/A
COMPRADOR: CLEALCO S/A
MUNICÍPIO: LUIZIÂNIA - SP

DISTÂNCIAS (km):
UNID. I - Asfalto: 23.00 Terra.: 4.50
UNID.I I - Asfalto: 37.00 Terra.: 4.50
UNID. III -Asfalto: 12.70 Terra.: 4.50

COORDENADAS: E(X): 560418.55 N(Y): 7607037.61
LAT: -21°38'19.7065" LONG: -50°24'58.1096"

CLEALCO - AÇÚCAR E ALCOOL S/A - DEPARTAMENTO DE GEOTECNOLOGIA

UNIDADE: I

FUNDO AGRÍCOLA: 100565

M:\01-Mapa de safra\Mapas Atualizados\Clealco\100565 - Fazenda Luiziânia (Clealco)\100565 - Fazenda Luiziânia (Clealco).dwg

Benati 25/08/2025