
Clealco
Açúcar, Etanol e Energia

Nº TAL.	DATA PL.	ÁREA (ha)	VARIEDADE
1	03/2025	24.35	RB966928
2		29.96	CTC 9001
3		42.42	RB966928
4		18.01	
5		26.86	
TOTAL PLANTIO		141.60	

(N.P)-NÃO PLANTOU	
TALHÃO	(ha)
1	0.43
4	0.32
Total	0.75

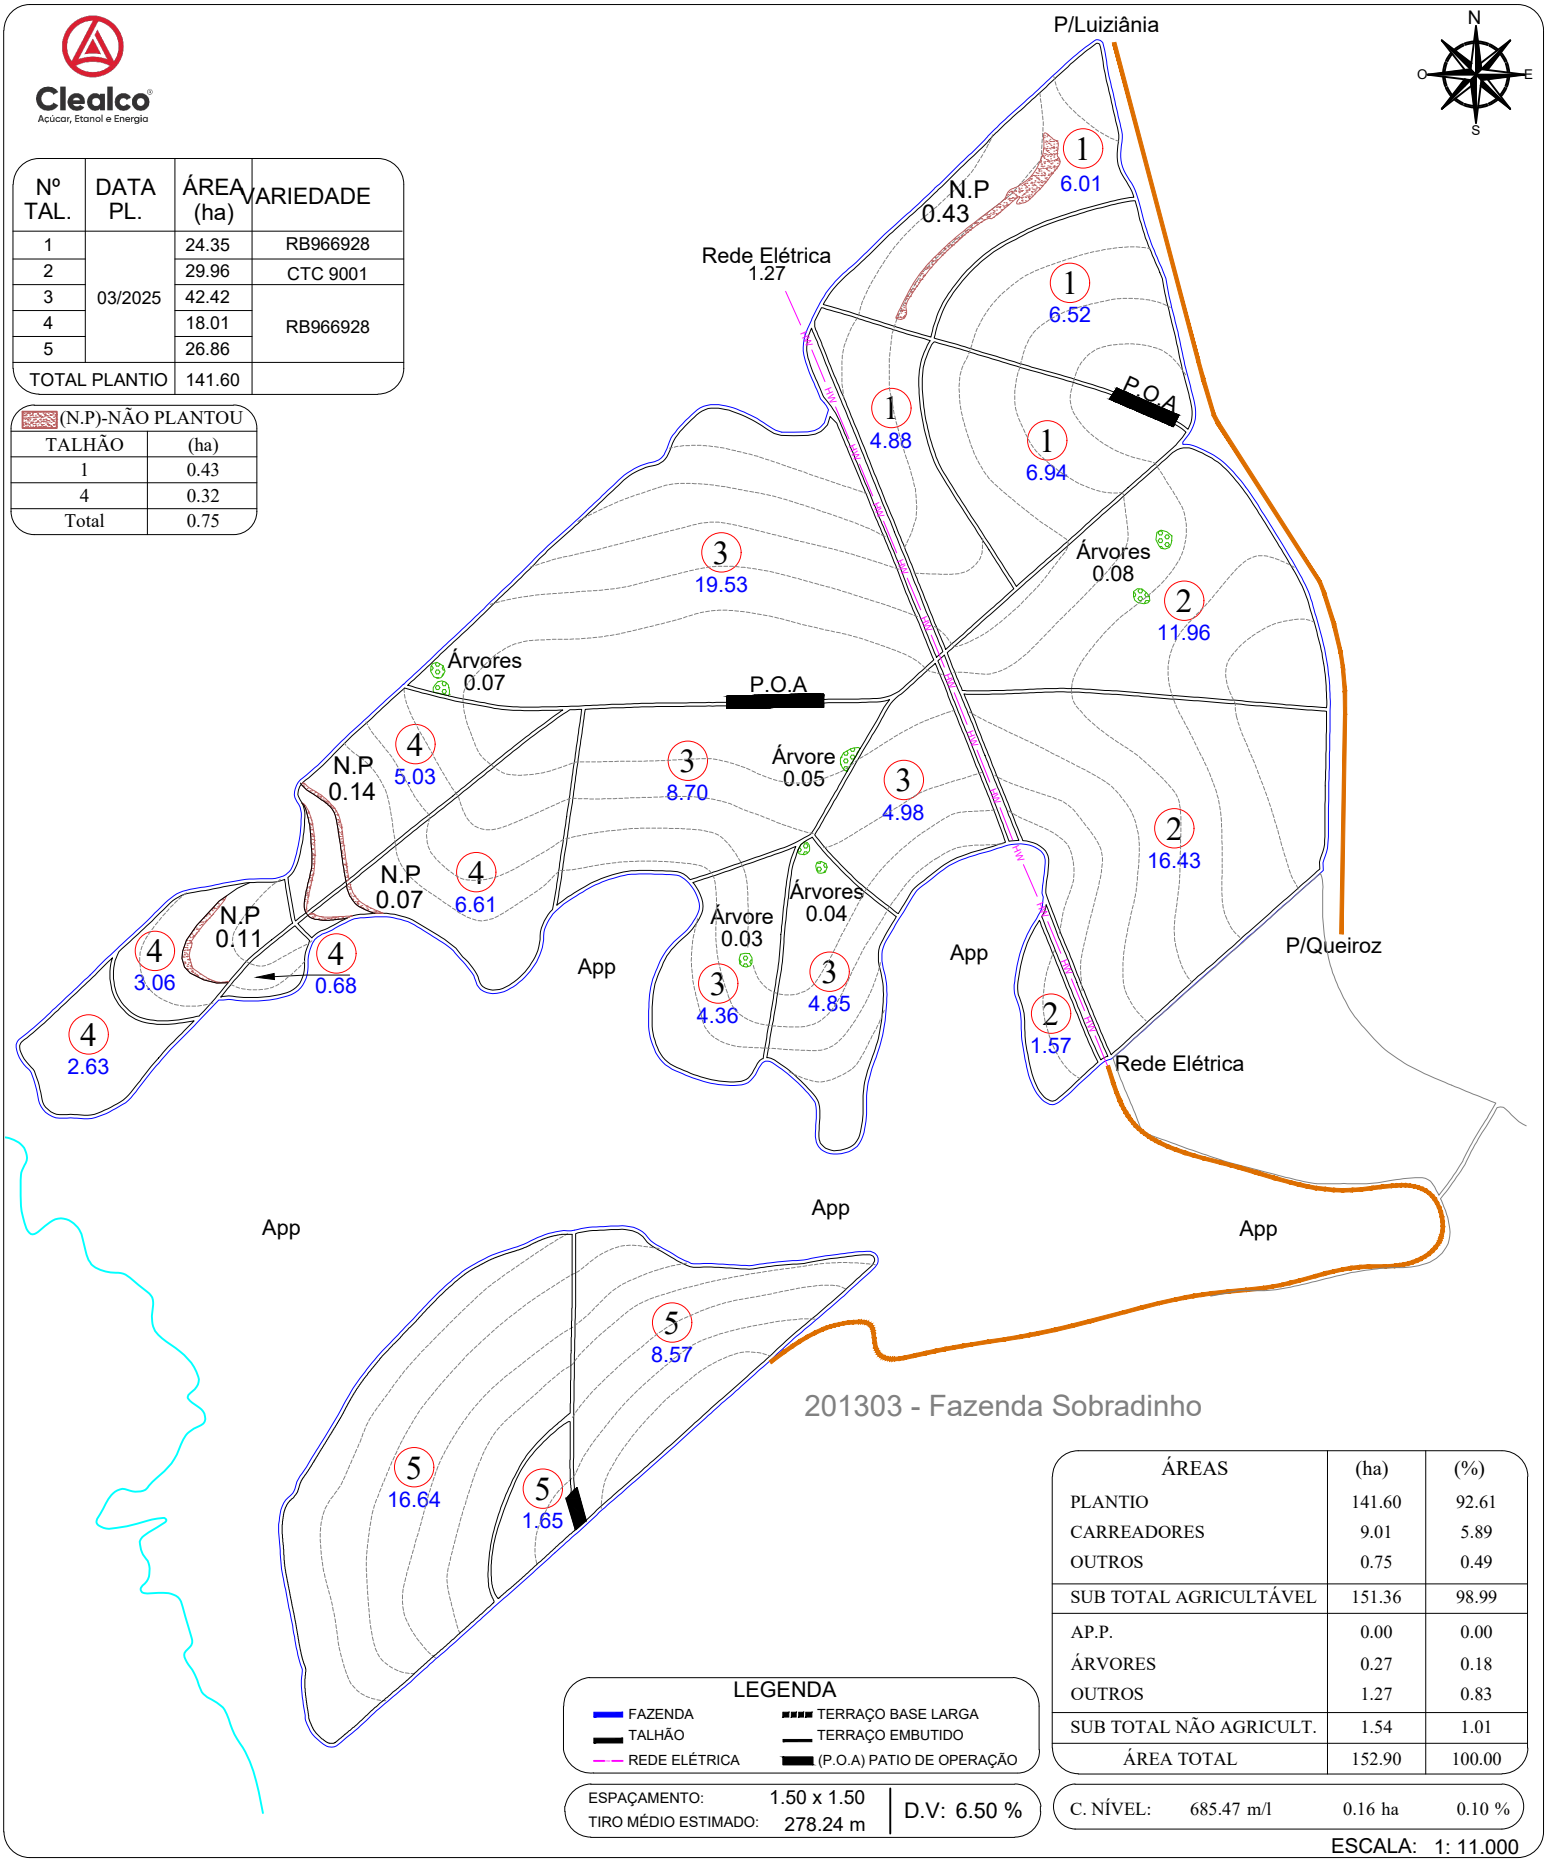

201303 - Fazenda Sobradinho

ÁREAS	(ha)	(%)
PLANTIO	141.60	92.61
CARREADORES	9.01	5.89
OUTROS	0.75	0.49
SUB TOTAL AGRICULTÁVEL	151.36	98.99
AP.P.	0.00	0.00
ÁRVORES	0.27	0.18
OUTROS	1.27	0.83
SUB TOTAL NÃO AGRICULT.	1.54	1.01
ÁREA TOTAL	152.90	100.00


LEGENDA
- FAZENDA
- TALHÃO
- REDE ELÉTRICA
- TERRAÇO BASE LARGA
- TERRAÇO EMBUTIDO
- (P.O.A) PATIO DE OPERAÇÃO

ESPAÇAMENTO: 1.50 x 1.50
TIRO MÉDIO ESTIMADO: 278.24 m
D.V: 6.50 %

C. NÍVEL: 685.47 m/l 0.16 ha 0.10 %

ESCALA: 1: 11.000

CROQUI DE ACESSO

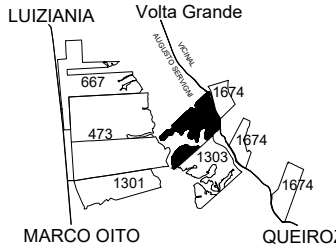

FAZENDA SÃO SEBASTIÃO

PROPRIETÁRIO: CLEALCO S/A
COMPRADOR: CLEALCO S/A
MUNICÍPIO: QUEIROZ - SP

DISTÂNCIAS (km):
UNID. I - Asfalto: 46.50 Terra.: 1.00
UNID.I I - Asfalto: 13.00 Terra.: 1.00

COORDENADAS: E(X): 574051.31 N(Y): 7593554.67
LAT: -21°45'36.3591" LONG: -50°17'1.6996"

CLEALCO - AÇÚCAR E ALCOOL S/A - DEPARTAMENTO DE GEOTECNOLOGIA

UNIDADE: II
PARTE: A/A
FUNDO AGRÍCOLA: 100646

M:\01-Mapa de safra\Mapas Atualizados\Clealco\100646 - Fazenda São Sebastião (Clealco)\100646 - Fazenda São Sebastião - Clealco.dwg

Bruno Gamboa 02/07/25