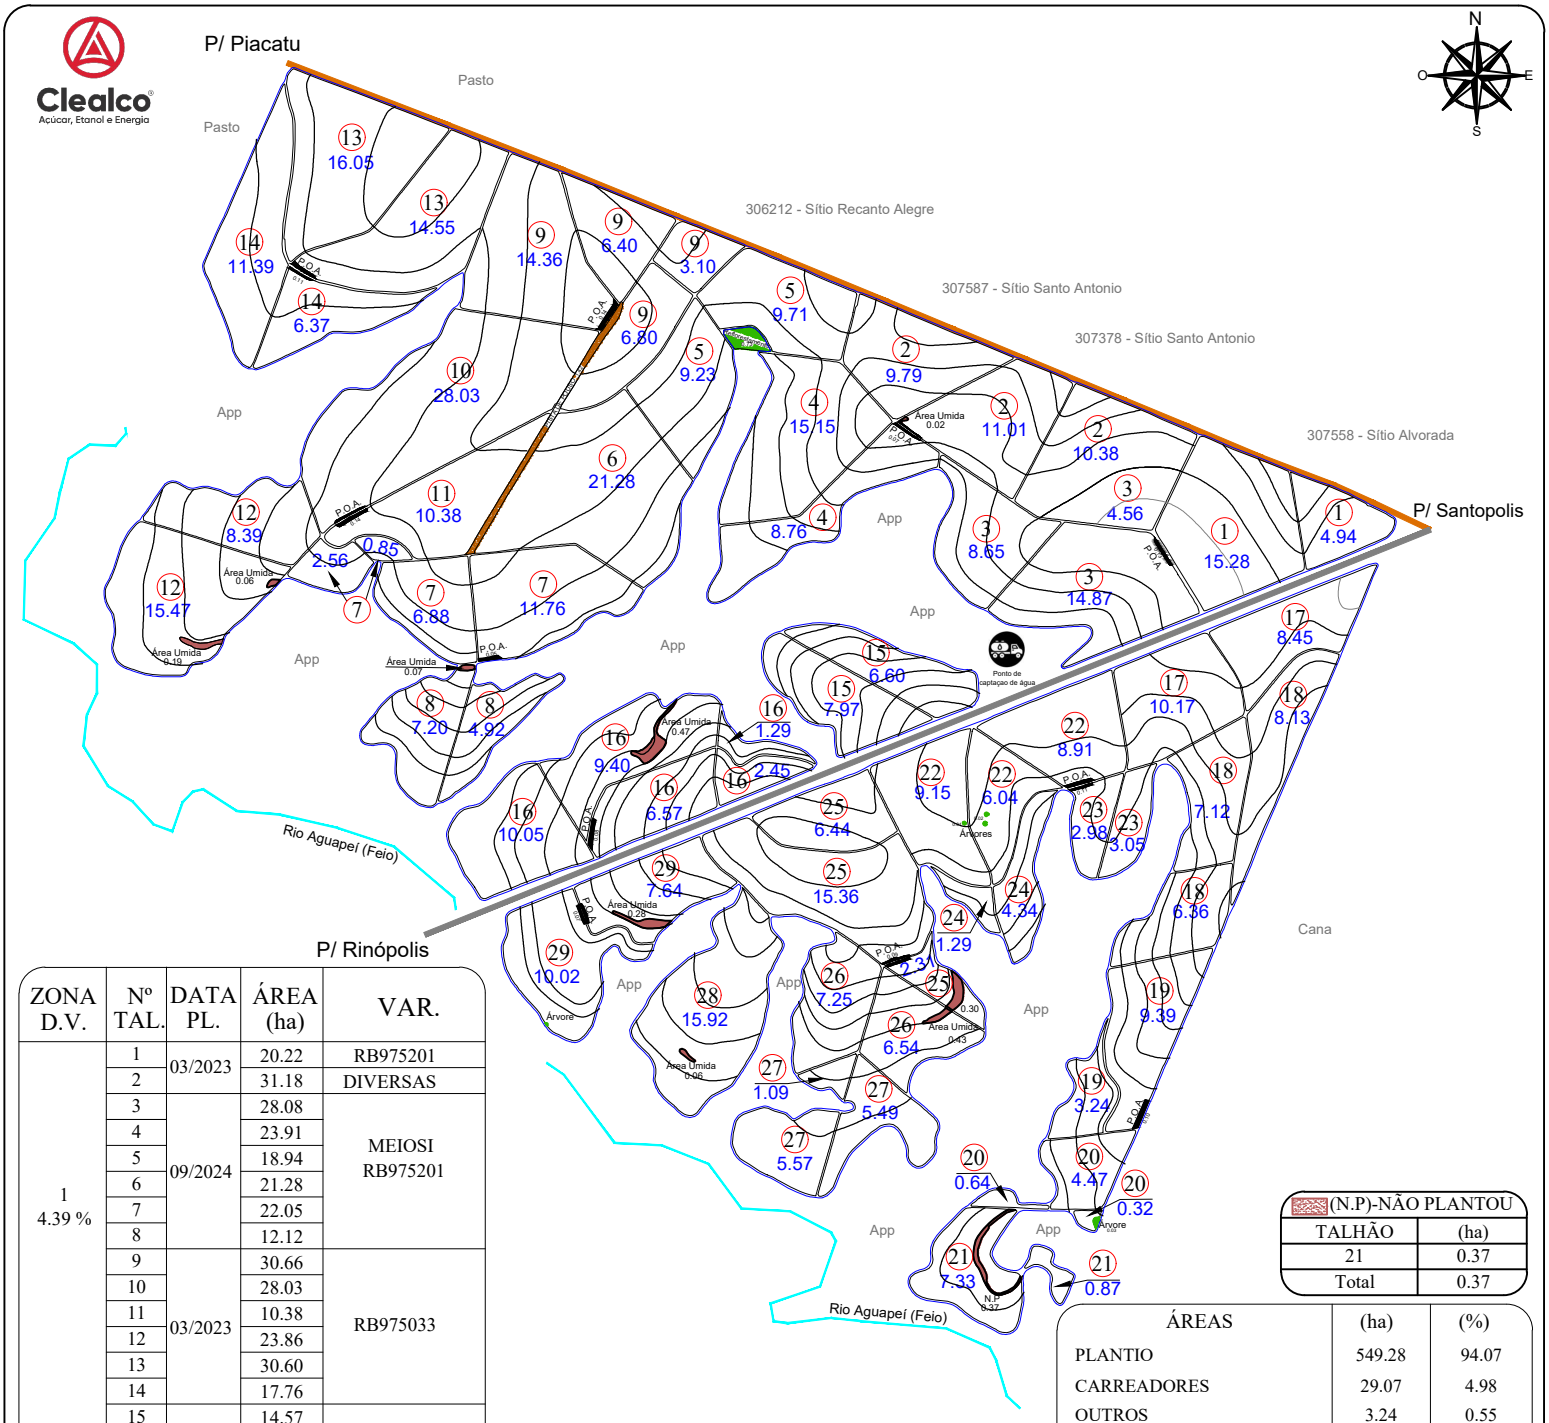


ZONA D.V.	Nº TAL.	DATA PL.	ÁREA (ha)	VAR.
1 4.39 %	1	03/2023	20.22	RB975201
	2		31.18	DIVERSAS
	3	09/2024	28.08	MEIOSI RB975201
	4		23.91	
	5		18.94	
	6		21.28	
	7		22.05	
	8		12.12	
	9	03/2023	30.66	RB975033
	10		28.03	
	11		10.38	
	12		23.86	
	13		30.60	
	14		17.76	
	15	07/2023	14.57	RB975242
	16		29.76	
2 4.39 %	17	06/2023	18.62	RB975242
	18		21.61	
	19		12.63	RB975201
	20		5.43	
	21		8.20	
	22		24.10	RB975242
	23		6.03	
	24		5.63	
	25		24.11	RB975201
	26		13.79	RB985476
	27		12.15	
	28		15.92	
	29		17.66	
TOTAL PLANTIO			549.28	--------

ESCALA: 1: 23.000

(N.P)-NÃO PLANTOU	
TALHÃO	(ha)
21	0.37
Total	0.37

ÁREAS	(ha)	(%)
PLANTIO	549.28	94.07
CARREADORES	29.07	4.98
OUTROS	3.24	0.55
SUB TOTAL AGRICULTÁVEL	581.59	99.60
AP.P.	0.00	0.00
ÁRVORES	0.06	0.01
OUTROS	2.25	0.39
SUB TOTAL NÃO AGRICULT.	2.31	0.40
ÁREA TOTAL	583.90	100.00


C. NÍVEL: 56400.87 m/l 12.97 ha 2.22 %

LEGENDA

- FAZENDA
- TALHÃO
- REDE ELÉTRICA
- VAZIO
- TERRAÇO BASE LARGA
- TERRAÇO EMBUTIDO
- (P.O.A) PATIO DE OPERAÇÃO
- CARREGADO

ESPAÇAMENTO: 1.50 x 1.50
TIRO MÉDIO ESTIMADO: 264.24 m
D.V: 4.39 %

CROQUI DE ACESSO

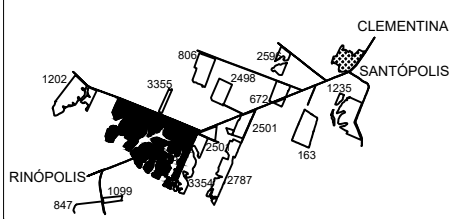

FAZENDA SÃO JOÃO

PROPRIETÁRIO: CLEALCO S/A
COMPRADOR: CLEALCO
MUNICÍPIO: SANTÓPOLIS - SP

DISTÂNCIAS (km):
UNID. I - Asfalto: 20.00 Terra.: 2.00
UNID.I I - Asfalto: 55.00 Terra.: 2.00

COORDENADAS: E(X): 543089.74 N(Y): 7603376.44
LAT: -21°40'20.6000" LONG: -50°35'0.6021"

CLEALCO - AÇÚCAR E ALCOOL S/A - DEPARTAMENTO DE GEOTECNOLOGIA

LEVANTAMENTO VIA:
- SATÉLITE
- GPS / VANT
- GOOGLE

UNIDADE: I
PARTE: A/A
FUNDO AGRÍCOLA: 200036

M:\01-Mapa de safra\Mapas Atualizados\Clealco\200036 - Fazenda São João (Clealco)\200036 - Fazenda São João.dwg

Peterson Santos 25/05/2026