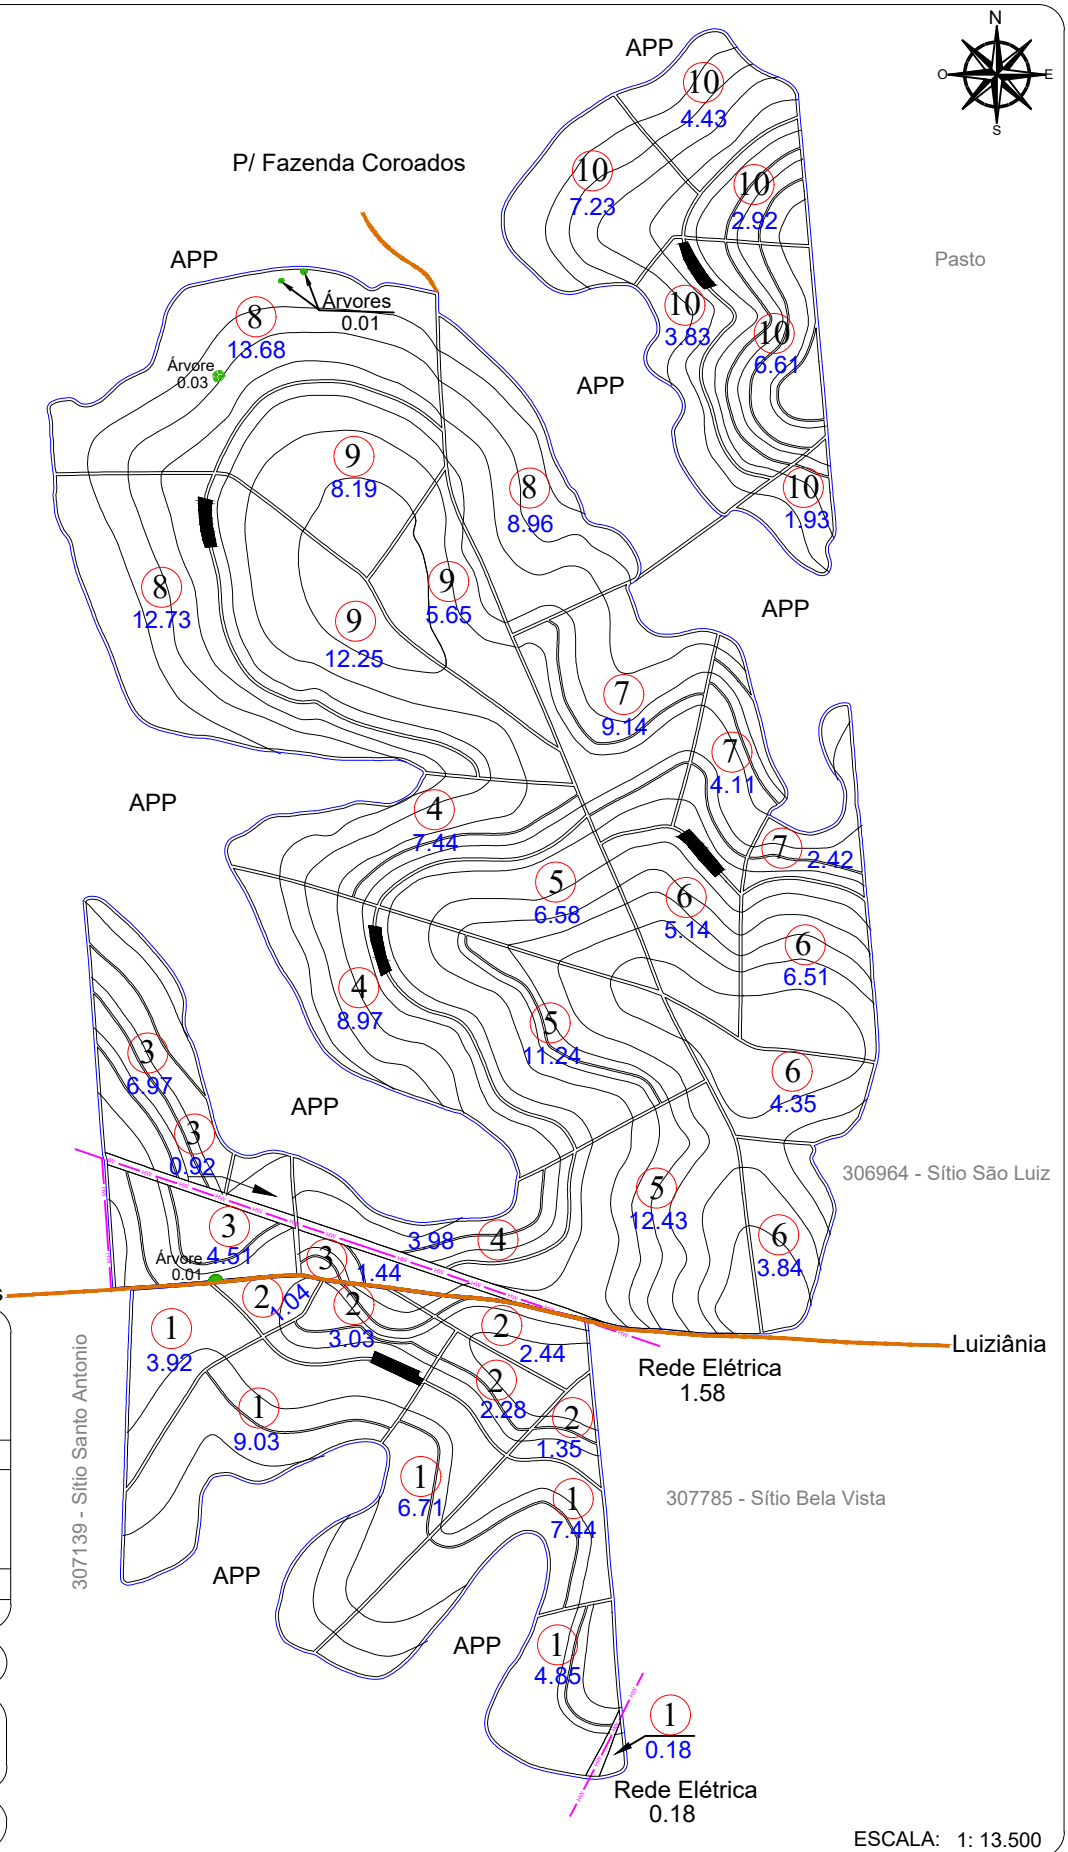


Nº TAL.	DATA PL.	ÁREA (ha)	VARIEDADE
1	06/2022	32.13	RB975033
2		10.14	
3		13.84	
4		20.39	
5		30.25	
6		19.84	
7		15.67	
8		35.37	
9		26.09	
10		26.95	
TOTAL PLANTIO		230.67	

ÁREAS	(ha)	(%)
PLANTIO	230.67	92.42
CARREADORES	16.20	6.49
(P.O.A) Patio de Operação Agrícola	0.90	0.36
SUB TOTAL AGRICULTÁVEL	247.77	99.27
AP.P.	0.00	0.00
ÁRVORES	0.05	0.02
REDE ELÉTRICA	1.76	0.71
SUB TOTAL NÃO AGRICULT.	1.81	0.73
ÁREA TOTAL	249.58	100.00

C. NÍVEL: 41428.83 m/l | 9.53 ha | 3.82 %


LEGENDA

- FAZENDA
- TALHÃO
- REDE ELÉTRICA
- TERRAÇO BASE LARGA
- TERRAÇO EMBUTIDO
- (P.O.A) PATIO DE OPERAÇÃO

ESPAÇAMENTO: 1.50 x 1.50
TIRO MÉDIO ESTIMADO: 226.12 m
D.V: 7.52 %

ESCALA: 1: 13.500

CROQUI DE ACESSO

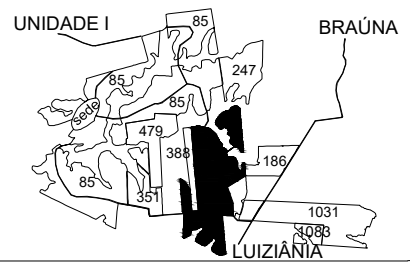

FAZENDA SÃO BOM JESUS DOS PASSOS

PROPRIETÁRIO: SILVIA JUNQUEIRA REIS
COMPRADOR: CLEALCO
MUNICÍPIO: BRAÚNA - SP

DISTÂNCIAS (km):
UNID. I - Asfalto: 0.00 Terra.: 9.80
UNID.I I - Asfalto: 30.00 Terra.: 8.00

COORDENADAS: E(X): 564806.46 N(Y): 7609528.11
LAT: -21°36'58.1498" LONG: -50°22'25.8147"

CLEALCO - AÇÚCAR E ALCOOL S/A - DEPARTAMENTO DE GEOTECNOLOGIA

LEVANTAMENTO VIA:
SATÉLITE
GPS / VANT
GOOGLE

UNIDADE: I
PARTE: A/A
FUNDO AGRÍCOLA: 200106

M:\01-Mapa de safra\Mapas Atualizados\Clealco\200106 - Fazenda São Bom Jesus dos Passos (Silvia Junqueira Reis)\200106 - Fazenda São Bom Jesus dos Passos (Silvia Junqueira Reis).dwg

Bruno Gamboa 19/08/25