D.V.	Nº TAL.	DATA PL.	ÁREA (ha)	VAR.
4.96%	1	10/2023	3.83	RB 975201
	2		12.92	
	3		8.74	
TOTAL PLANTIO			25.49	--------


ÁREAS	(ha)	(%)
PLANTIO	25.49	90.76
CARREADORES	2.57	9.16
OUTROS	0.00	0.00
SUB TOTAL AGRICULTÁVEL	28.06	99.93
AP.P.	0.00	0.00
ÁRVORES	0.01	0.04
OUTROS	0.01	0.04
SUB TOTAL NÃO AGRICULT.	0.02	0.07
ÁREA TOTAL	28.08	100.00

C. NÍVEL: 0.00 m/l 0.00 ha 0.00 %


LEGENDA

- FAZENDA
- TALHÃO
- CURVA DE NÍVEL
- CARREADOR
- CONFRONTANTE
- REDE ELÉTRICA
- TRAJETO VAZIO
- TRAJETO CARREGADO

PLANTIO MANUAL - ESPAÇAMENTO: 1.50 X 1.50
TIRO MÉDIO ESTIMADO: 165.01 m

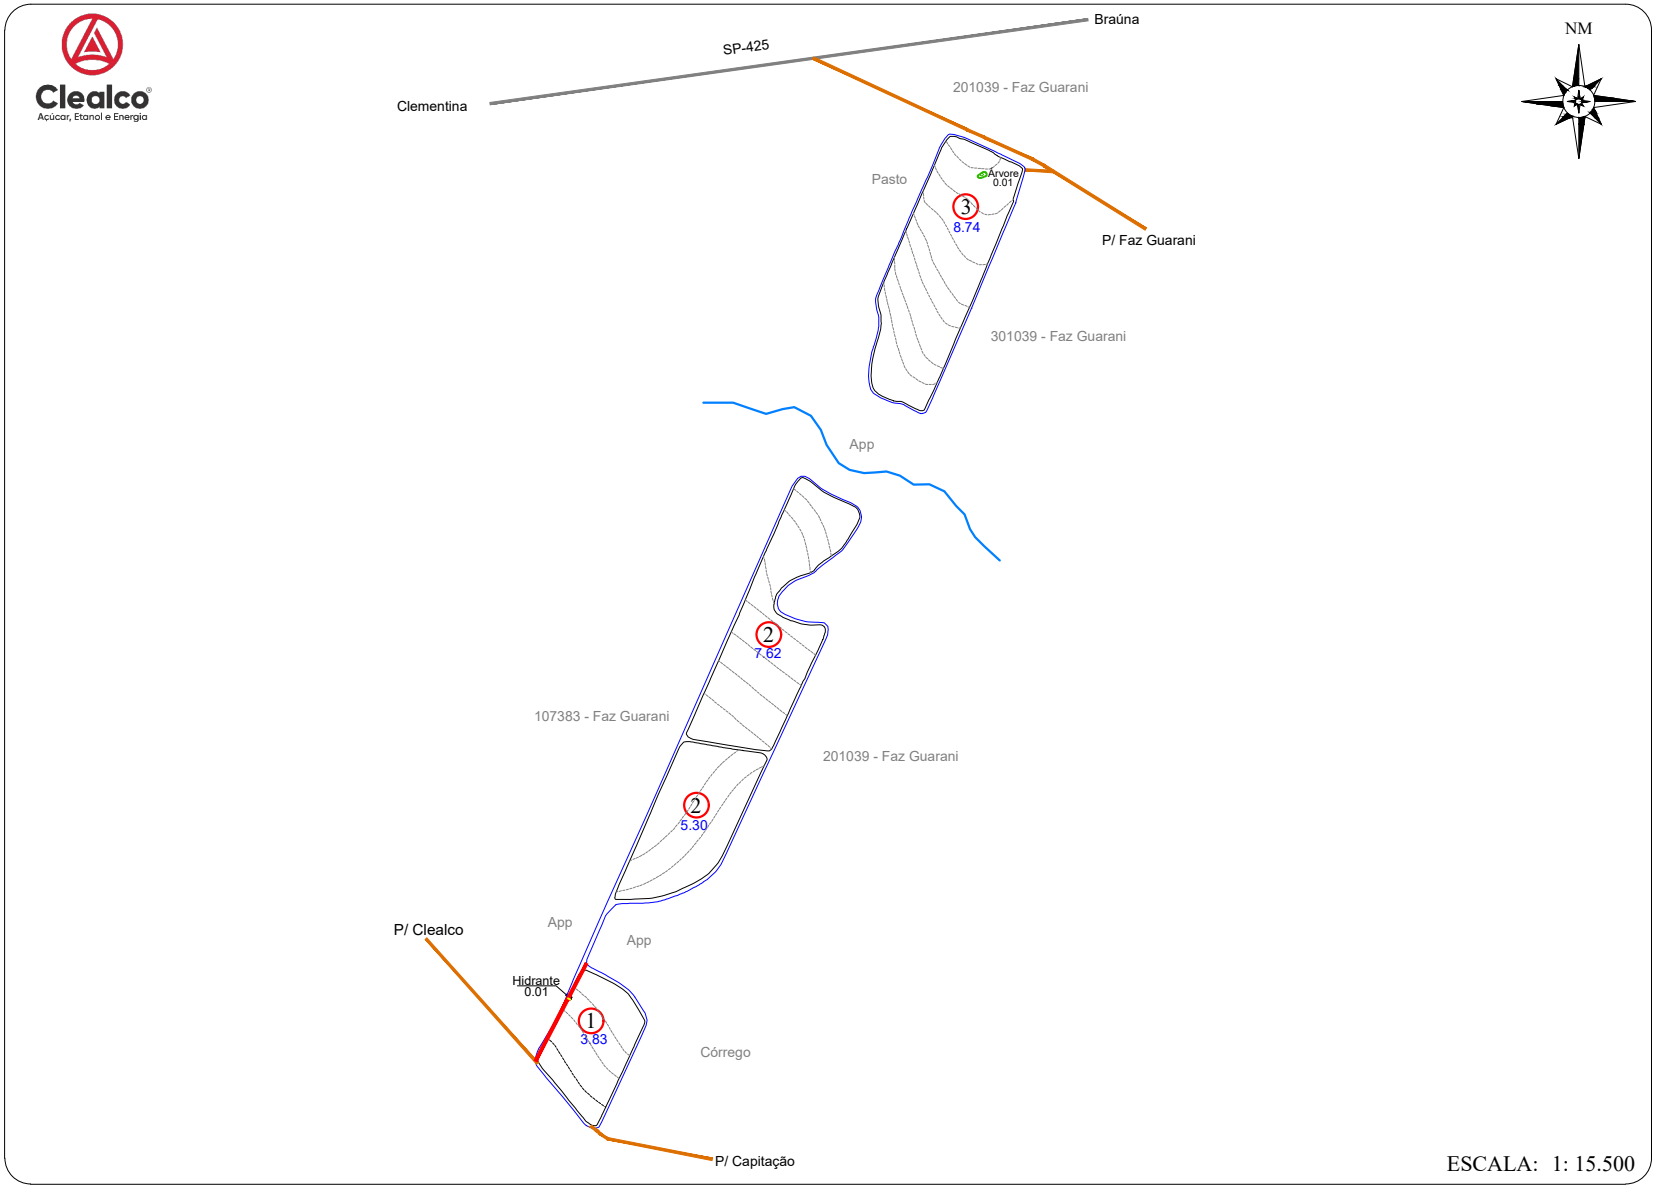

CROQUI DE ACESSO

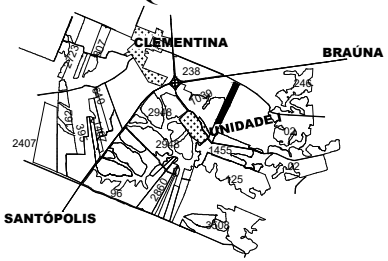

SÍTIO GUARANI

PROPRIETÁRIO: BENVINDA PAULINA DA SILVA
COMPRADOR: CLEALCO S/A
MUNICÍPIO: CLEMENTINA - SP

DISTÂNCIAS (km):
UNID. I - Asfalto: 0.40 Terra.: 1.60
UNID.I I - Asfalto: 58.00 Terra.: 1.60
UNID. III -Asfalto: 56.00 Terra.: 1.60

COORDENADAS: E(X): 559666.63 N(Y): 7613445.93
LAT: -21°34'51.3716" LONG: -50°25'25.0928"

CLEALCO - AÇÚCAR E ALCOOL S/A - DEPARTAMENTO DE TOPOGRAFIA

UNIDADE:
I
PARTE:
A/A
FUNDO AGRÍCOLA:
200349