ZONA D.V.	Nº TAL.	DATA PL.	ÁREA (ha)	VARIEDADE
1 4.61 %	1	04/2023	4.85	CTC 2944
	2		11.43	IACSP01-5503
	3		5.71	DIVERSAS
	4		11.49	RB 975242
	5		6.19	
	6	03/2023	22.86	RB975201
	7		15.69	
	8		15.14	
	9		5.56	
	10		14.12	DIVERSAS
	11		15.95	
	12		7.94	RB975201
	13		10.68	
TOTAL PLANTIO			147.61	--------


ÁREAS	(ha)	(%)
PLANTIO	147.61	92.67
CARREADORES	10.90	6.84
OUTROS	0.50	0.31
SUB TOTAL AGRICULTÁVEL	159.01	99.82
AP.P.	0.00	0.00
ÁRVORES	0.16	0.10
OUTROS	0.12	0.08
SUB TOTAL NÃO AGRICULT.	0.28	0.18
ÁREA TOTAL	159.29	100.00

C. NÍVEL: 2470.27 m/l 0.57 ha 0.36 %


LEGENDA

- FAZENDA
- TALHÃO
- CURVA DE NÍVEL
- CARREADOR
- CONFRONTANTE
- REDE ELÉTRICA
- TRAJETO VAZIO
- TRAJETO CARREGADO

PLANTIO MANUAL - ESPAÇAMENTO: 1.50 X 1.50
TIRO MÉDIO ESTIMADO: 234.47 m

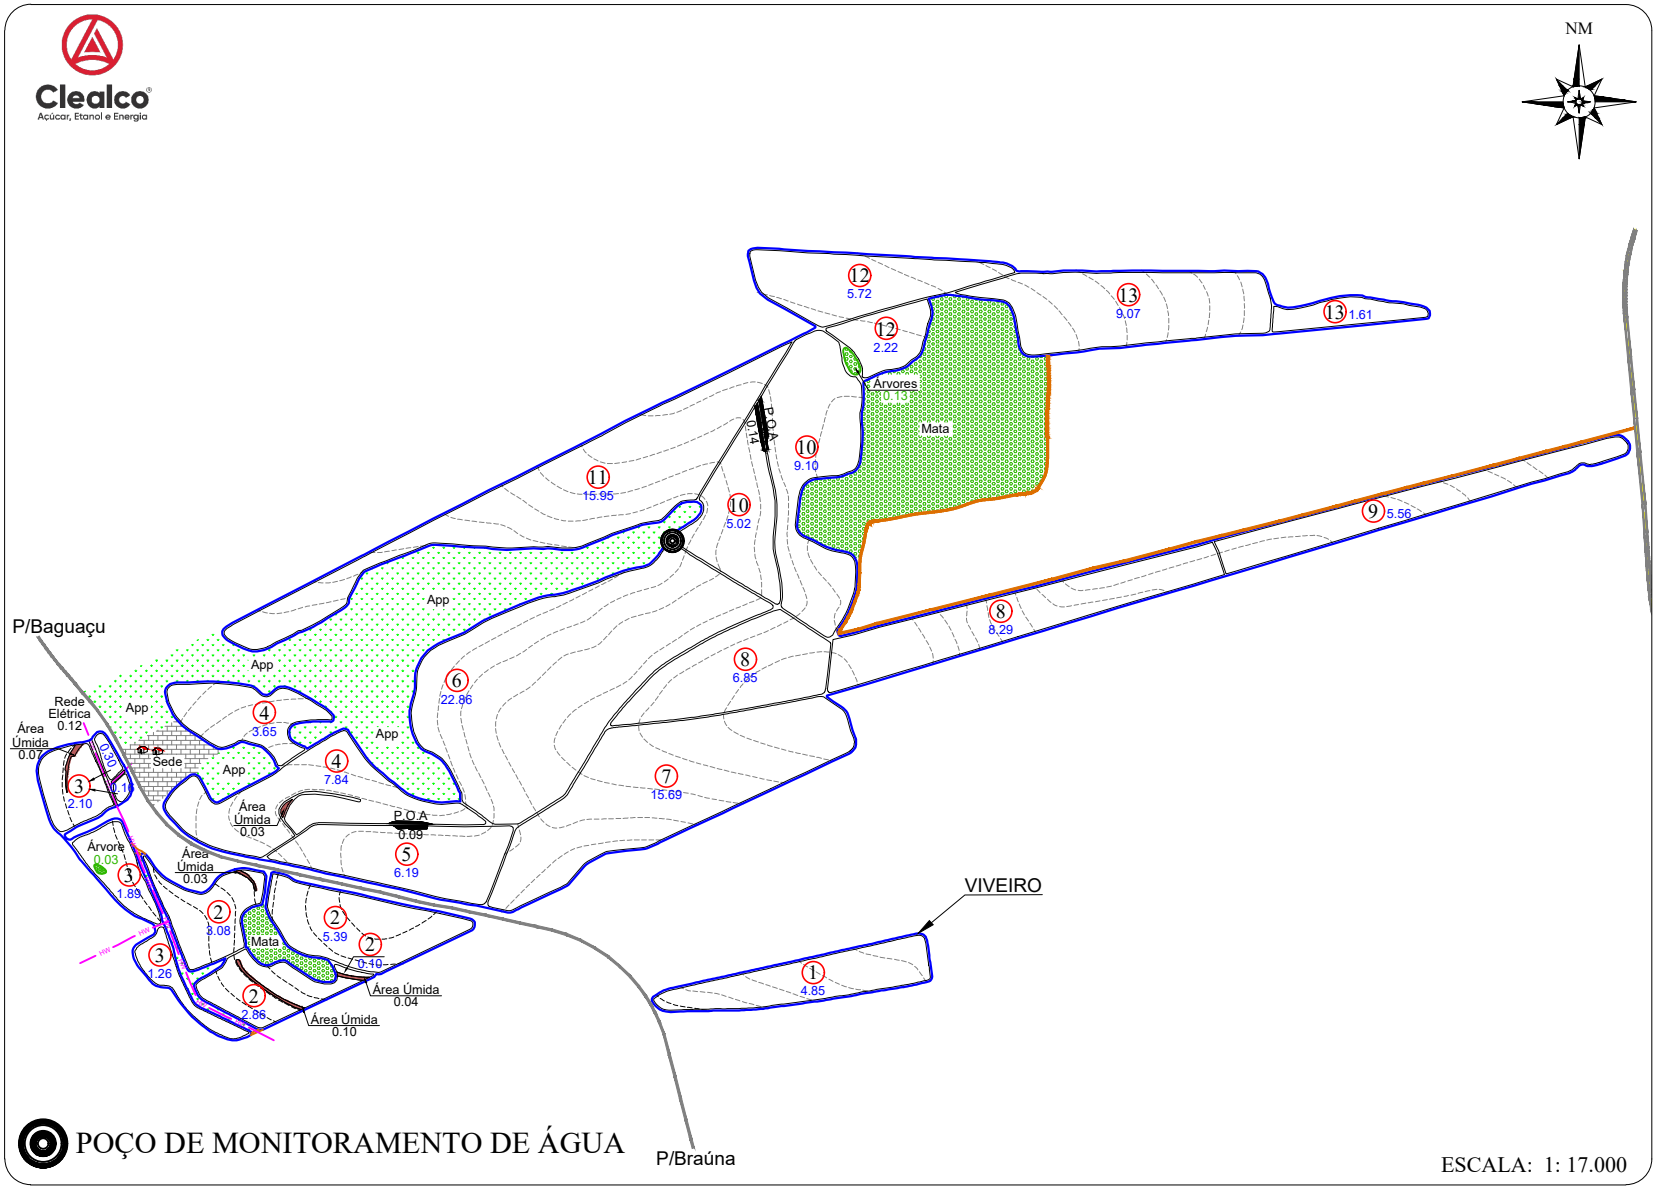

CROQUI DE ACESSO

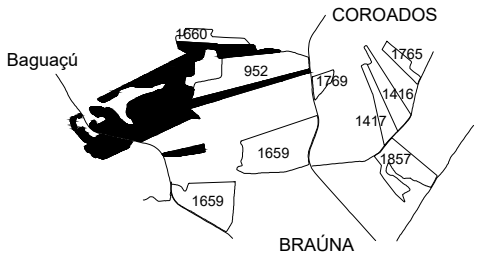

FAZENDA SAN MIGUEL

PROPRIETÁRIO: JUVENAL SAN MIGUEL
COMPRADOR: CLEALCO S/A
MUNICÍPIO: COROADOS

DISTÂNCIAS (km):
UNID. I - Asfalto: 25.00 Terra.: 0.50
UNID.I I - Asfalto: 73.00 Terra.: 1.50
UNID. III -Asfalto: 26.50 Terra.: 10.50

COORDENADAS: E(X): 568725.92 N(Y): 7625075.95
LAT: -21°28'31.9426" LONG: -50°20'11.7894"

CLEALCO - AÇÚCAR E ALCOOL S/A - DEPARTAMENTO DE TOPOGRAFIA

UNIDADE: I
PARTE: A/A
FUNDO AGRÍCOLA: 200365