D.V.	Nº TAL.	DATA PL.	ÁREA (ha)	VAR.
4.70%	1	05/2023	20.82	IACSP01-5503
	2		36.92	DIVERSAS
	3		18.67	RB 92579
	4		37.35	
	5		22.94	
	6		19.88	
	7		7.71	IACSP01-5503
	8		33.69	DIVERSAS
	9		45.84	
	10		19.95	
	11		35.68	
	12		26.12	
TOTAL PLANTIO			325.57	--------

ÁREAS	(ha)	(%)
PLANTIO	325.57	91.94
CARREADORES	19.73	5.57
OUTROS	0.56	0.16
SUB TOTAL AGRICULTÁVEL	345.86	97.67
AP.P.	5.10	1.44
ÁRVORES	0.33	0.09
OUTROS	2.83	0.80
SUB TOTAL NÃO AGRICULT.	8.26	2.33
ÁREA TOTAL	354.12	100.00

C. NÍVEL: 39554.59 m/l 9.10 ha 2.57 %


LEGENDA

- FAZENDA
- TALHÃO
- CURVA DE NÍVEL
- CARREADOR
- CONFRONTANTE
- REDE ELÉTRICA
- TRAJETO VAZIO
- TRAJETO CARREGADO

PLANTIO MANUAL - ESPAÇAMENTO: 1.50 X 1.50
TIRO MÉDIO ESTIMADO: 000.00m


Clealco
Açúcar, Etanol e Energia

6328 - Fazenda Vo Eduardo

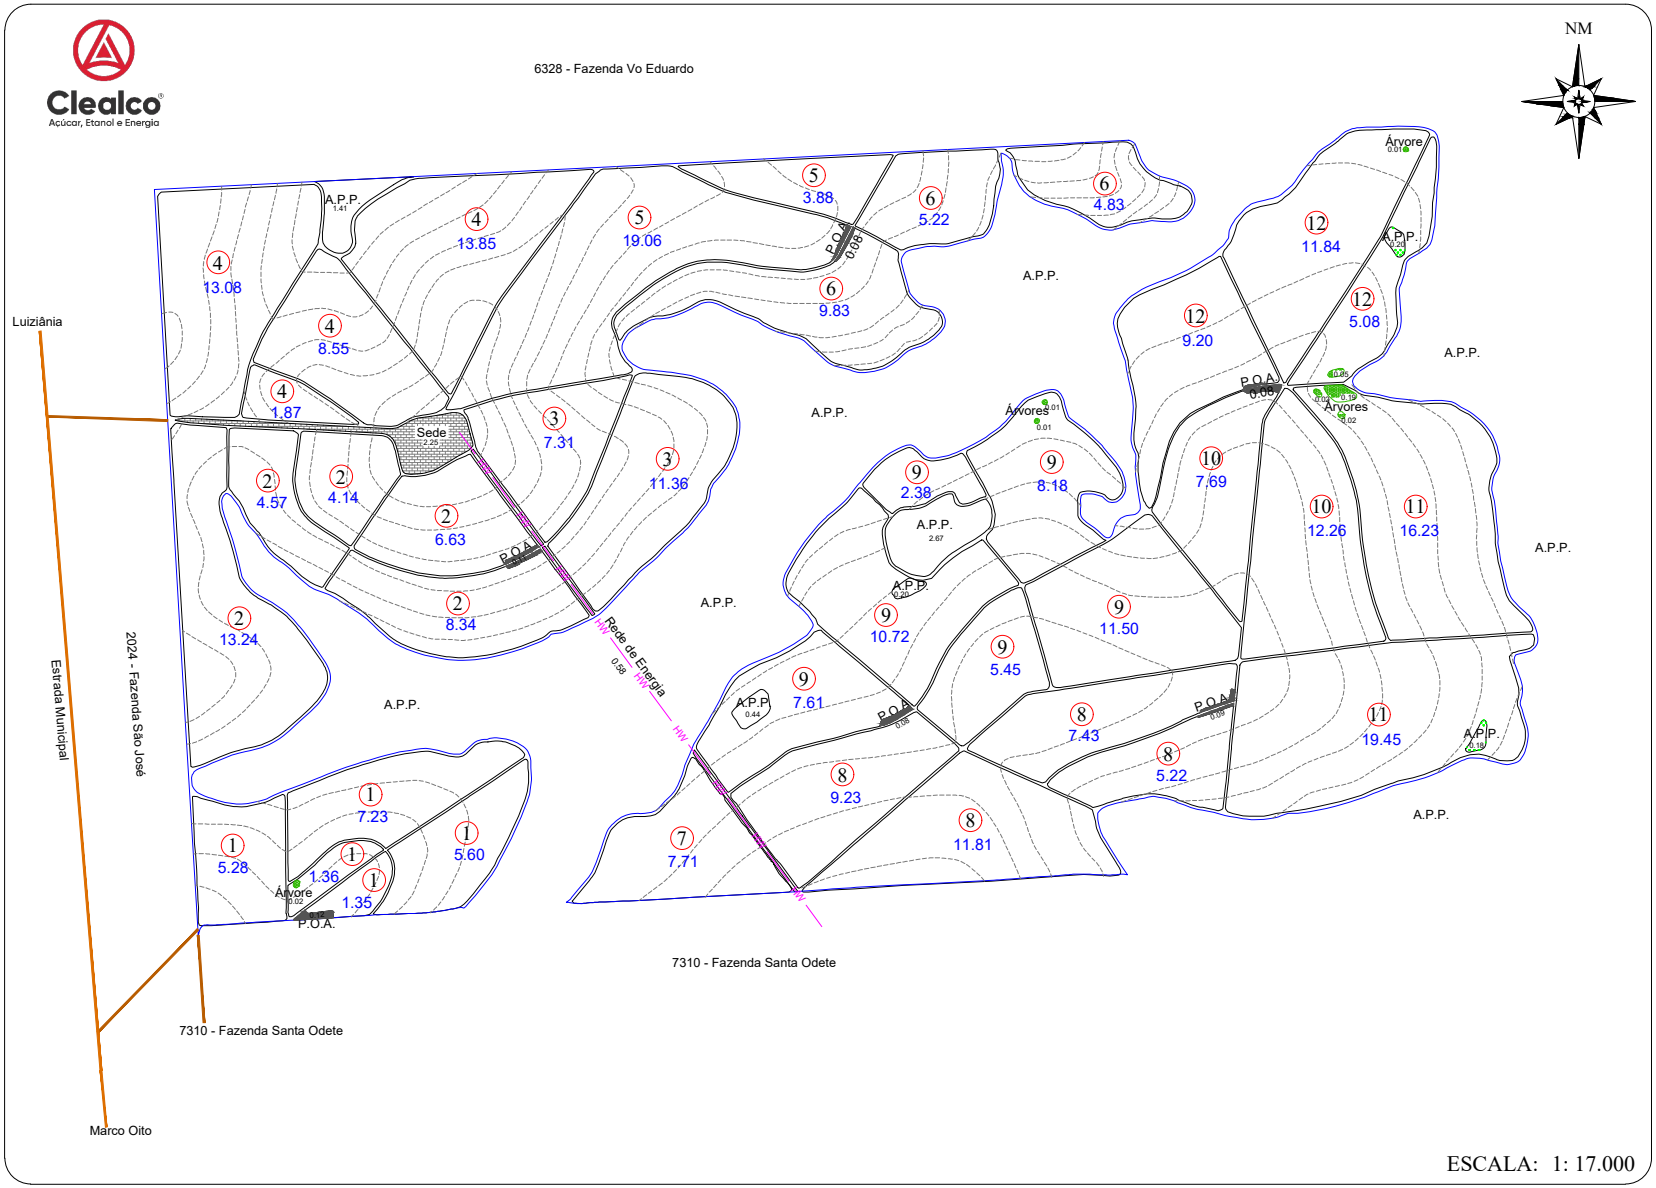

ESCALA: 1: 17.000

CROQUI DE ACESSO

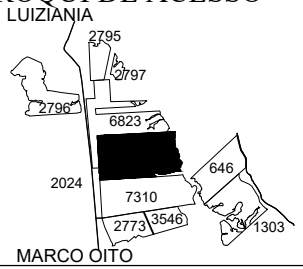

FAZENDA SANTA ODETE

PROPRIETÁRIO: MARIA DA P. Z. CINTRA
ARRENDATÁRIO: CLEALCO S/A
MUNICÍPIO: QUEIROZ

DISTÂNCIAS (km):

UNID. I -	Asfalto:	32.80	Terra.:	11.00
UNID.I I -	Asfalto:	17.00	Terra.:	15.40
UNID. III -	Asfalto:	34.00	Terra.:	12.60

COORDENADAS: E(X): 571712.7731 N(Y): 7594673.348
LAT: 21°45'0,3231" LONG: 50°18'23,2922"

CLEALCO - AÇÚCAR E ALCOOL S/A - DEPARTAMENTO DE TOPOGRAFIA

UNIDADE: II

PARTE: A/A

FUNDO AGRÍCOLA: 200473