
Clealco
Açúcar, Etanol e Energia

ÁREAS	(ha)	(%)
PLANTIO	1224.89	92.32
CARREADORES	88.31	6.66
OUTROS	4.27	0.32
SUB TOTAL AGRICULTÁVEL	1317.47	99.30
AP.P.	1.95	0.15
ÁRVORES	0.21	0.02
OUTROS	7.11	0.54
SUB TOTAL NÃO AGRICULT.	9.27	0.70
ÁREA TOTAL	1326.74	100.00

(N.P)-NÃO PLANTOU

TALHÃO	(ha)
1	1.04
2	3.04
3	4.14
4	2.14
5	1.22
32	1.14
33	1.12
34	1.33
35	1.72
36	2.27
37	1.78
38	1.85
39	3.31
Total	26.10

Zona	Nº TAL.	DATA PL.	ÁREA (ha)	VARIEDADE
1	1	04/2022	16.86	RB975242
	2		36.81	
	3		30.30	
	4		19.56	
	5		22.75	
	6		4.52	
	7	05/2025	64.30	RB96 6928
	8		26.82	
	9	04/2022	49.75	RB 975242
	10		21.64	
	11		15.98	
	12	05/2025	13.20	RB96 6928
	13	04/2022	52.41	RB 975242
	14		59.91	
	15		17.20	
	16		38.27	
	17	2026	23.39	PRÉ PLANTIO
	18		37.71	
	19	04/2021	32.53	RB 975242
	20		42.85	
	21		34.38	
	22		49.16	
	23		45.81	
	24		40.41	
	25		27.67	
	26		47.65	
	27		56.06	
	28		31.71	
	29		48.25	
	30		22.14	
	31		57.30	
2	32	03/2022	6.37	
	33		21.10	
	34		11.87	
	35		16.59	
	36		20.28	
	37		12.07	
	38		19.32	
	39		29.99	
TOTAL PLANTIO			1224.89	

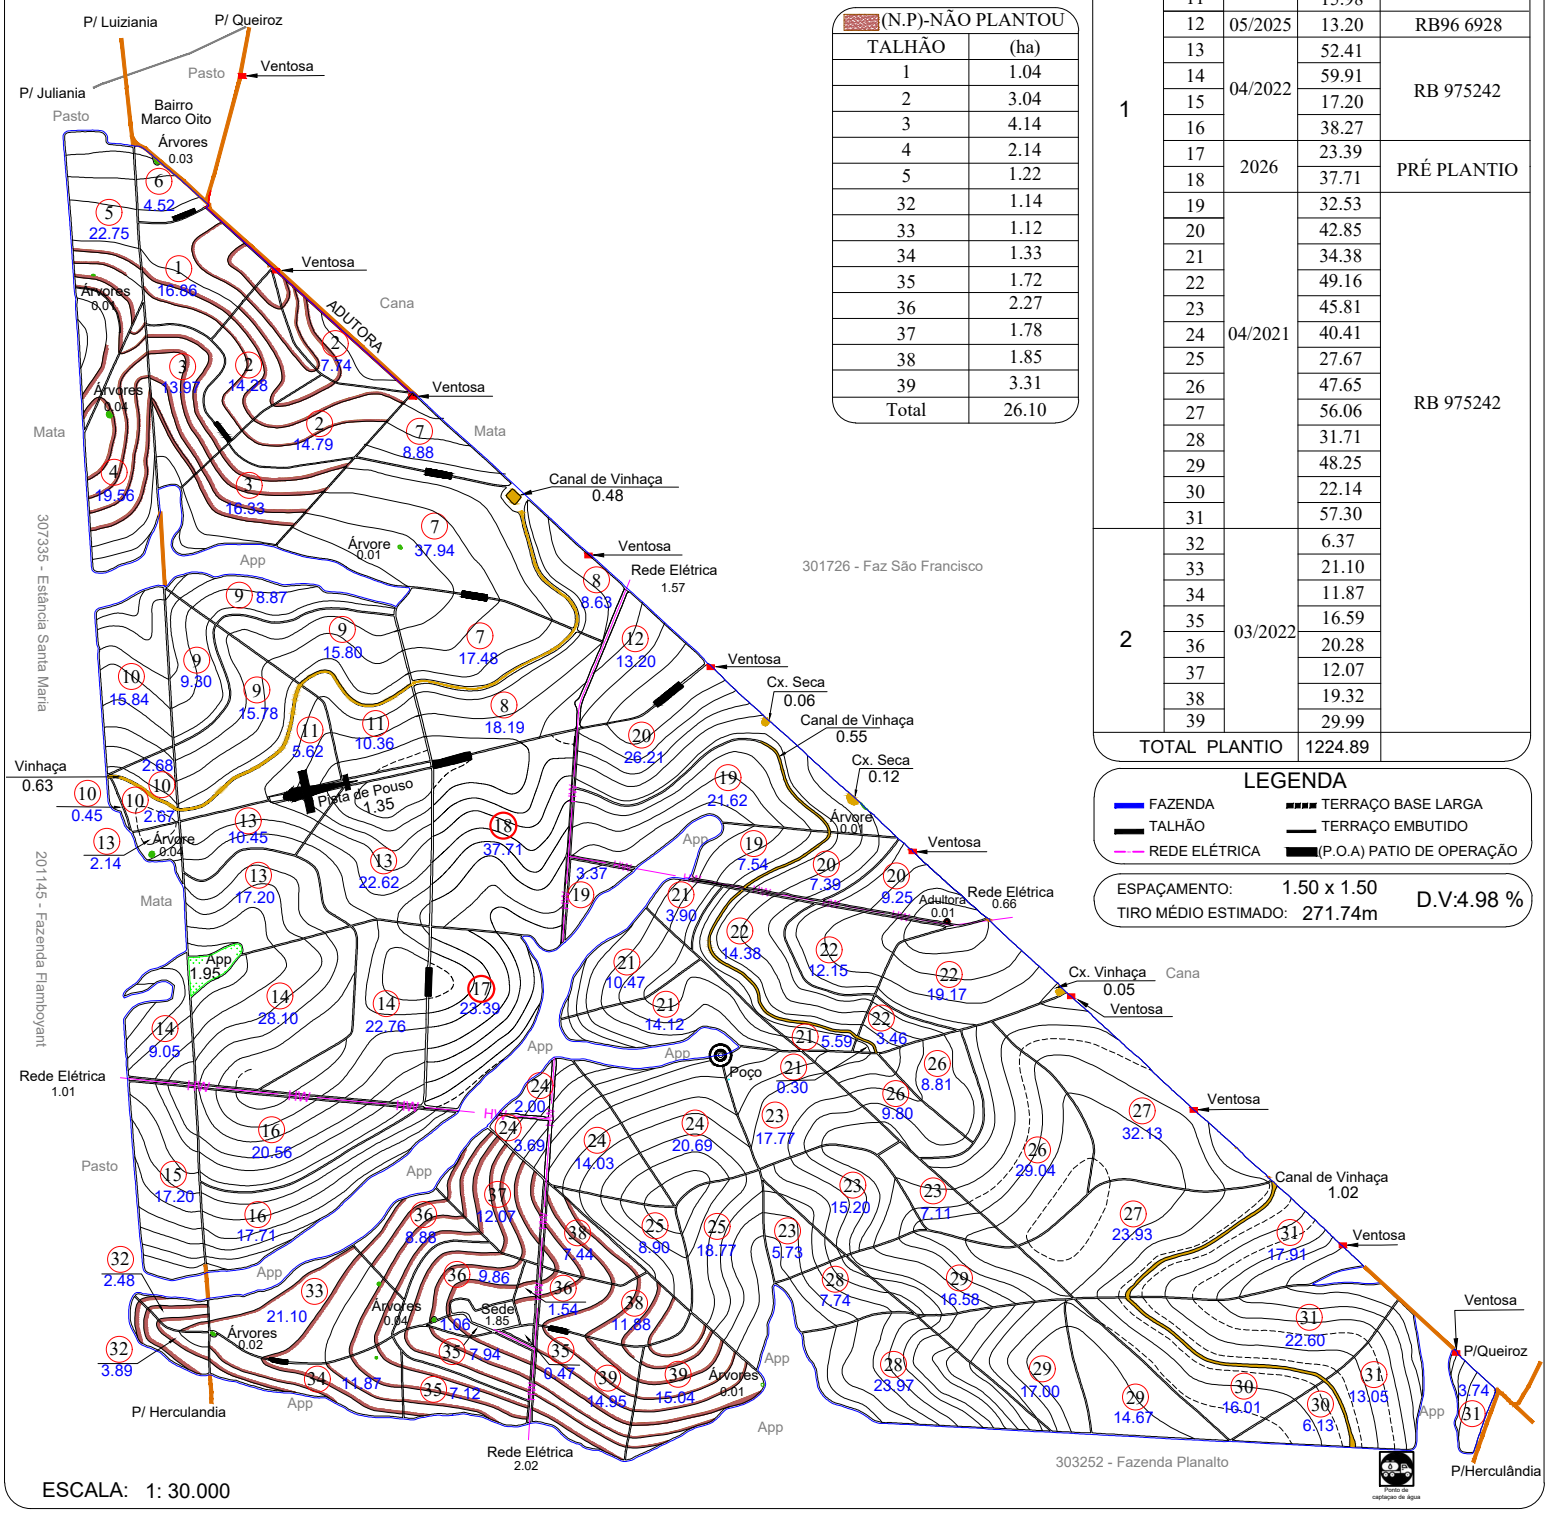


ESCALA: 1: 30.000

LEGENDA

- FAZENDA
- TALHÃO
- REDE ELÉTRICA
- TERRAÇO BASE LARGA
- TERRAÇO EMBUTIDO
- (P.O.A) PATIO DE OPERAÇÃO

ESPAÇAMENTO: 1.50 x 1.50
TIRO MÉDIO ESTIMADO: 271.74m
D.V:4.98 %

CROQUI DE ACESSO

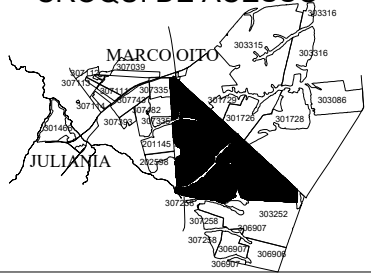

FAZENDA SANTA MARIA DO CARU

PROPRIETÁRIO: FRANCISCO CINTRA FRANCO
COMPRADOR: CLEALCO
MUNICÍPIO: HERCULANDIA - SP

DISTÂNCIAS (km):
UNID. I - Asfalto: 32.50 Terra.: 6.50
UNID.I I - Asfalto: 17.00 Terra.: 6.50

COORDENADAS: E(X): 569846.91 N(Y): 7580071.21
LAT: -21°52'55.4955" LONG: -50°19'26.0201"

CLEALCO - AÇÚCAR E ALCOOL S/A - DEPARTAMENTO DE GEOTECNOLOGIA

LEVANTAMENTO VIA:
SATÉLITE
GPS / VANT
GOOGLE

UNIDADE: II
PARTE: A/A
FUNDO AGRÍCOLA: 200506

M:\01-Mapa de safra\Mapas Atualizados\Clealco\200506 - Fazenda Santa Maria do Caru (Francisco Cintra Franco)\200506 - Fazenda Santa Maria do Caru (Francisco Cintra Franco).dwg

Peterson Santos 19/08/2026